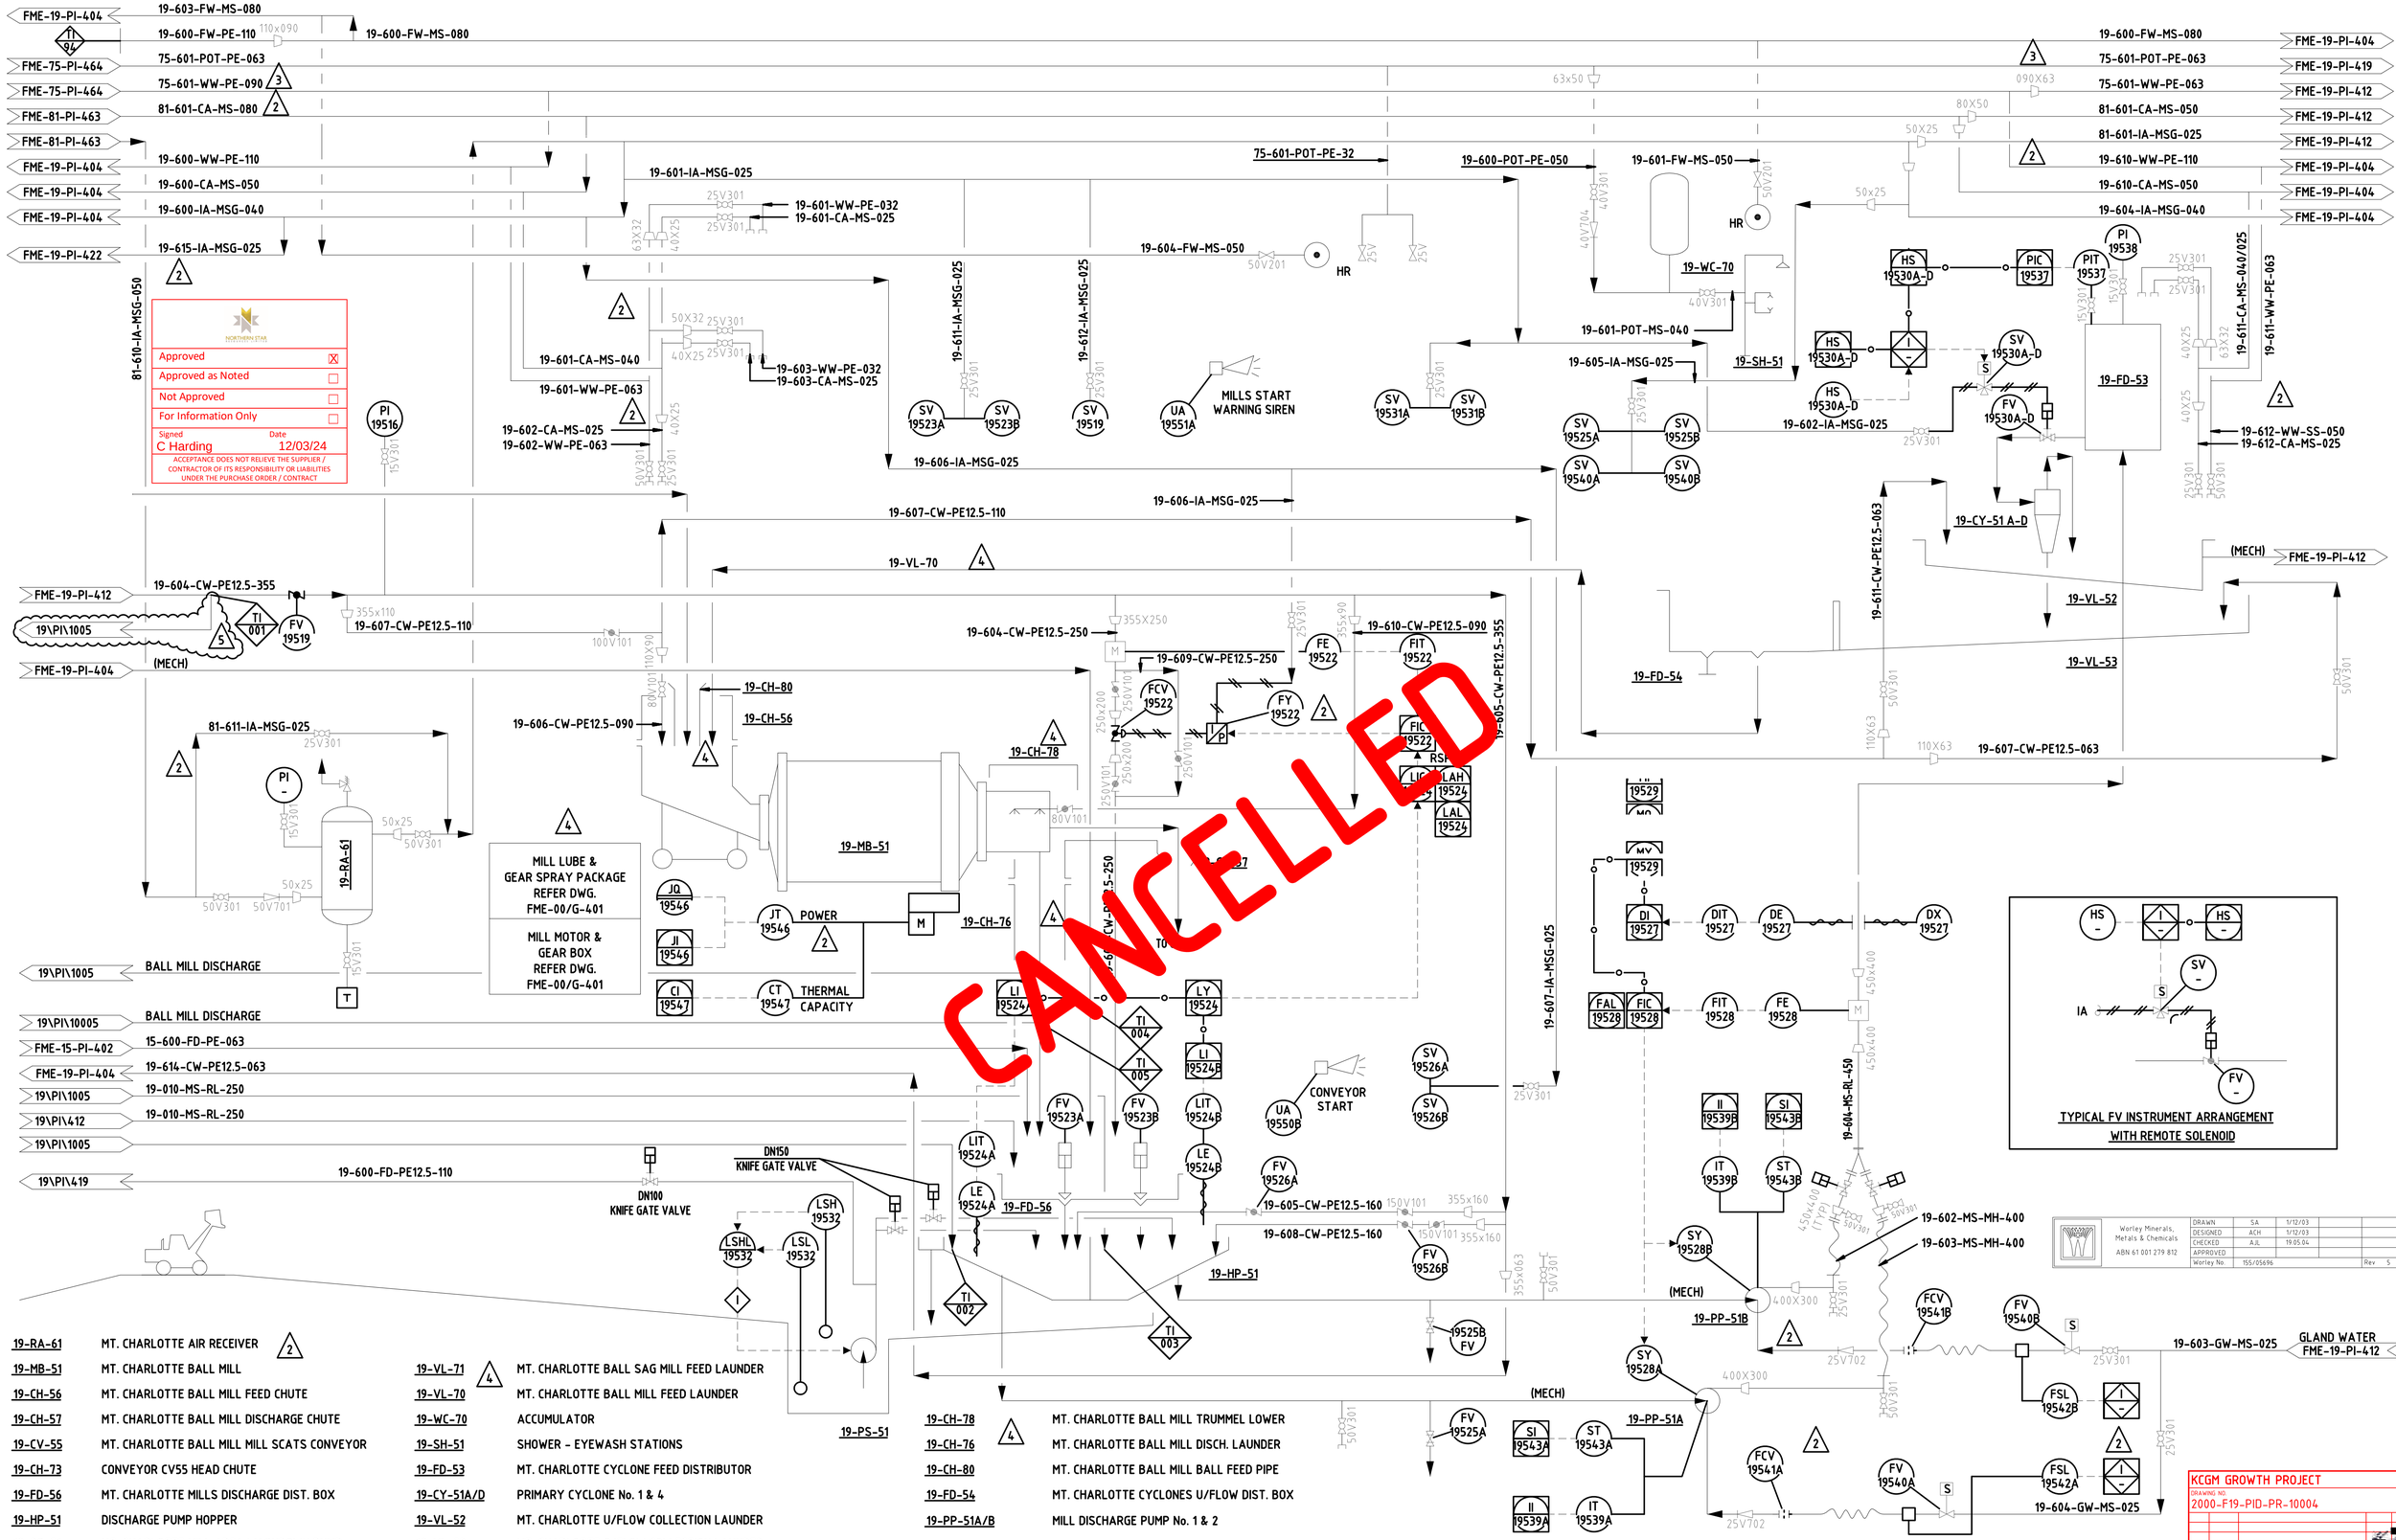


19-RA-61	MT. CHARLOTTE AIR RECEIVER	19-VL-71	MT. CHARLOTTE BALL SAG MILL FEED LAUNDER
19-MB-51	MT. CHARLOTTE BALL MILL	19-VL-70	MT. CHARLOTTE BALL MILL FEED LAUNDER
19-CH-56	MT. CHARLOTTE BALL MILL FEED CHUTE	19-WC-70	ACCUMULATOR
19-CH-57	MT. CHARLOTTE BALL MILL DISCHARGE CHUTE	19-SH-51	SHOWER - EYEWASH STATIONS
19-CV-55	MT. CHARLOTTE BALL MILL MILL SCATS CONVEYOR	19-FD-53	MT. CHARLOTTE CYCLONE FEED DISTRIBUTOR
19-CH-73	CONVEYOR CV55 HEAD CHUTE	19-CY-51A/D	PRIMARY CYCLONE No. 1 & 4
19-FD-56	MT. CHARLOTTE MILLS DISCHARGE DIST. BOX	19-VL-52	MT. CHARLOTTE U/FLOW COLLECTION LAUNDER
19-HP-51	DISCHARGE PUMP HOPPER	19-VL-53	MT. CHARLOTTE O/FLOW COLLECTION LAUNDER
19-PS-51	MT. CHARLOTTE MILL AREA WASHDOWN PUMP	19-CH-78	MT. CHARLOTTE BALL MILL TRUMMEL LOWER
		19-CH-76	MT. CHARLOTTE BALL MILL DISCH. LAUNDER
		19-CH-80	MT. CHARLOTTE BALL MILL BALL FEED PIPE
		19-FD-54	MT. CHARLOTTE CYCLONES U/FLOW DIST. BOX
		19-PP-51A/B	MILL DISCHARGE PUMP No. 1 & 2

FME-00-SP-408	INSTRUMENTS STANDARDS
FME-00-SP-404	STANDARD ABBREV. & VALVE SYMBOLS
FME-00-SP-403	STANDARD EQUIPMENT SYMBOLS
DRAWING No.	REFERENCE DRAWINGS

COPYRIGHT ©
This drawing remains the property of MINPROC ENGINEERS LIMITED and may not be copied in any way without prior written approval from this company.

MINPROC ENGINEERS LIMITED
A.C.N. 008 992 694
22, STIRLING HIGHWAY, NEDLANDS WA 6009
PHONE (09) 347 4777

No.	BY	DATE	REVISION	CHECKED
6	TR	31/12/19	UPDATED	P.A.Z.
5	LB	12/05/04	APP FOR CONSTRUCTION	AJL ACH
4		2/5/95	REVISED AS NOTED	
3		14/4/95	REVISED AS NOTED	
2		31/3/95	REVISED AS NOTED	
1		27/1/95	APPROVED FOR CONSTRUCTION F037	
0		21/12/94	APPROVED FOR TENDER	

	BY	DATE
PROJECT APPR.		9/3/95
DESIGN APPR.		3/5/95
DESIGNED		20/2/95
CHECKED	G.TORKINGTON	28/2/95
DRAWN		28.07.94

PLANT GRID NORTH

CLIENT: KALGOORLIE CONSOLIDATED GOLD MINES

TITLE: FIMISTON EXPANSION 1994/95
PIPING & INSTRUMENTATION DIAGRAM
BALL MILLING MT. CHARLOTTE

SIZE B1 | SCALE N.T.S

REV. No. 0 1 2 3 4 5 6

DRAWING No. FME-19-PI-408

Worley Minerals, Metals & Chemicals ABN 61 001 279 812	DRAWN	SA	1/12/03		
	DESIGNED	ACH	1/12/03		
	CHECKED	AJL	19.05.04		
	APPROVED				
	Worley No.	155/05696		Rev	5

KCGM GROWTH PROJECT
DRAWING NO. 2000-F19-PID-PR-10004

REV	DATE	DESCRIPTION
B	01MAR24	CANCELLED
A	08MAY23	ISSUED FOR INFORMATION