


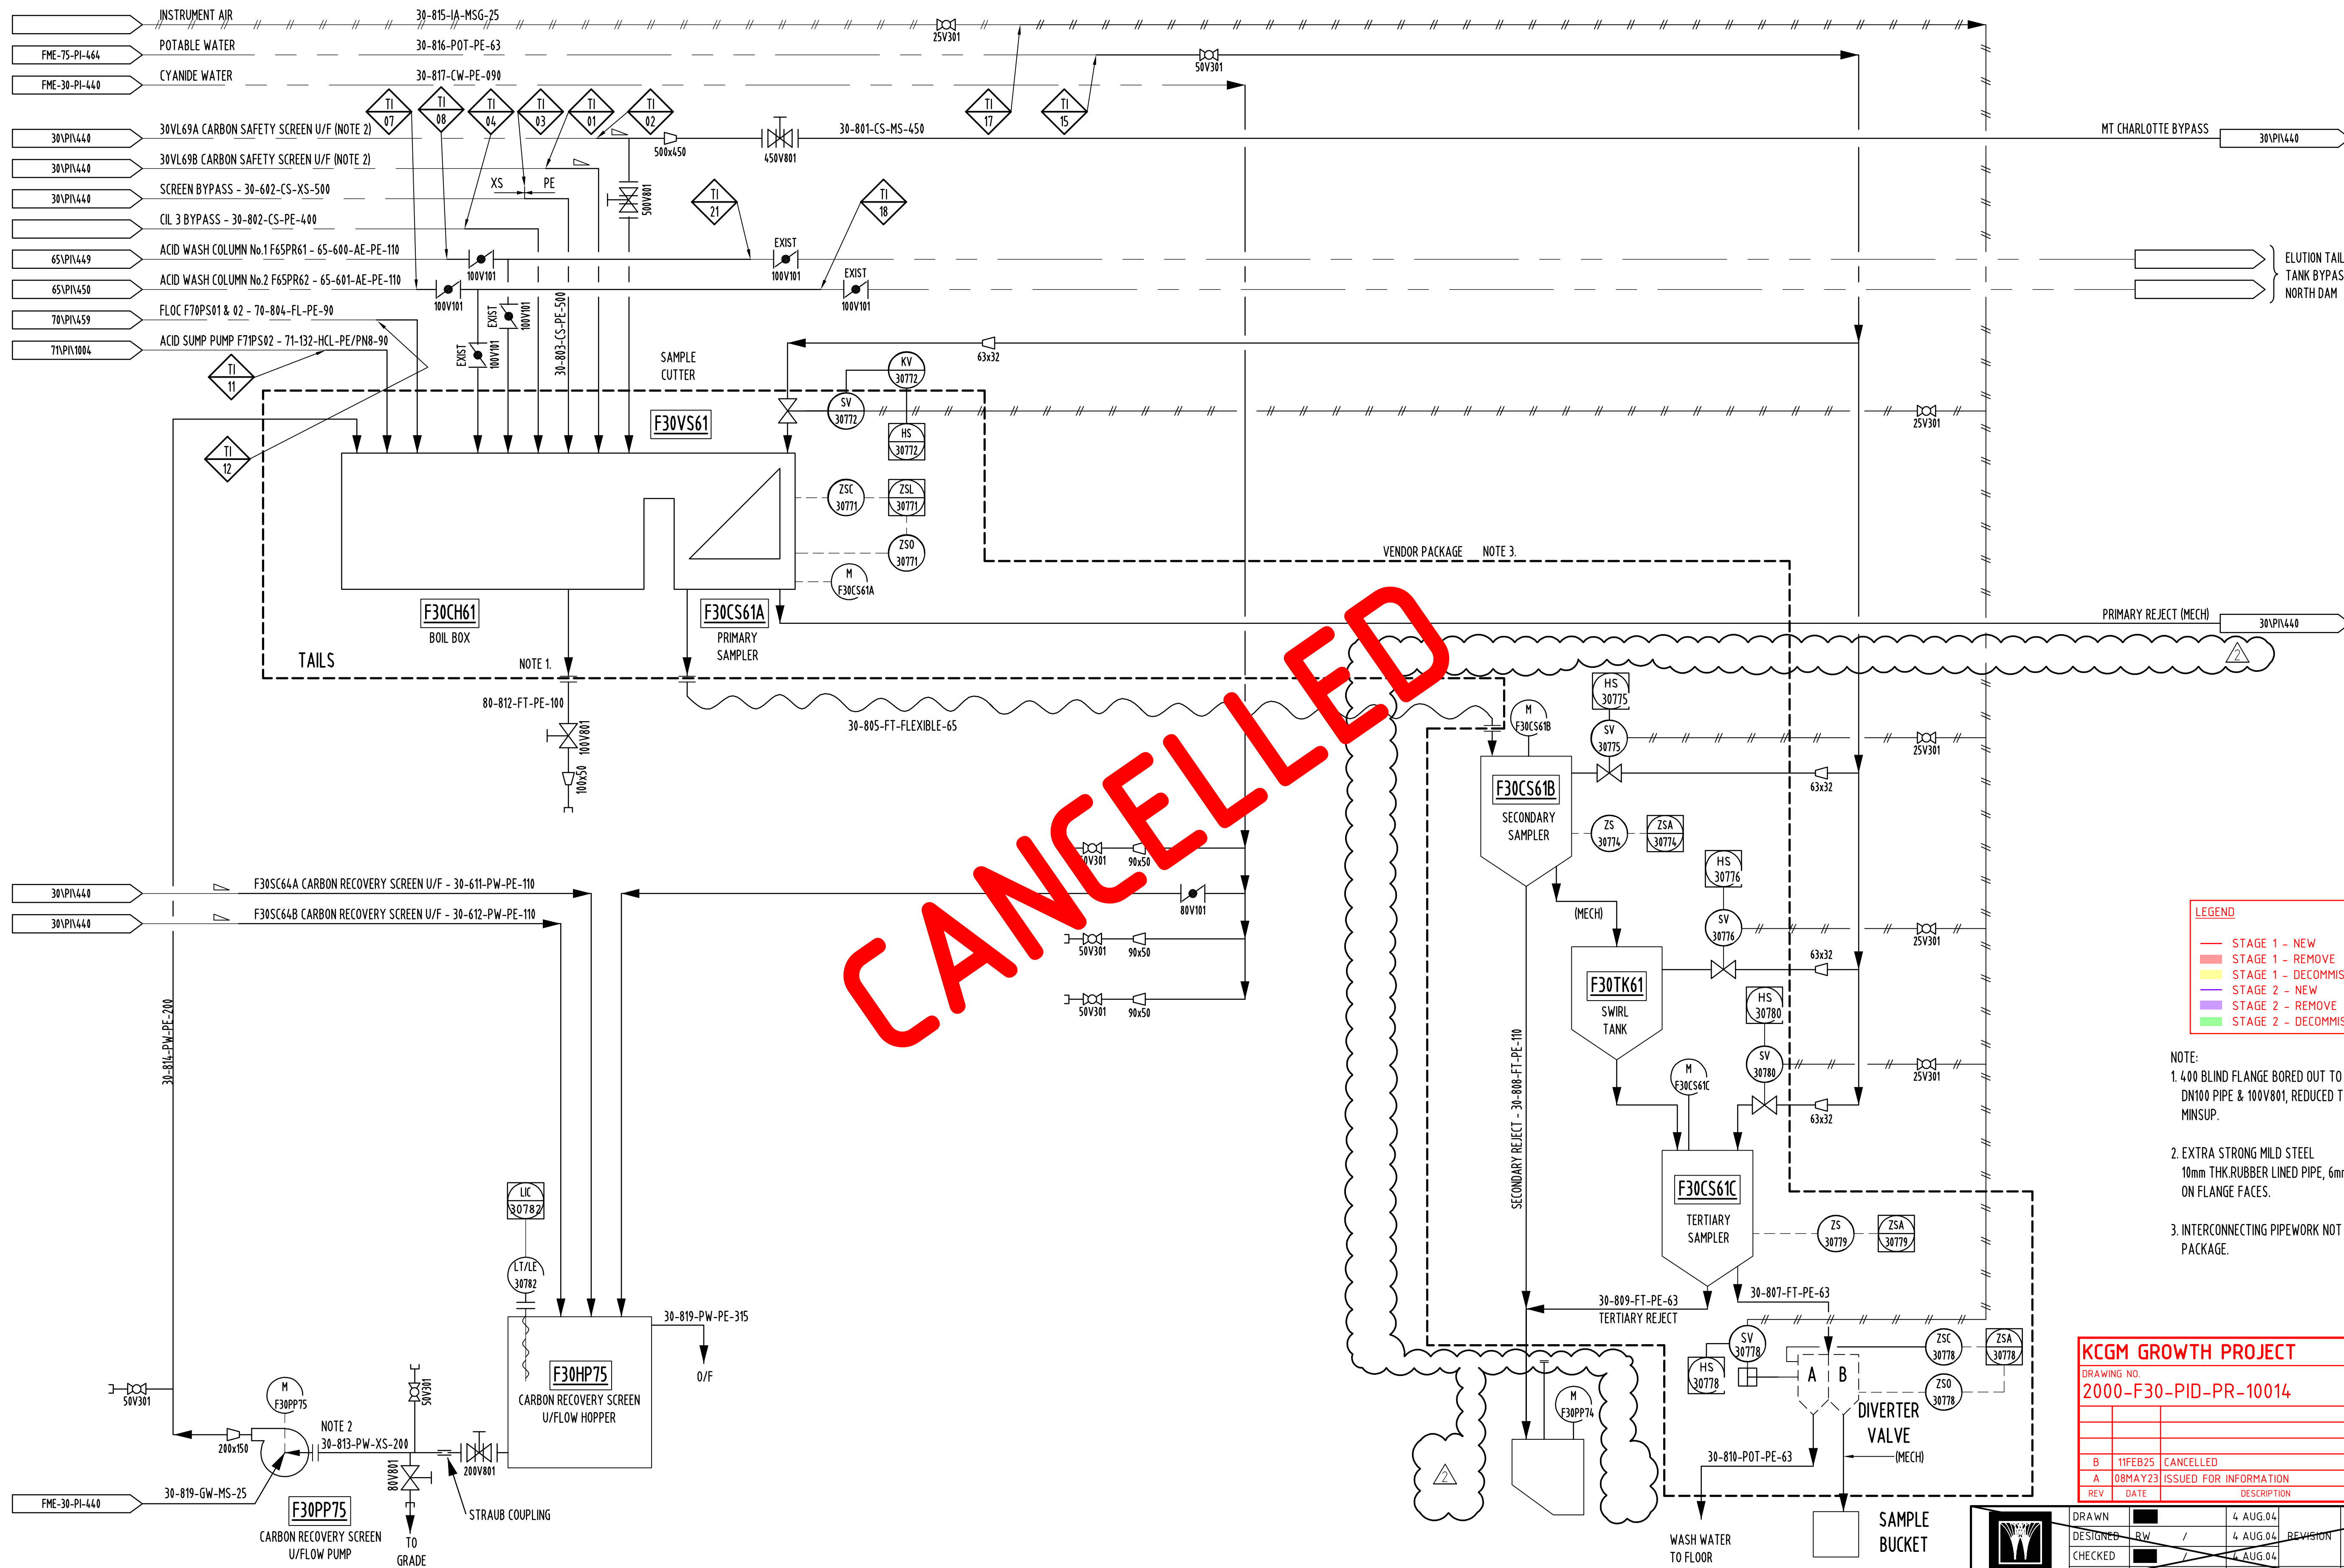

- LEGEND
- STAGE 1 - NEW
 - STAGE 1 - REMOVE
 - STAGE 1 - DECOMMISSIONED (OTHERS)
 - STAGE 2 - NEW
 - STAGE 2 - REMOVE
 - STAGE 2 - DECOMMISSIONED (OTHERS)

- NOTE:
- 400 BLIND FLANGE BORED OUT TO SUIT
DN100 PIPE & 100V801, REDUCED TO 50mm
MINSUP.
 - EXTRA STRONG MILD STEEL
10mm THK. RUBBER LINED PIPE, 6mm THK.
ON FLANGE FACES.
 - INTERCONNECTING PIPEWORK NOT PART OF VEDOR
PACKAGE.

KCGM GROWTH PROJECT				
DRAWING NO. 2000-F30-PID-PR-10014				
REV	DATE	DESCRIPTION	CHECK	TECH APP
B	11FEB25	CANCELLED		
A	08MAY23	ISSUED FOR INFORMATION		

DRAWN	DESIGNED	CHECKED	PRINT ENG	APPROVED	DATE	REVISION	Worley No.	30\PI\1000

SCALE	NTS	SIZE	DRAWING NUMBER	REV
DRAWN	13.01.04	A1	30\PI\1000	2
DESIGNED	18.08.03			
CHECKED	21.07.04			
APPROVED	21.07.04			
PROJ APP				
PROJ FILE #				