


1. REFER TO 2000-F75-PID-PR-25008 FOR FINAL TAILS SLURRY LINES RE-ROUTING.

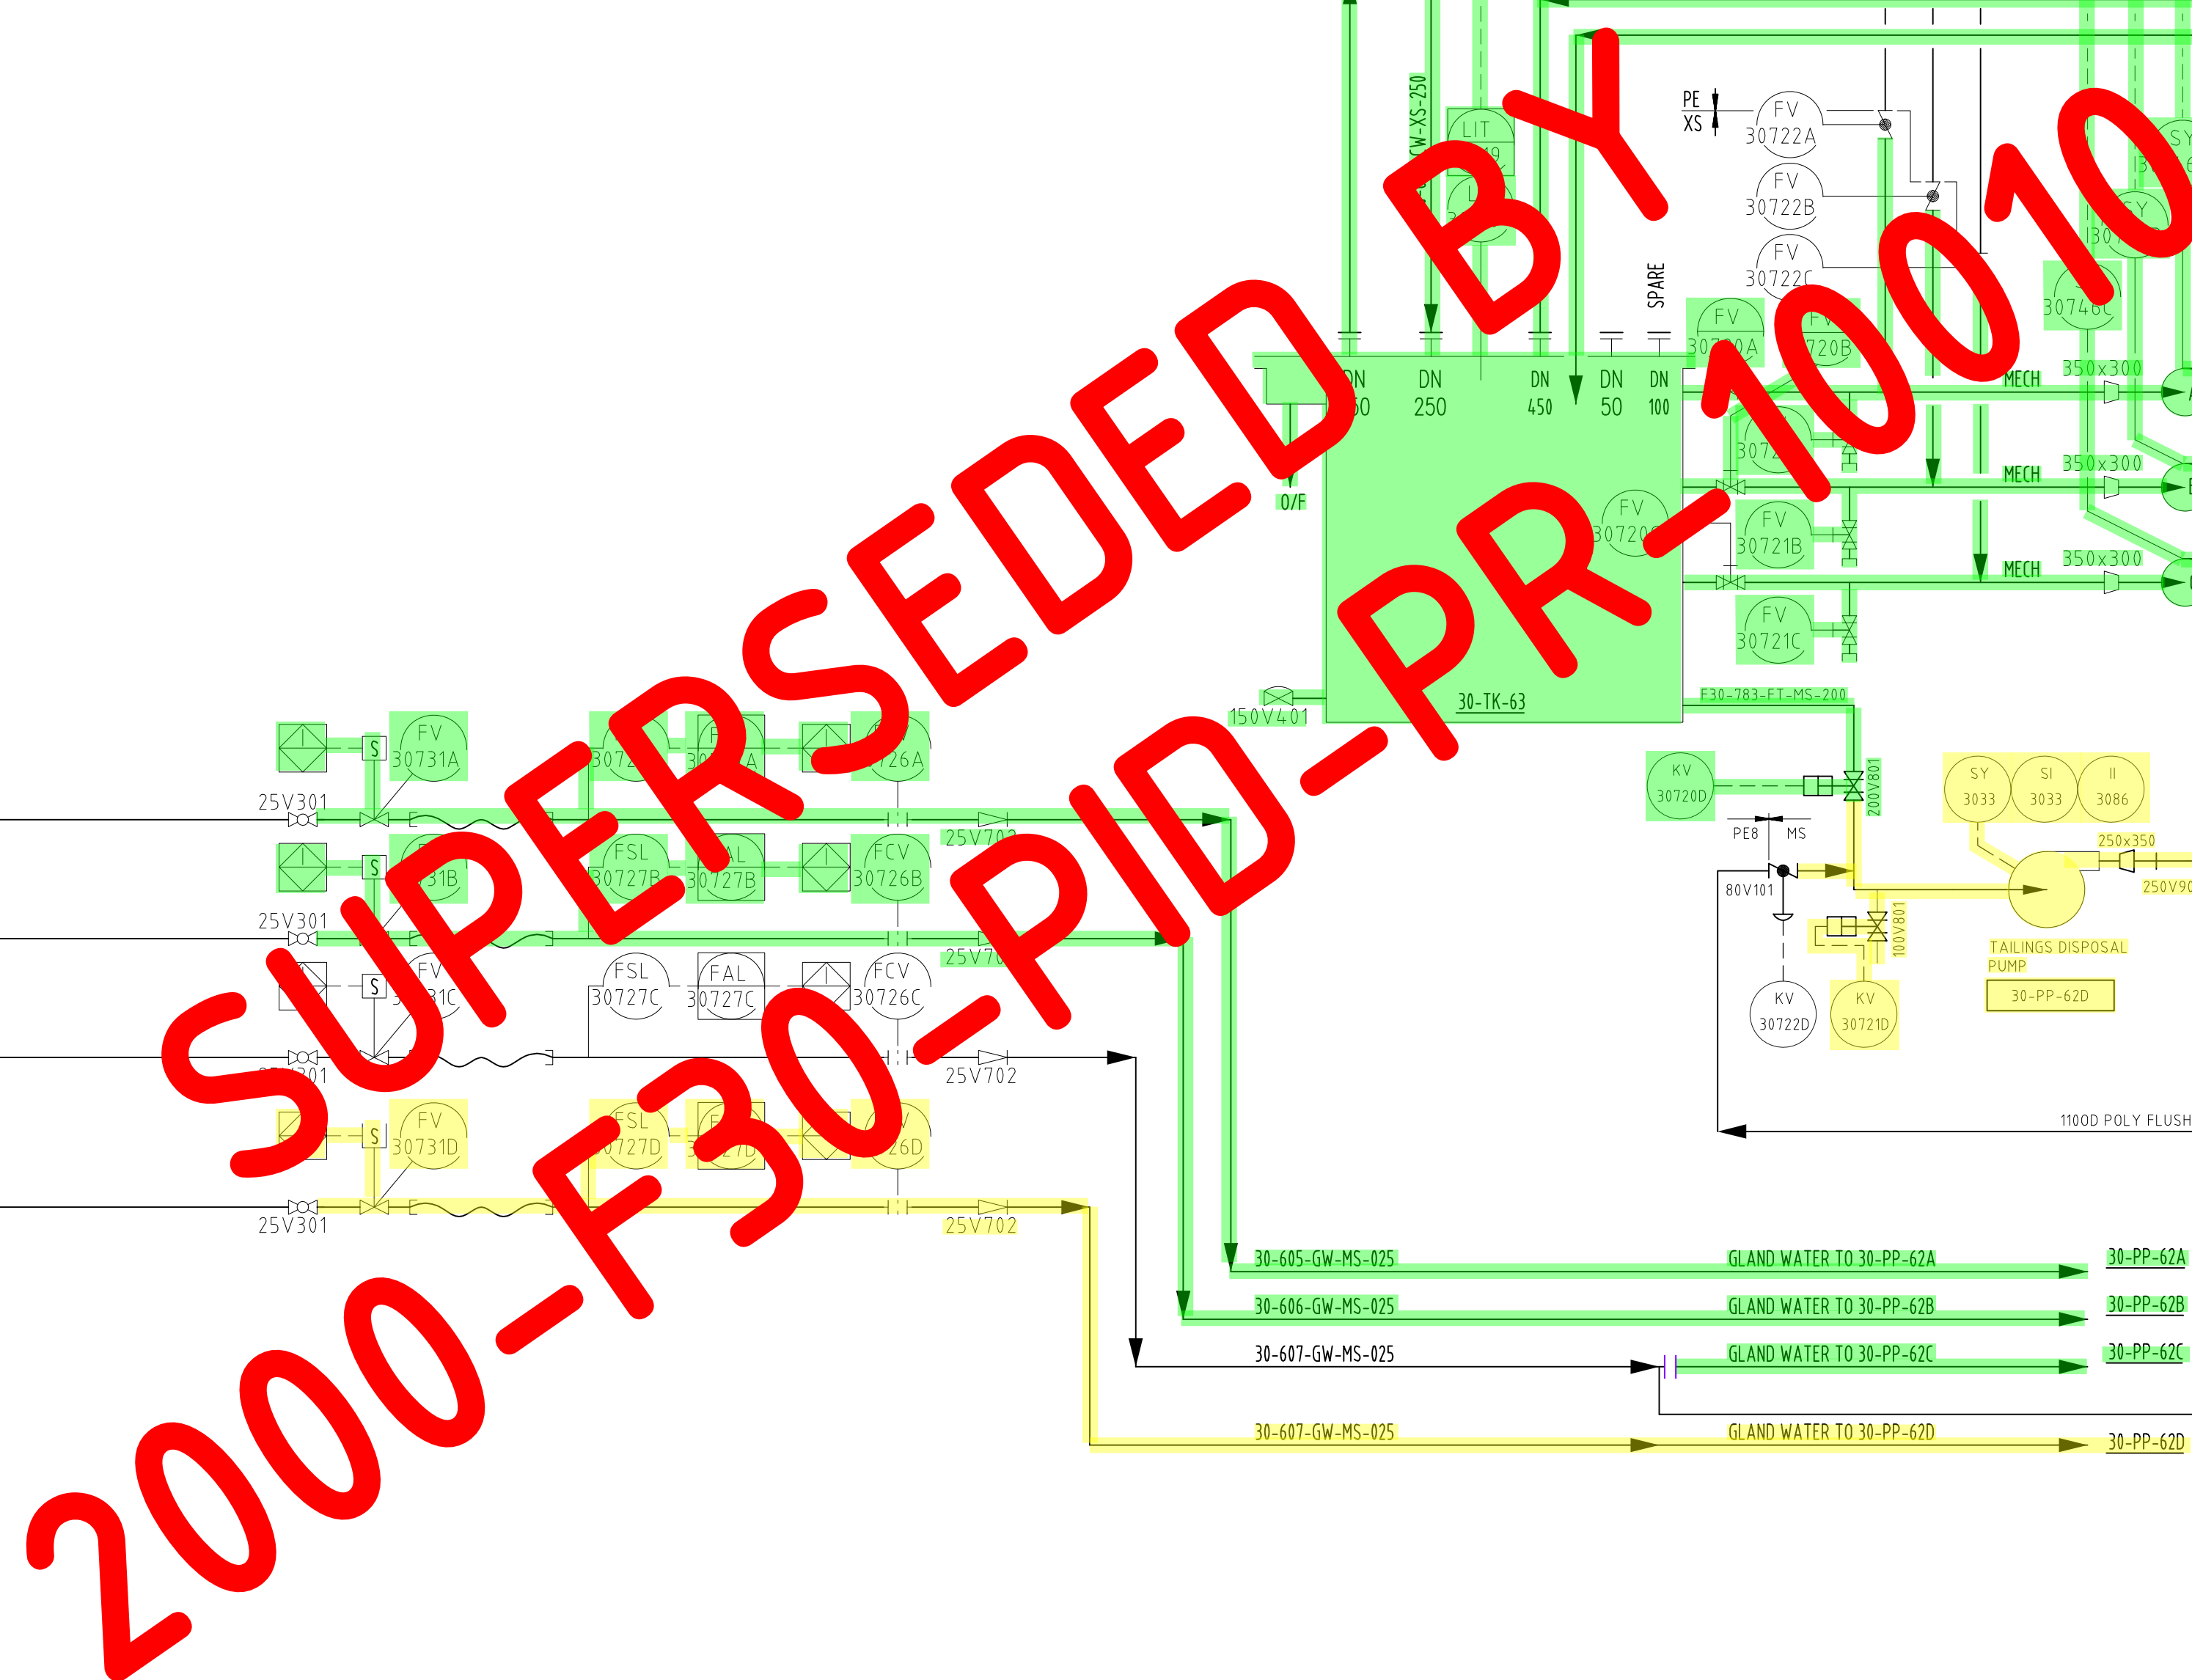

KCGM GROWTH PROJECT				
DRAWING NO.				
2000-F30-PID-PR-10015				
E	11FEB25	SUPERSEDED		
D	30MAY24	ISSUED FOR HAZOP		
C	26APR24	ISSUED FOR DESIGN		
B	01MAR24	ISSUED FOR CLIENT REVIEW		
REV	DATE	DESCRIPTION	CHECK	TECH APP

[illegible]