


D:\CAD PROJECTS\235 NORTHERN STAR RESOURCES LTD\23517 KCGM GROWTH PROJECT\03 DELIVERABLES\PR\PID\ISSUED\12.09.25 - SIGNING\NATIVES\2000-F30-PID-PR-10013_1.DWG 09SEP25 8:27AM ANNE.HOYNE

NOTES:

1. THIS DRAWING ONLY SHOWS THE OXYGEN INJECTION TIE-INS FOR CIL2. THIS SHOULD BE READ IN CONJUNCTION WITH 2000-F30-PID-PR-10005

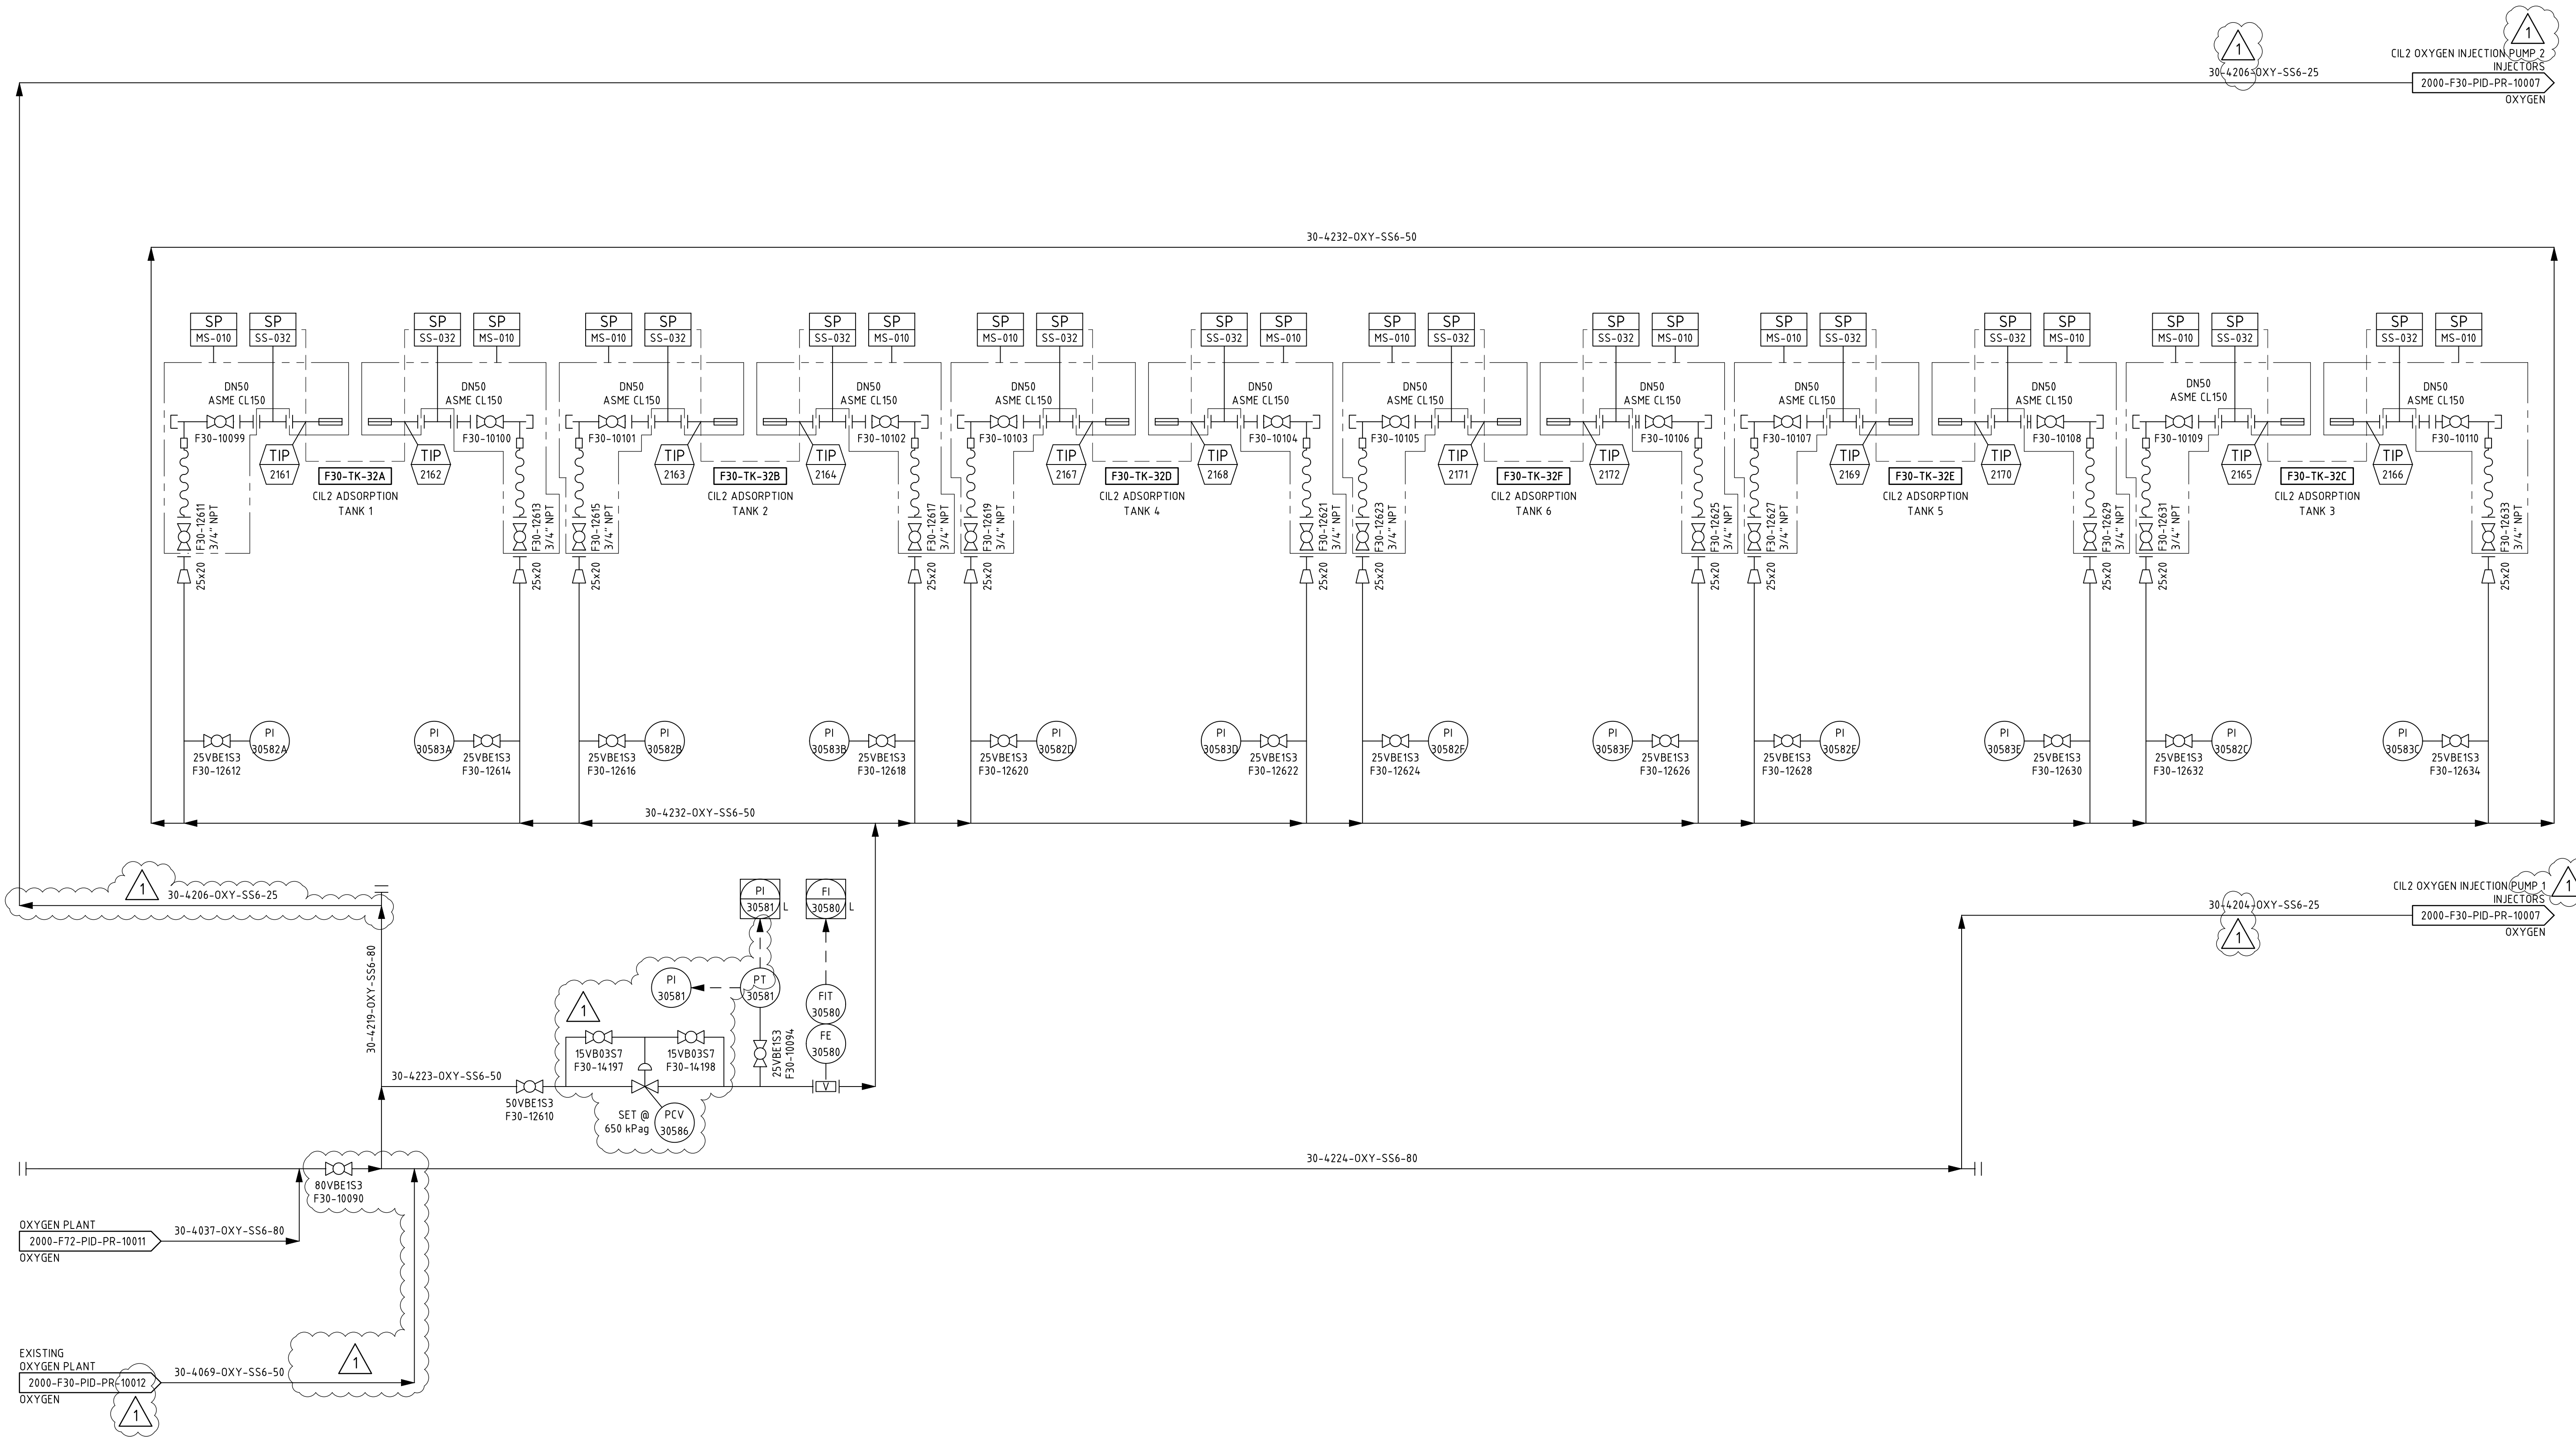

DRG No.	REFERENCES	REV	DATE	DESCRIPTION	DRAW	CHECK	DESIGN	TECH APP	PROJ APP
2000-F00-PID-PR-10007	LEGEND SHEET 7 - PIPING AND INSTRUMENTATION DIAGRAM								
2000-F00-PID-PR-10006	LEGEND SHEET 6 - PIPING AND INSTRUMENTATION DIAGRAM								
2000-F00-PID-PR-10005	LEGEND SHEET 5 - PIPING AND INSTRUMENTATION DIAGRAM								
2000-F00-PID-PR-10004	LEGEND SHEET 4 - PIPING AND INSTRUMENTATION DIAGRAM								
2000-F00-PID-PR-10003	LEGEND SHEET 3 - PIPING AND INSTRUMENTATION DIAGRAM								
2000-F00-PID-PR-10002	LEGEND SHEET 2 - PIPING AND INSTRUMENTATION DIAGRAM								
2000-F00-PID-PR-10001	LEGEND SHEET 1 - PIPING AND INSTRUMENTATION DIAGRAM								
1	12SEP25	GENERAL REVISIONS AS NOTED			AH	LV	JBe	LV	DM
0	20JUN25	APPROVED FOR CONSTRUCTION			AH	LV	JBe	LV	DM



PRIMERO PROJECT NUMBER: 23517

INFORMATION AND REPRESENTATIONS ON THIS DRAWING ARE THE INTELLECTUAL PROPERTY OF PRIMERO UNLESS SPECIFICALLY IDENTIFIED OTHERWISE. ALL RIGHTS INCLUDING USE RESERVED

PROJECT:	NORTHERN STAR RESOURCES LTD KCGM GROWTH PROJECT		
TITLE:	CIL2 CIL2 OXYGEN INJECTION LANCE PIPING AND INSTRUMENTATION DIAGRAM		
SHEET	SCALE	DRG No.	REVISION
A1	NTS	2000-F30-PID-PR-10013	1