


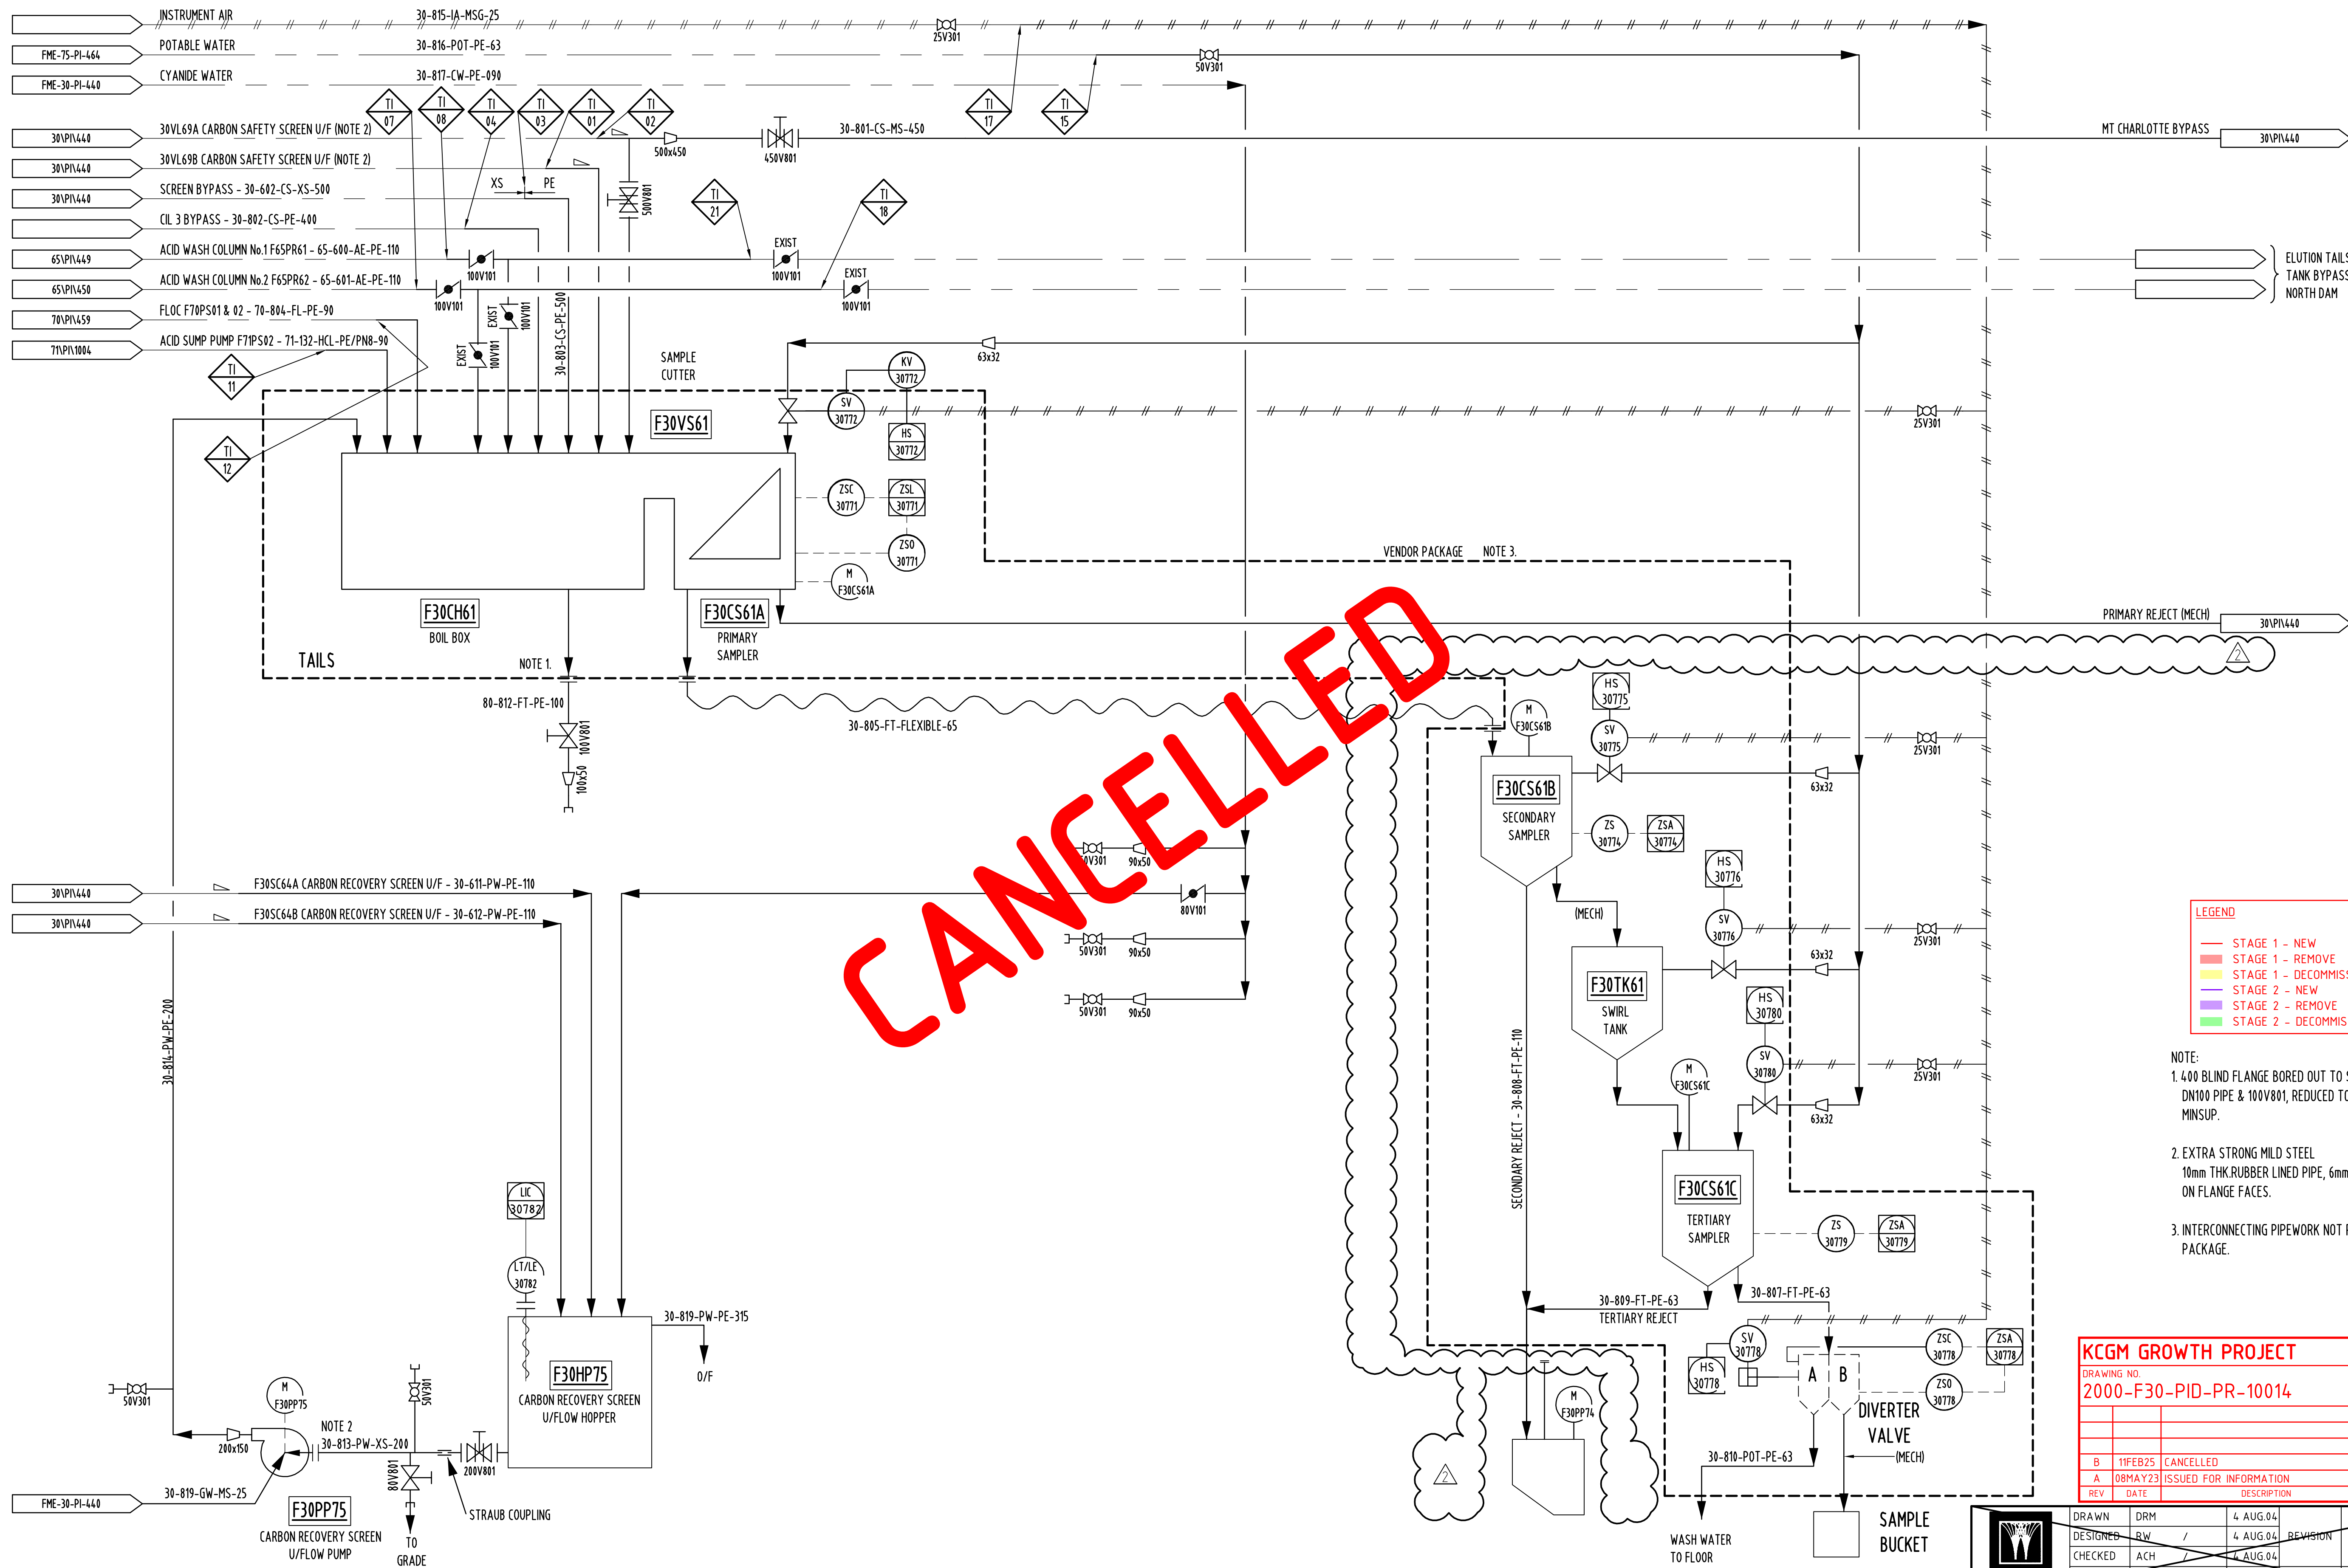

LEGEND					
—	STAGE 1 - NEW				
—	STAGE 1 - REMOVE				
—	STAGE 1 - DECOMMISSIONED (OTHERS)				
—	STAGE 2 - NEW				
—	STAGE 2 - REMOVE				
—	STAGE 2 - DECOMMISSIONED (OTHERS)				

- NOTE:
- 400 BLIND FLANGE BORED OUT TO SUIT DN100 PIPE & 100V801, REDUCED TO 50mm MINSUP.
 - EXTRA STRONG MILD STEEL 10mm THK. RUBBER LINED PIPE, 6mm THK. ON FLANGE FACES.
 - INTERCONNECTING PIPEWORK NOT PART OF VENDOR PACKAGE.

KCGM GROWTH PROJECT
DRAWING NO.
2000-F30-PID-PR-10014

REV	DATE	DESCRIPTION	CHECK	TECH APP
B	11FEB25	CANCELLED	LV	DM
A	08MAY23	ISSUED FOR INFORMATION	LV	LV

DRAWN	DRM	DATE	REVISION	1
DESIGNED	RW	4 AUG 04		
CHECKED	ACH	4 AUG 04		
PRINC. ENG.	ACH	4 AUG 04		
APPROVED	RW	4 AUG 04		



SCALE	NTS	SIZE	DRAWING NUMBER	REV
DRAWN	RW	13.01.04		
DESIGNED	ACH	18.08.03		
CHECKED	ACH	21.07.04		
APPROVED	RW	21.07.04		

FIMISTON PLANT
LEACH, ADSORPTION & THICKENING
TAILINGS SAMPLING CIRCUIT
P&ID

KALGOORLIE CONSOLIDATED GOLD MINES PTY. LTD.

ABN 009 377 619 003