
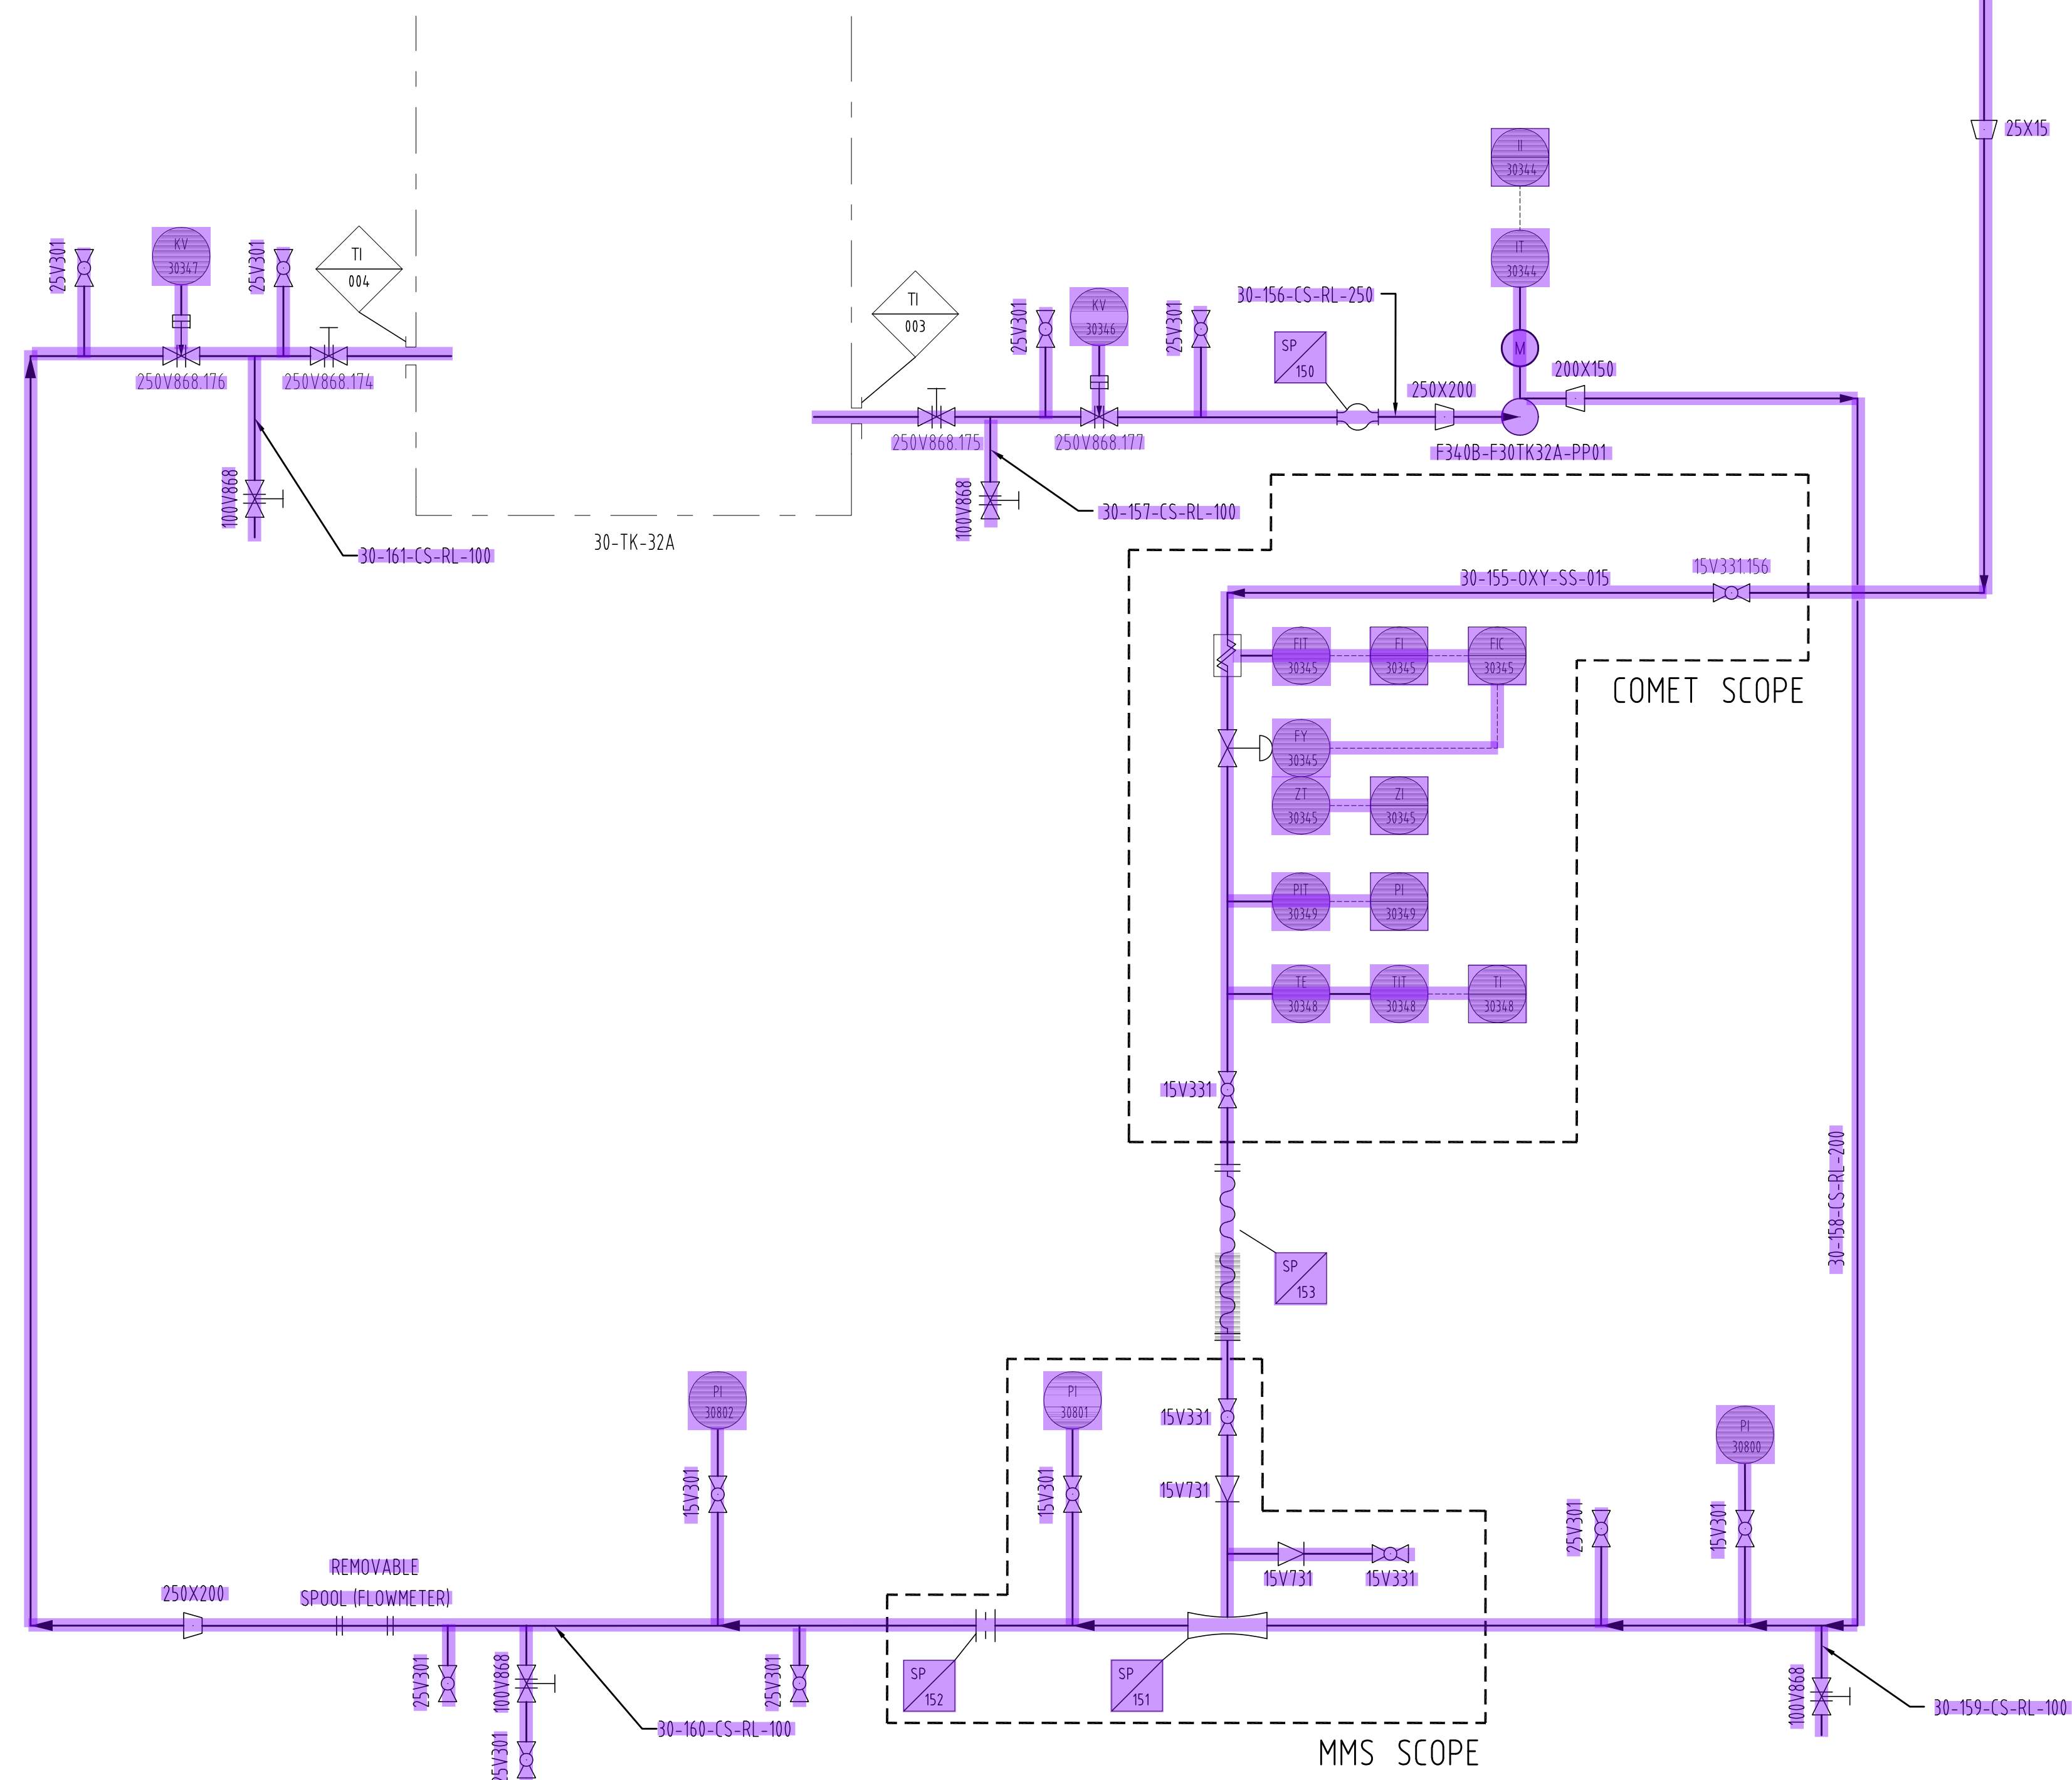


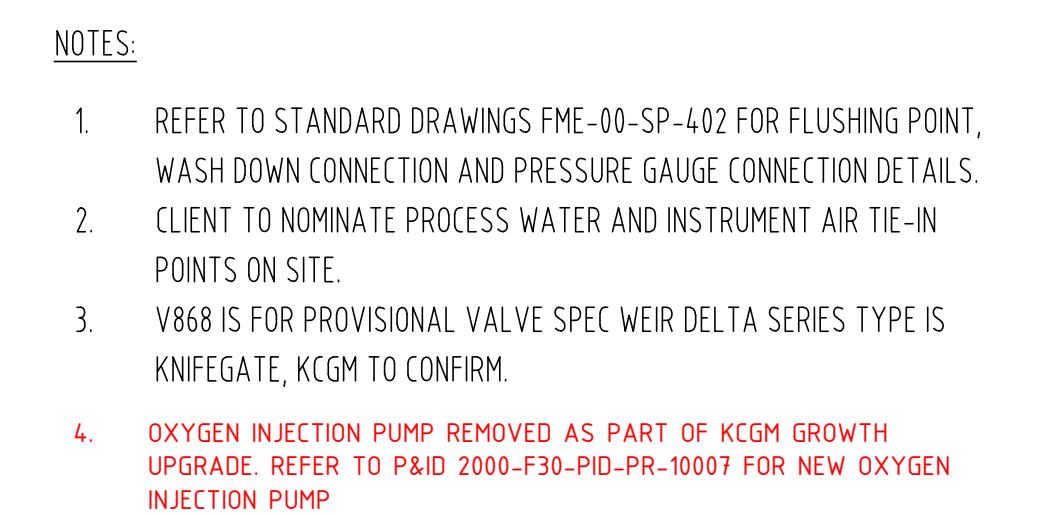

30-TK32A
FIMISTON TK32A

LEGEND

- EXISTING
- NON-EXISTENT
- STAGE 1 - NEW
- STAGE 1 - REMOVE
- STAGE 1 - DECOMMISSIONED (OTHERS)
- STAGE 2 - NEW
- STAGE 2 - REMOVE
- STAGE 2 - DECOMMISSIONED (OTHERS)

KCGM GROWTH PROJECT					
DRAWING NO.					
2000-F30-PID-PR-10022					
0	22SEP25	APPROVED FOR CONSTRUCTION		LV	DM
REV	DATE	DESCRIPTION		CHECK	TECH APP

[illegible]