
NOTES:

1. REFER TO 2000-F24-PID-PR-10034 FOR GLAND WATER DETAIL.
2. F35-PP-448 TO BE RELOCATED IN STAGE 2. REFER TO P&ID 2000-F35-PID-PR-10006.
3. FE 35434, DE 35435 AND LINES 3032 & 3053 REPURPOSED FOR STAGE 2 FOR THE UFG CIRCUIT 1 FEED PUMP DISCHARGE. REFER TO P&ID 2000-F35-PID-PR-10006.

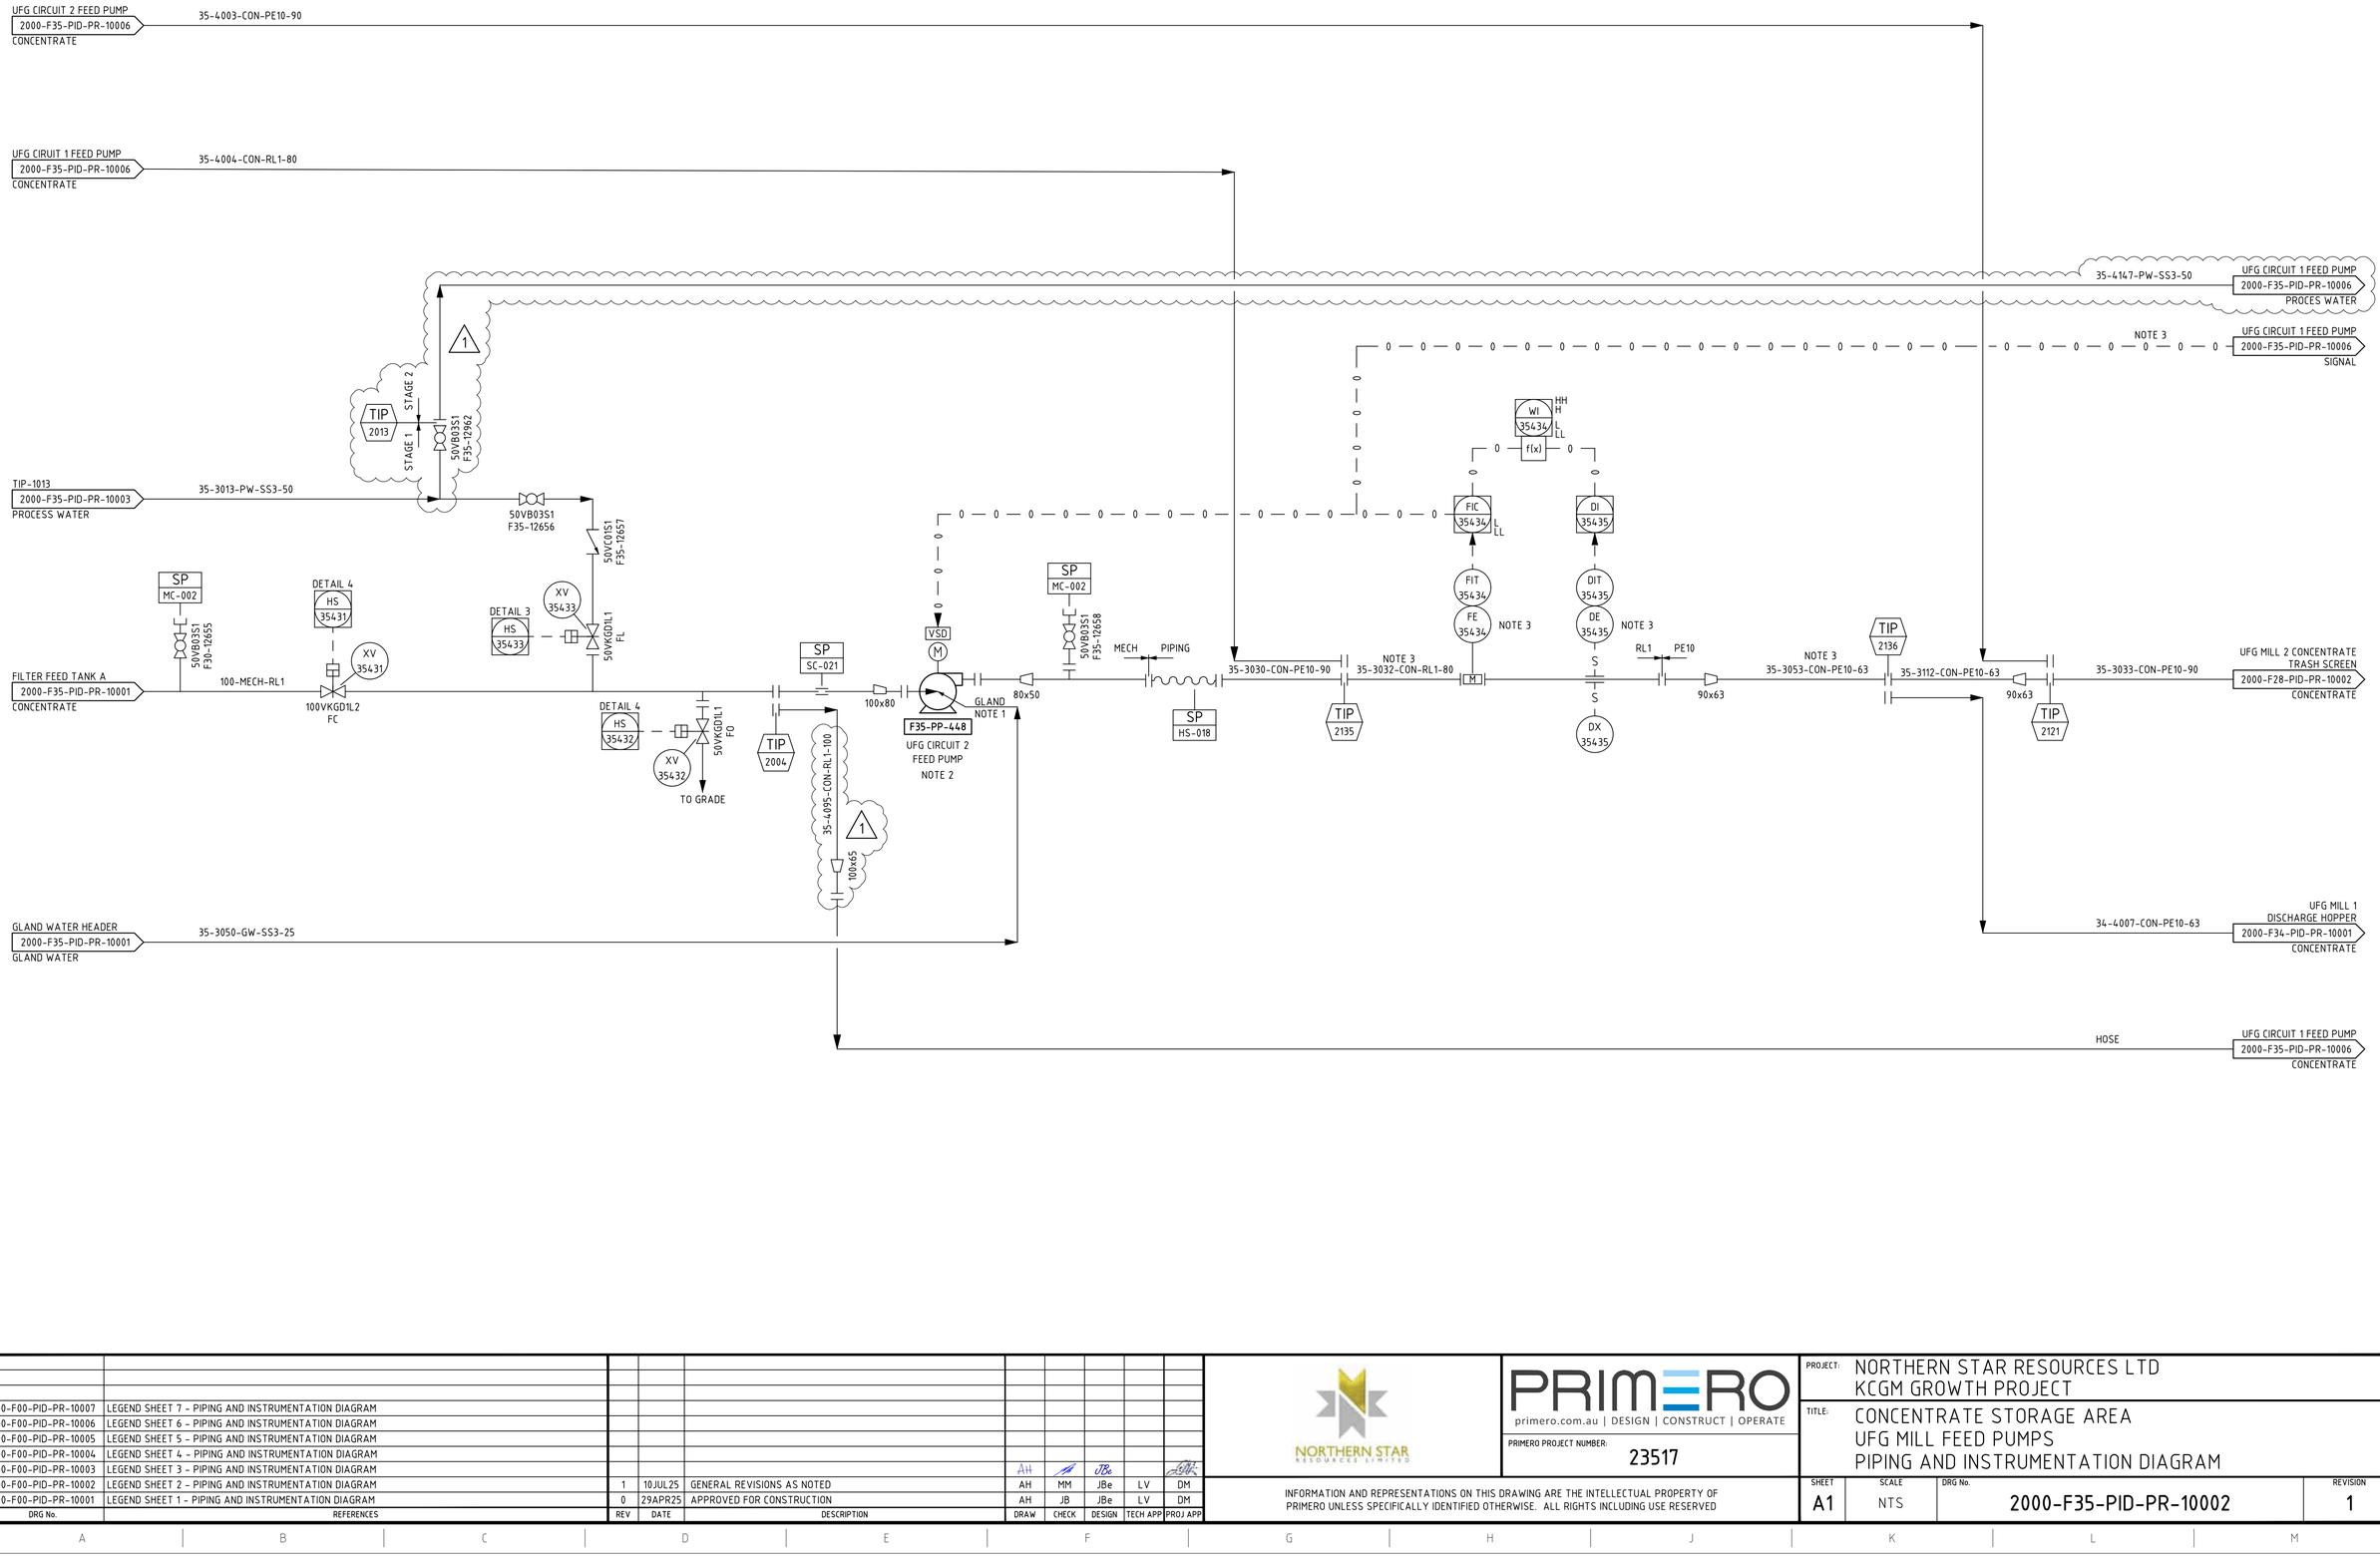

DRG No.	REFERENCES
2000-F00-PID-PR-10007	LEGEND SHEET 7 - PIPING AND INSTRUMENTATION DIAGRAM
2000-F00-PID-PR-10006	LEGEND SHEET 6 - PIPING AND INSTRUMENTATION DIAGRAM
2000-F00-PID-PR-10005	LEGEND SHEET 5 - PIPING AND INSTRUMENTATION DIAGRAM
2000-F00-PID-PR-10004	LEGEND SHEET 4 - PIPING AND INSTRUMENTATION DIAGRAM
2000-F00-PID-PR-10003	LEGEND SHEET 3 - PIPING AND INSTRUMENTATION DIAGRAM
2000-F00-PID-PR-10002	LEGEND SHEET 2 - PIPING AND INSTRUMENTATION DIAGRAM
2000-F00-PID-PR-10001	LEGEND SHEET 1 - PIPING AND INSTRUMENTATION DIAGRAM

REV	DATE	DESCRIPTION	DRAW	CHECK	DESIGN	TECH APP	PROJ APP
1	10JUL25	GENERAL REVISIONS AS NOTED	AH	MM	JBe	LV	DM
0	29APR25	APPROVED FOR CONSTRUCTION	AH	JB	JBe	LV	DM

NORTHERN STAR RESOURCES LIMITED

PRIMERO
primero.com.au | DESIGN | CONSTRUCT | OPERATE

PRIMERO PROJECT NUMBER: 23517

INFORMATION AND REPRESENTATIONS ON THIS DRAWING ARE THE INTELLECTUAL PROPERTY OF PRIMERO UNLESS SPECIFICALLY IDENTIFIED OTHERWISE. ALL RIGHTS INCLUDING USE RESERVED

PROJECT: NORTHERN STAR RESOURCES LTD
KCGM GROWTH PROJECT

TITLE: CONCENTRATE STORAGE AREA
UFG MILL FEED PUMPS
PIPING AND INSTRUMENTATION DIAGRAM

SHEET	SCALE	DRG No.	REVISION
A1	NTS	2000-F35-PID-PR-10002	1

D:\CAD PROJECTS\235 NORTHERN STAR RESOURCES LTD\23517 KCGM GROWTH PROJECT\03 DELIVERABLES\PRIPID\2000-F35-PID-PR-10002_1.DWG 10JUL25 12:42PM ANNE.HOYNE