


D:\CAD PROJECTS\235 NORTHERN STAR RESOURCES LTD\23517 KCGM GROWTH PROJECT\03 DELIVERABLES\PR\PID\NATIVES\2000-F21-PID-10002_1.DWG 09SEP25 8:00AM ANNE HOYNE

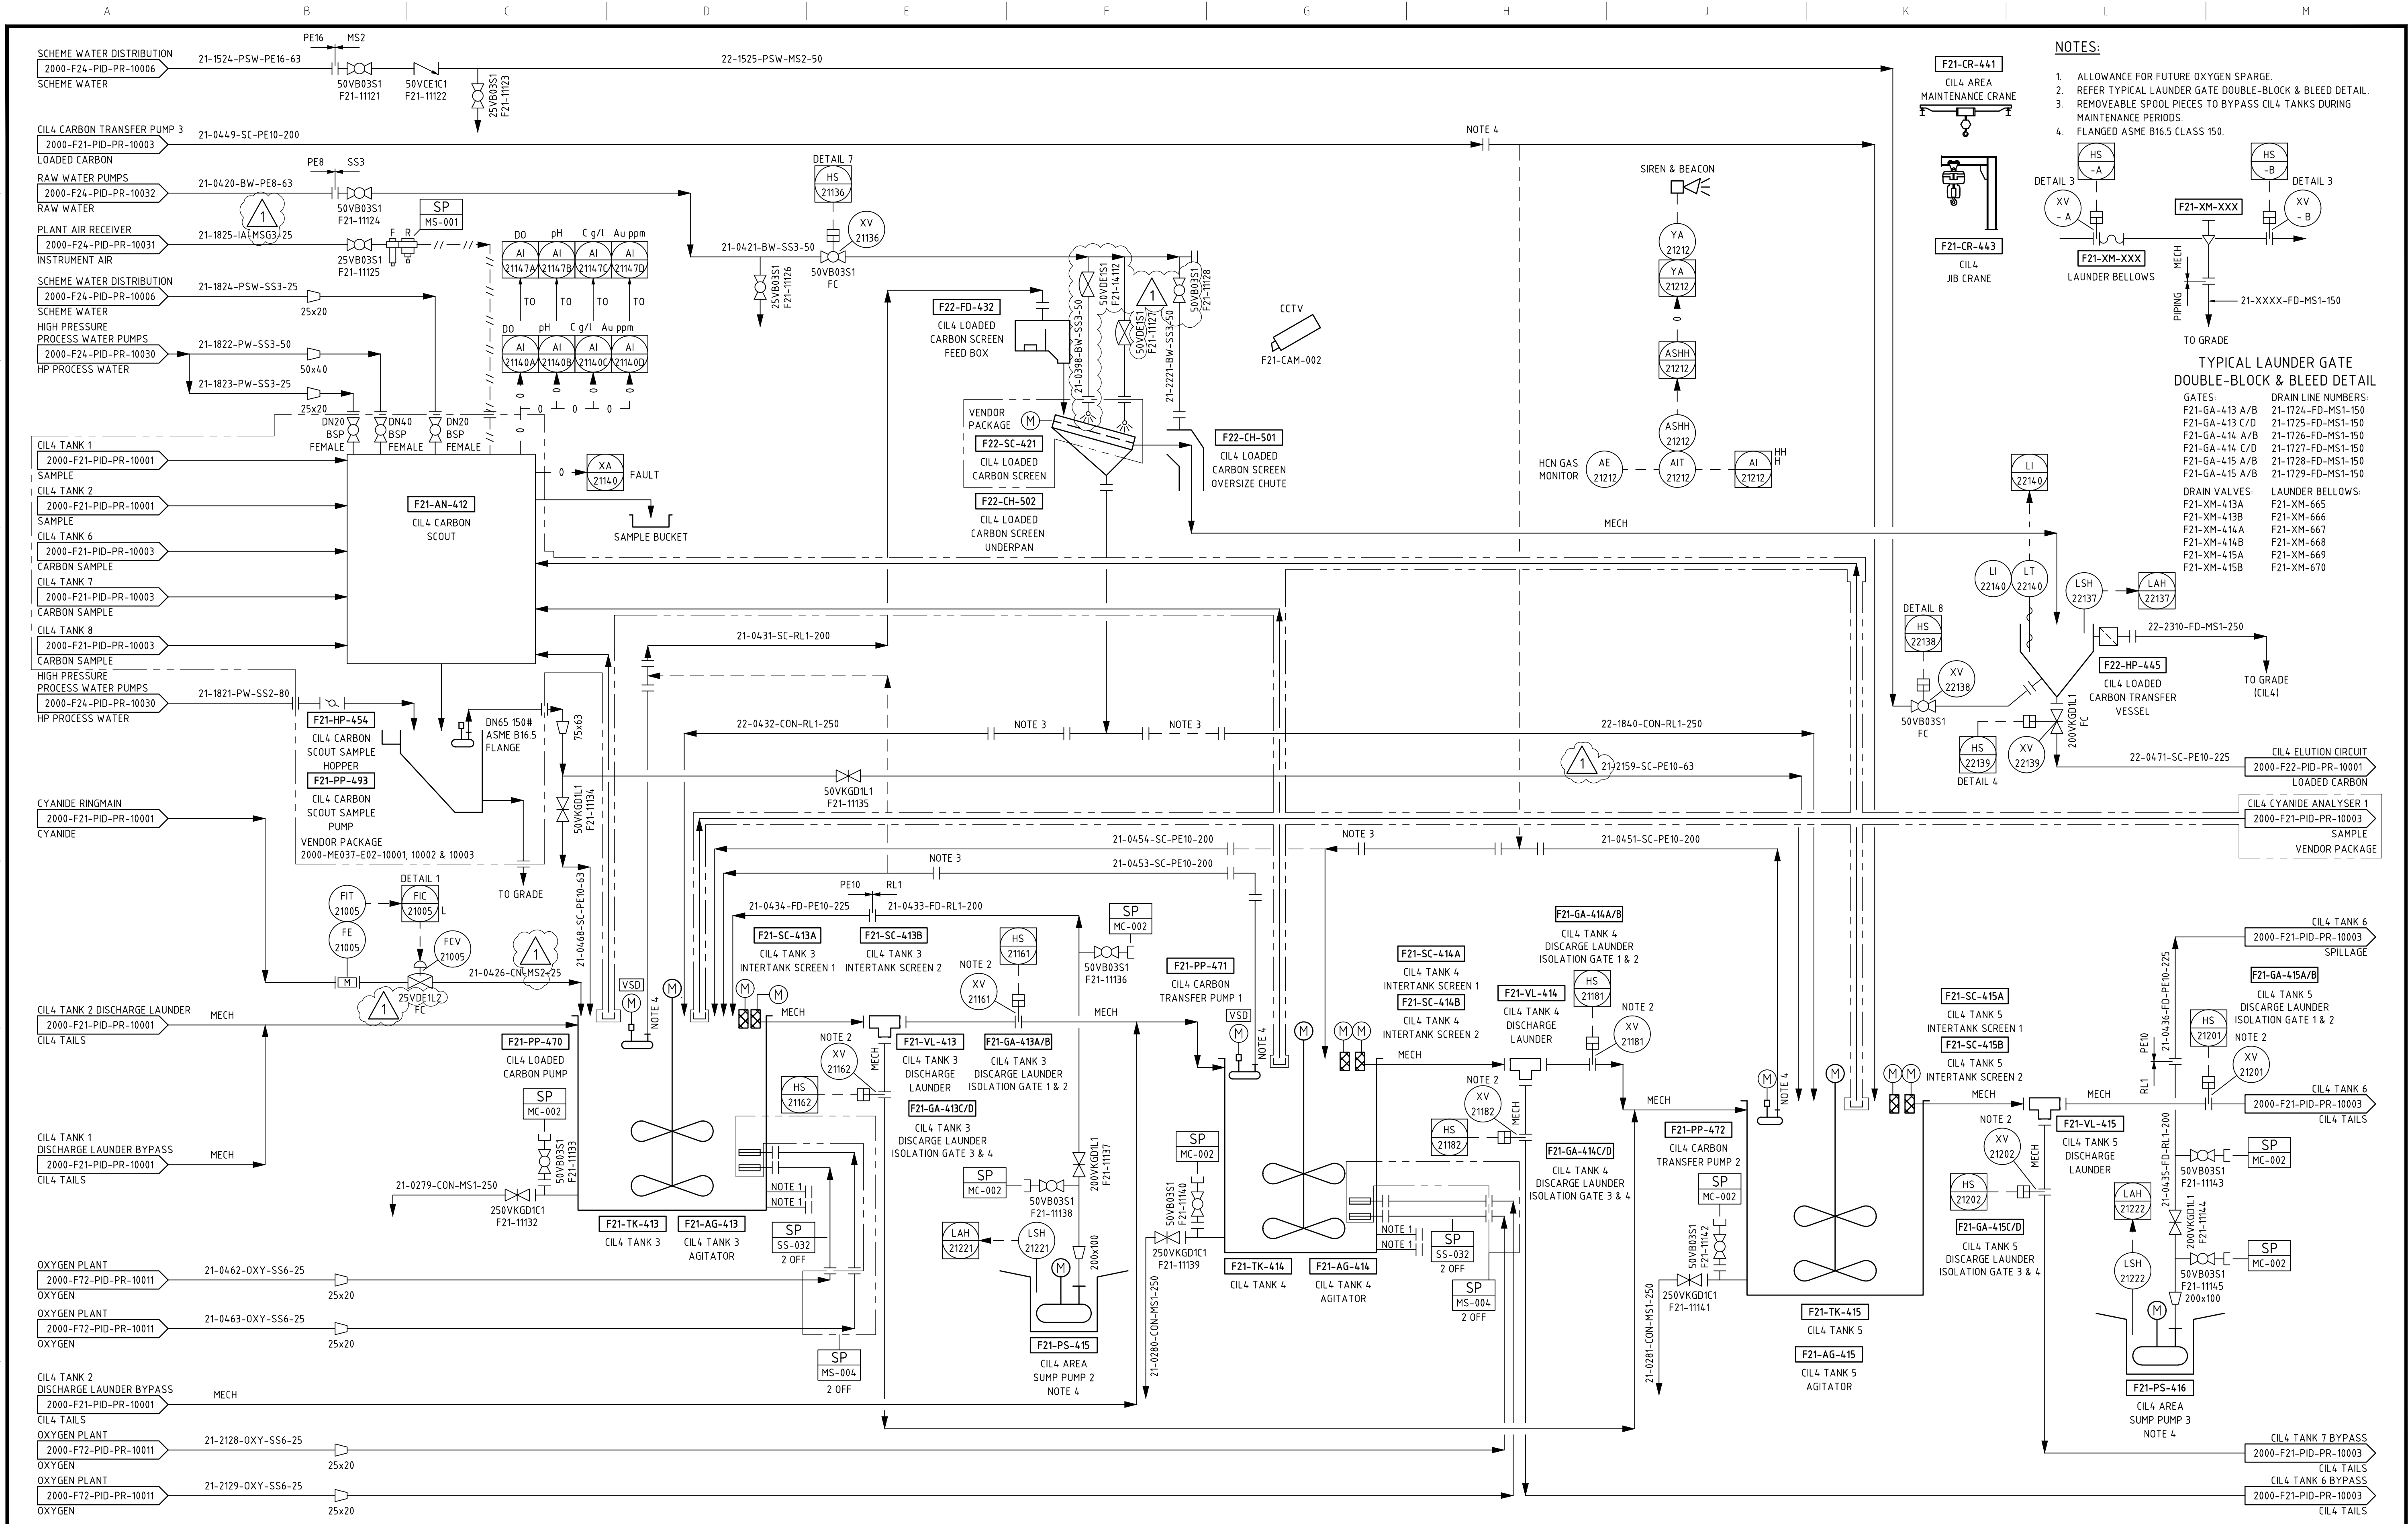

NOTES:

1. ALLOWANCE FOR FUTURE OXYGEN SPARGE.
2. REFER TYPICAL LAUNDER GATE DOUBLE-BLOCK & BLEED DETAIL.
3. REMOVEABLE SPOOL PIECES TO BYPASS CIL4 TANKS DURING MAINTENANCE PERIODS.
4. FLANGED ASME B16.5 CLASS 150.

TYPICAL LAUNDER GATE DOUBLE-BLOCK & BLEED DETAIL

- GATES:
- | | |
|----------------|--------------------|
| F21-GA-413 A/B | 21-1724-FD-MS1-150 |
| F21-GA-413 C/D | 21-1725-FD-MS1-150 |
| F21-GA-414 A/B | 21-1726-FD-MS1-150 |
| F21-GA-414 C/D | 21-1727-FD-MS1-150 |
| F21-GA-415 A/B | 21-1728-FD-MS1-150 |
| F21-GA-415 A/B | 21-1729-FD-MS1-150 |
- LAUNDER BELLOWS:
- | | |
|-------------|------------|
| F21-XM-413A | F21-XM-665 |
| F21-XM-413B | F21-XM-666 |
| F21-XM-414A | F21-XM-667 |
| F21-XM-414B | F21-XM-668 |
| F21-XM-415A | F21-XM-669 |
| F21-XM-415B | F21-XM-670 |

ORG No.	REFERENCES	REV	DATE	DESCRIPTION	DRAW	CHECK	DESIGN	TECH APP	PROJ APP
2000-F00-PID-PR-10007	LEGEND SHEET 7 - PIPING AND INSTRUMENTATION DIAGRAM								
2000-F00-PID-PR-10006	LEGEND SHEET 6 - PIPING AND INSTRUMENTATION DIAGRAM								
2000-F00-PID-PR-10005	LEGEND SHEET 5 - PIPING AND INSTRUMENTATION DIAGRAM								
2000-F00-PID-PR-10004	LEGEND SHEET 4 - PIPING AND INSTRUMENTATION DIAGRAM								
2000-F00-PID-PR-10003	LEGEND SHEET 3 - PIPING AND INSTRUMENTATION DIAGRAM								
2000-F00-PID-PR-10002	LEGEND SHEET 2 - PIPING AND INSTRUMENTATION DIAGRAM								
2000-F00-PID-PR-10001	LEGEND SHEET 1 - PIPING AND INSTRUMENTATION DIAGRAM								



INFORMATION AND REPRESENTATIONS ON THIS DRAWING ARE THE INTELLECTUAL PROPERTY OF PRIMERO UNLESS SPECIFICALLY IDENTIFIED OTHERWISE. ALL RIGHTS INCLUDING USE RESERVED

PROJECT:	NORTHERN STAR RESOURCES LTD KCGM GROWTH PROJECT		
TITLE:	FLOTATION TAILINGS CIL4 CIL4 - FLOTATION TAILS LEACHING - SHEET 2 PIPING AND INSTRUMENTATION DIAGRAM		
SHEET	A1	SCALE	NTS
DRG No.	2000-F21-PID-PR-10002		
REVISION	1		