


APPROVED FOR
CONSTRUCTION

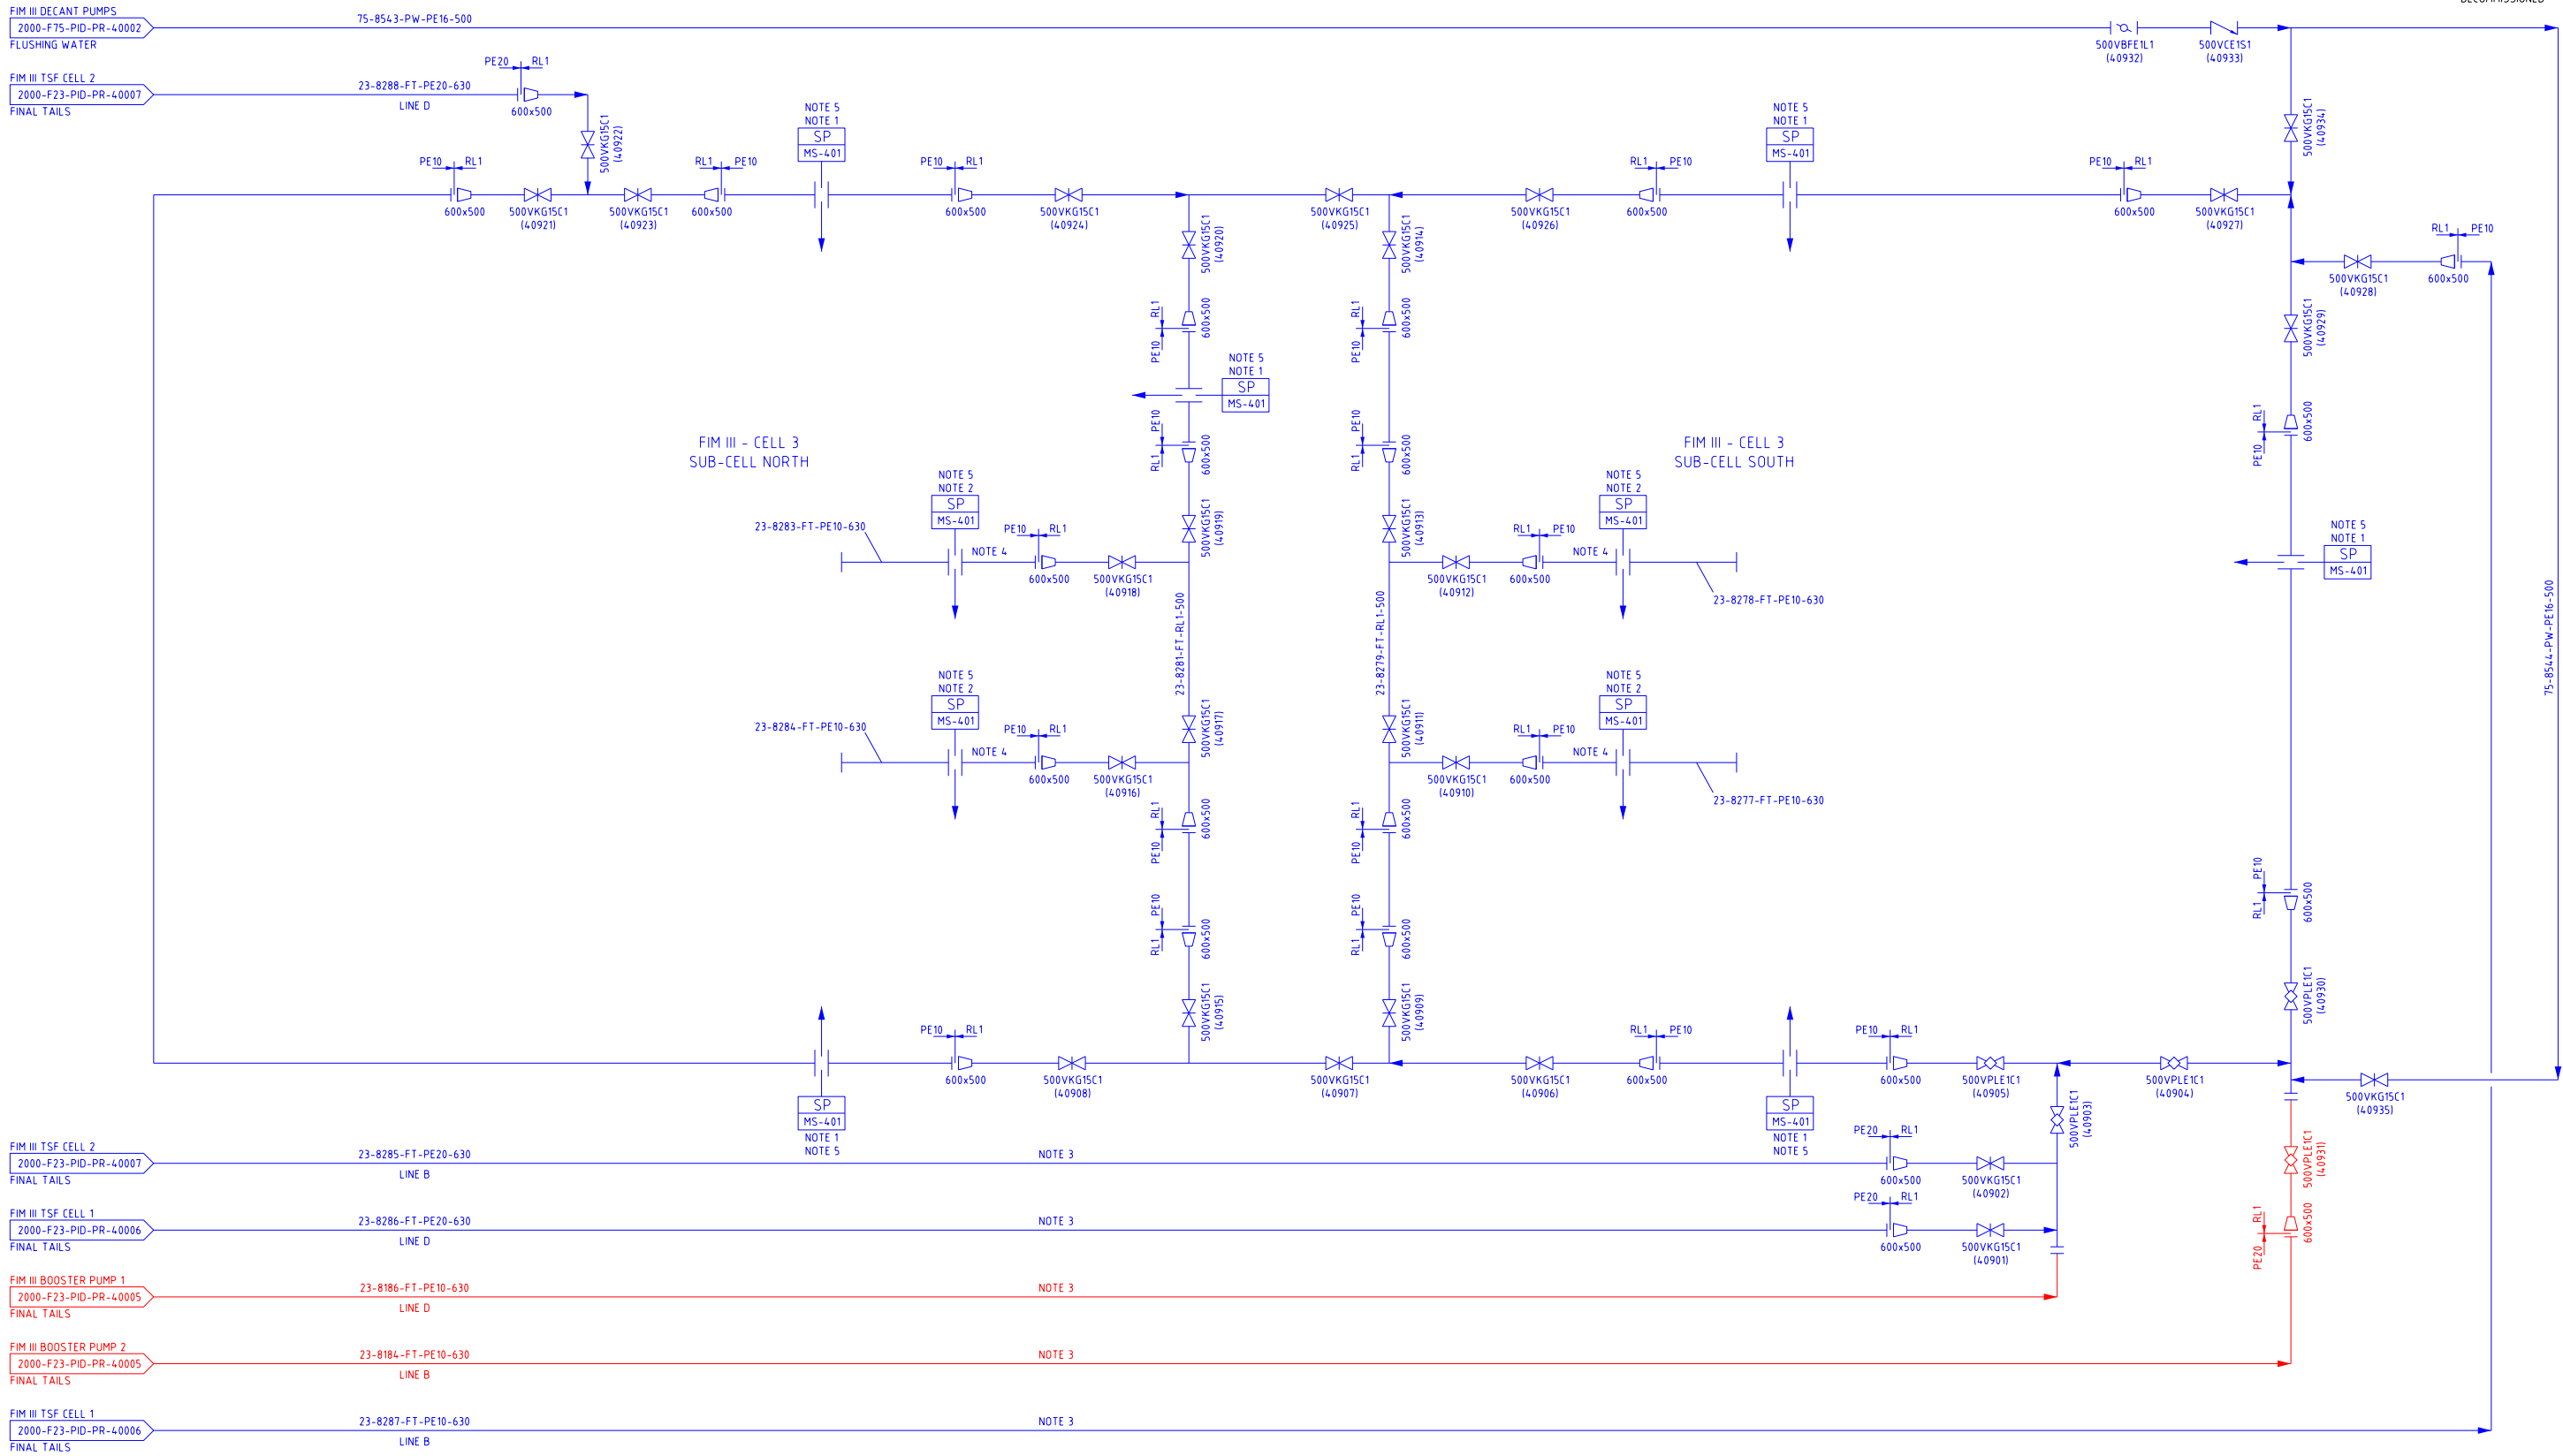

- | <u>NOTES:</u> | | <u>LEGEND:</u> | |
|---------------|--|----------------|----------------|
| 1. | SPIGOTS PLACED AT 40m CENTRES UNLESS OTHERWISE NOTED. | ————— | EXISTING |
| 2. | SPIGOTS PLACED AT 15m CENTRES ON THE CAUSEWAYS. | | |
| 3. | PIPING ON TSF EMBANKMENT TO BE FLANGED EVERY 40m. | | |
| 4. | CAUSEWAY PIPING TO BE FLANGED EVERY 15m. | ————— | NEW |
| 5. | REFER TO DRAWING 2000-T03-DRG-GE-40003
FOR SPIGOT DETAILS, A TOTAL OF 244 SPIGOTS REQUIRED
WITH UNIQUE VALVE NUMBERS 43801 TO 44044. | ————— | FUTURE |
| | | — — — — — | DECOMMISSIONED |

[illegible]

DRA PACIFIC (PTY) LIMITED

PROJECT		KCGM GROWTH PROJECT	
TITLE		FINAL TAILINGS HANDLING AND STORAGE FIM III DEPOSITION CELL 3 PIPING AND INSTRUMENTATION DIAGRAM	
SHEET A1	SCALE NTS	DRG No. 2000-F23-PID-PR-40008	REVISION 0