


D:\CAD PROJECTS\235 NORTHERN STAR RESOURCES LTD\23517 KCGM GROWTH PROJECT\03 DELIVERABLES\PR\PID\2000-F24-PID-PR-1001_1.DWG 11JUL25 11:11AM ANNE HOYNE

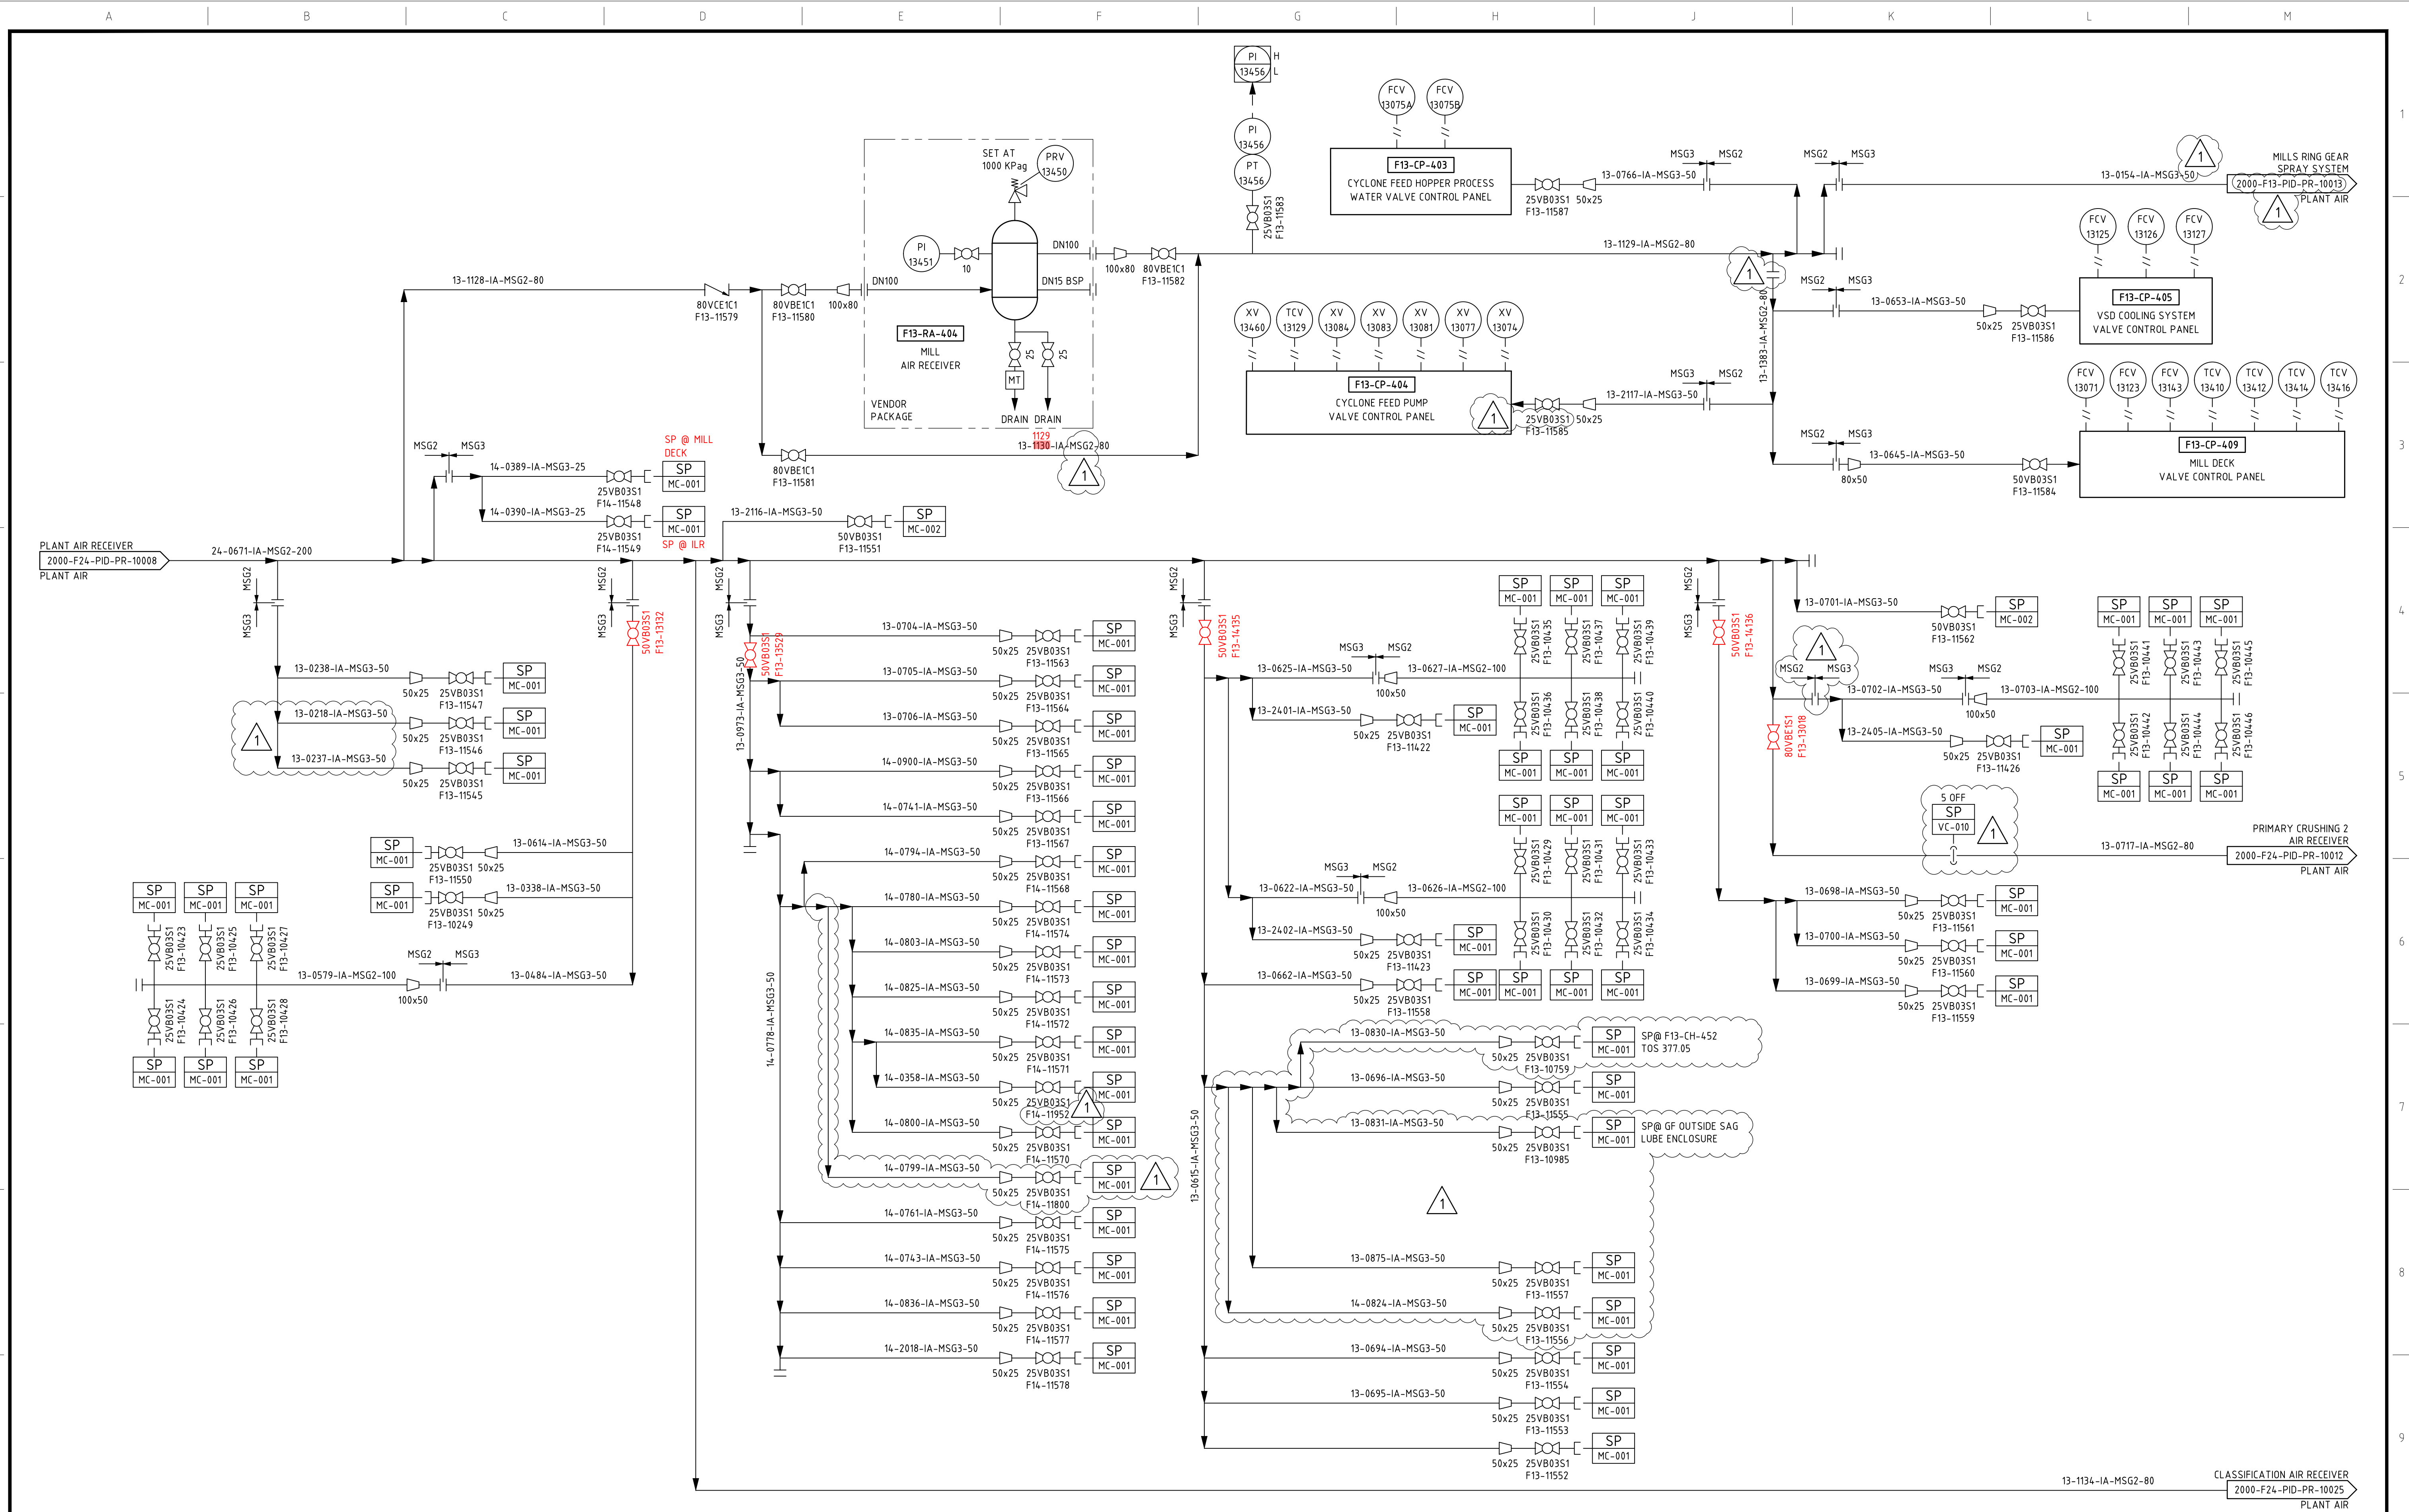

2000-F00-PID-PR-10007		LEGEND SHEET 7 - PIPING AND INSTRUMENTATION DIAGRAM													
2000-F00-PID-PR-10006		LEGEND SHEET 6 - PIPING AND INSTRUMENTATION DIAGRAM													
2000-F00-PID-PR-10005		LEGEND SHEET 5 - PIPING AND INSTRUMENTATION DIAGRAM													
2000-F00-PID-PR-10004		LEGEND SHEET 4 - PIPING AND INSTRUMENTATION DIAGRAM													
2000-F00-PID-PR-10003		LEGEND SHEET 3 - PIPING AND INSTRUMENTATION DIAGRAM													
2000-F00-PID-PR-10002		LEGEND SHEET 2 - PIPING AND INSTRUMENTATION DIAGRAM													
2000-F00-PID-PR-10001		LEGEND SHEET 1 - PIPING AND INSTRUMENTATION DIAGRAM													
ORG No.		REFERENCES		REV		DATE		DESCRIPTION		DRAW		CHECK		DESIGN	

		PRIMERO		PROJECT: NORTHERN STAR RESOURCES LTD KCGM GROWTH PROJECT	
primero.com.au DESIGN CONSTRUCT OPERATE		PRIMERO PROJECT NUMBER: 23517		TITLE: AIR & WATER SERVICES PLANT AIR - SHEET 3 PIPING AND INSTRUMENTATION DIAGRAM	
INFORMATION AND REPRESENTATIONS ON THIS DRAWING ARE THE INTELLECTUAL PROPERTY OF PRIMERO UNLESS SPECIFICALLY IDENTIFIED OTHERWISE. ALL RIGHTS INCLUDING USE RESERVED		SHEET: A1		SCALE: NTS	
		DRG No. 2000-F24-PID-PR-10011		REVISION: 1	