


D:\CAD PROJECTS\235 NORTHERN STAR RESOURCES LTD\23517 KCGM GROWTH PROJECT\03 DELIVERABLES\PR\PID\ISSUED\12.09.25 - SIGNING\NATIVES\2000-F24-PID-PR-10012_2.DWG (05EP25 10:43AM ANNE HOYNE)

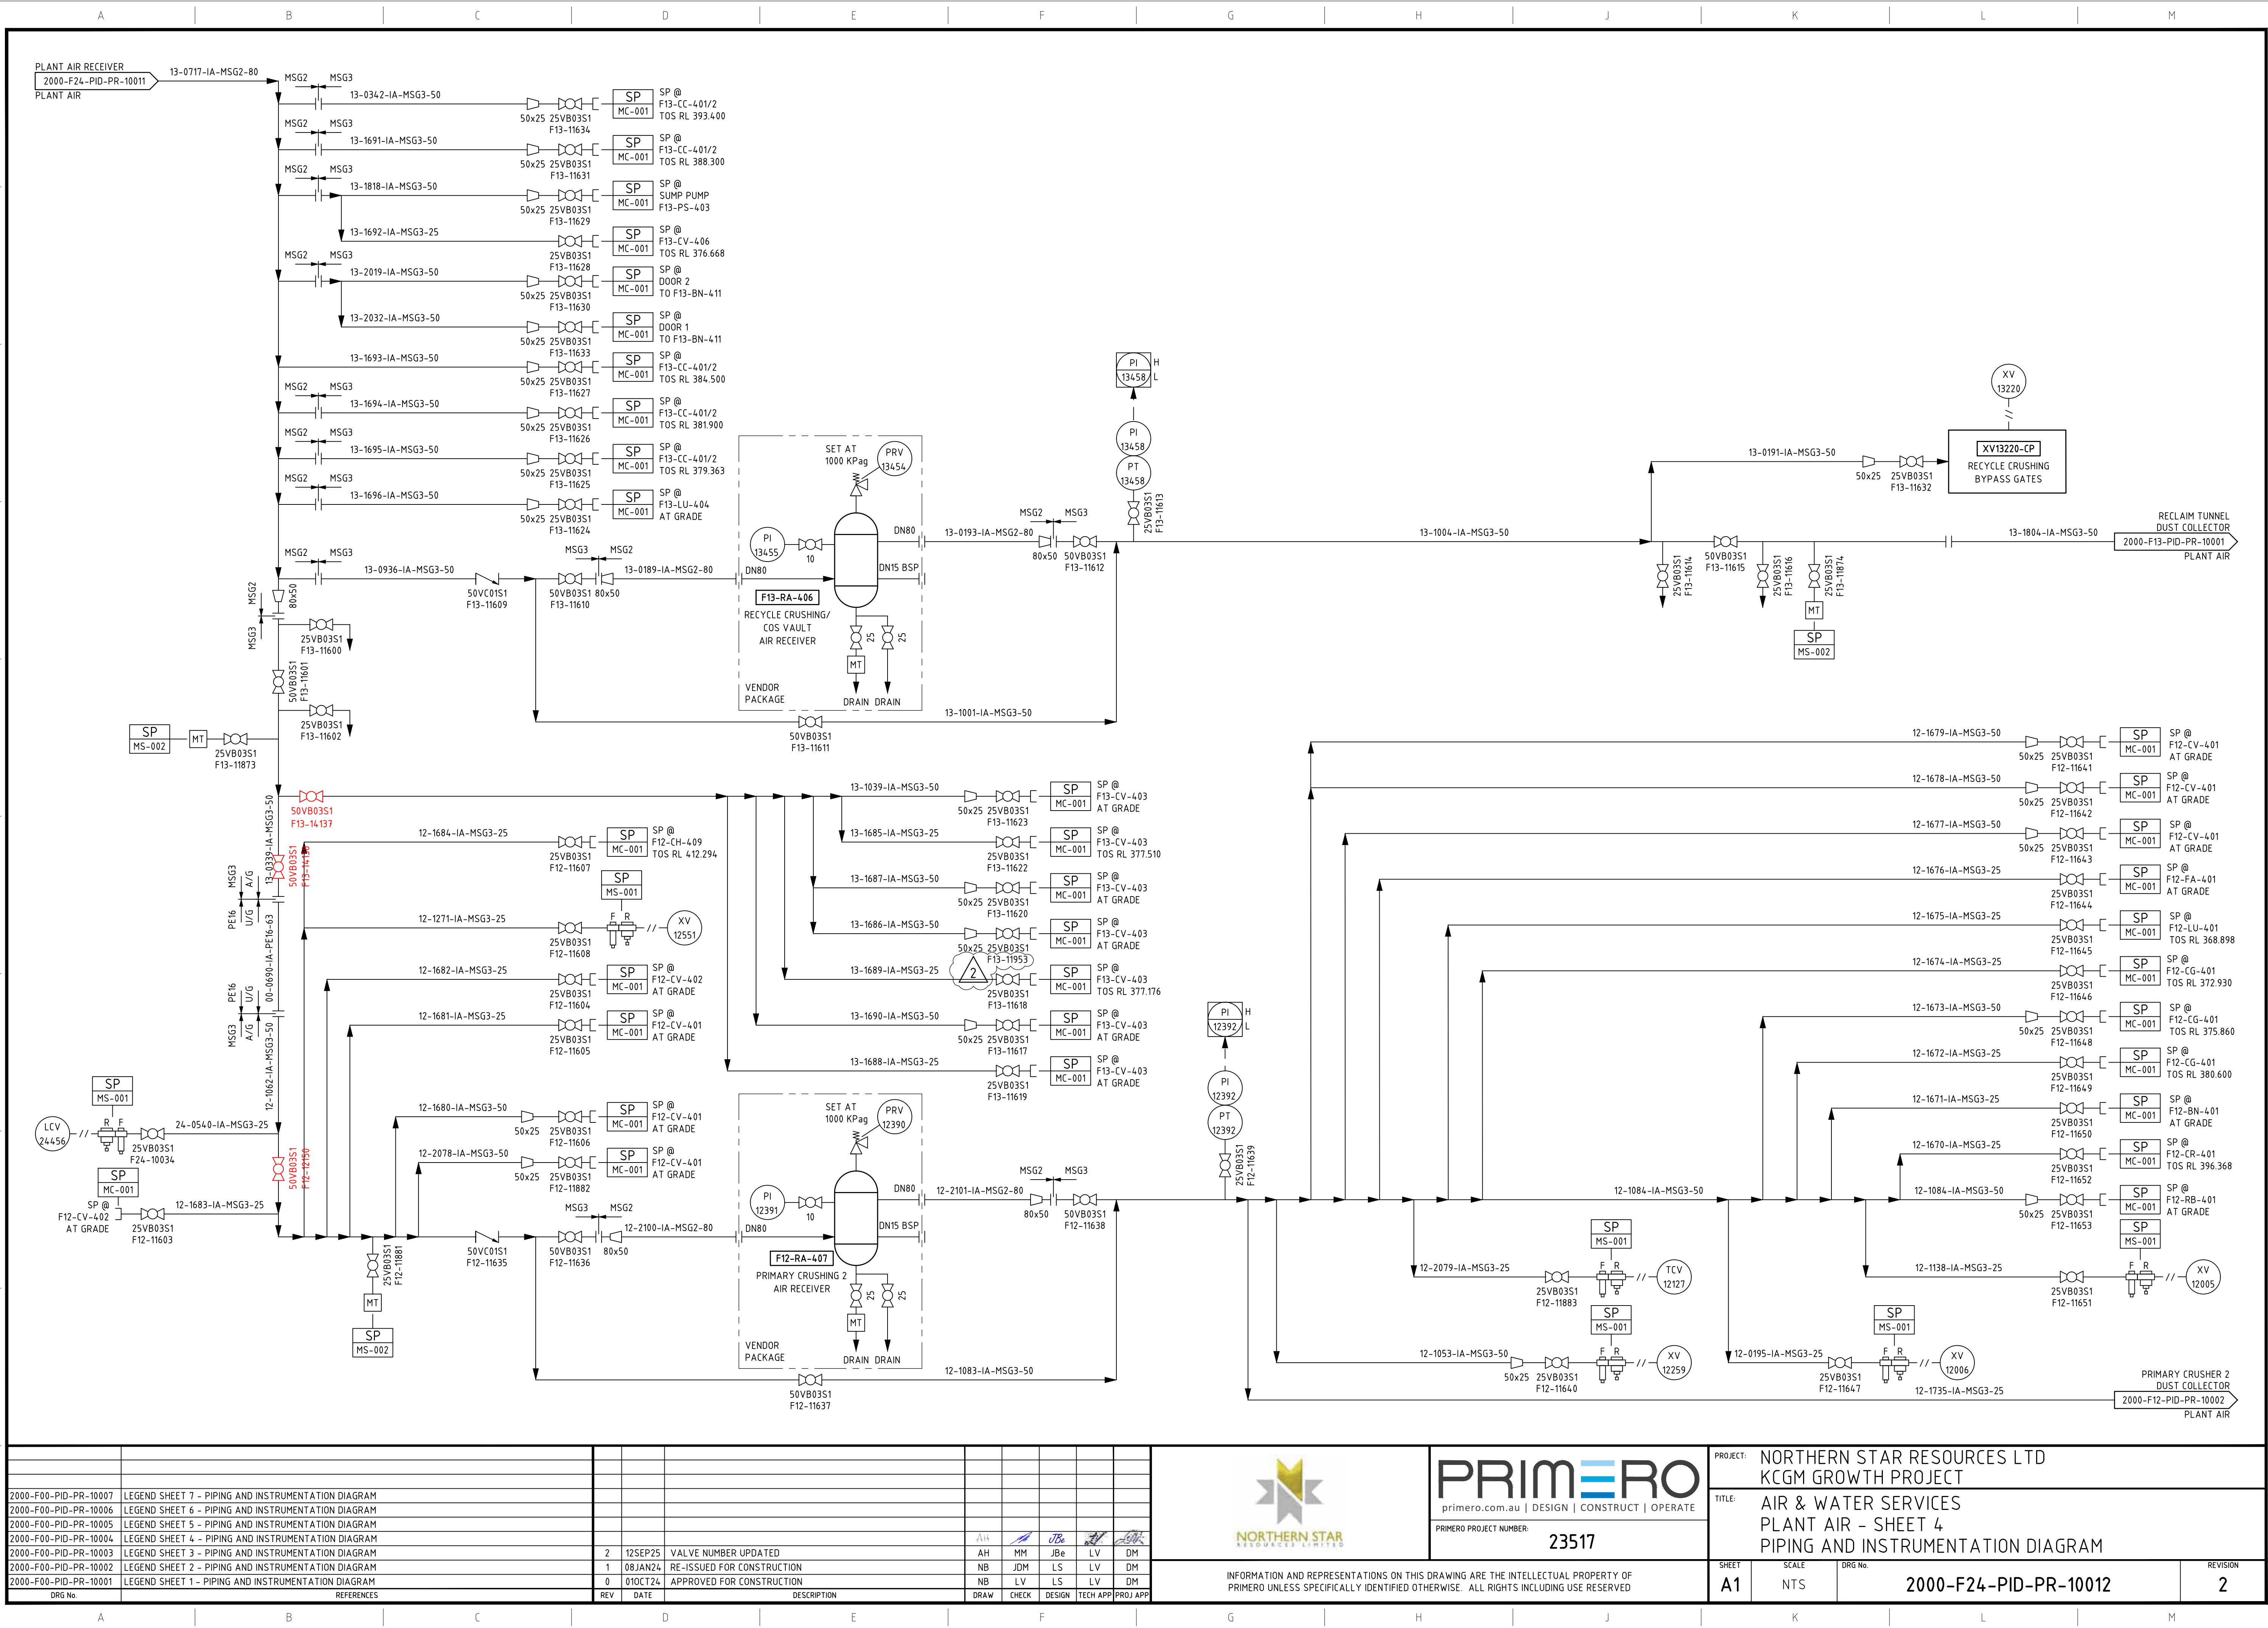

DRG No.	REFERENCES	REV	DATE	DESCRIPTION	DRAW	CHECK	DESIGN	TECH APP	PROJ APP
2000-F00-PID-PR-10007	LEGEND SHEET 7 - PIPING AND INSTRUMENTATION DIAGRAM								
2000-F00-PID-PR-10006	LEGEND SHEET 6 - PIPING AND INSTRUMENTATION DIAGRAM								
2000-F00-PID-PR-10005	LEGEND SHEET 5 - PIPING AND INSTRUMENTATION DIAGRAM								
2000-F00-PID-PR-10004	LEGEND SHEET 4 - PIPING AND INSTRUMENTATION DIAGRAM								
2000-F00-PID-PR-10003	LEGEND SHEET 3 - PIPING AND INSTRUMENTATION DIAGRAM								
2000-F00-PID-PR-10002	LEGEND SHEET 2 - PIPING AND INSTRUMENTATION DIAGRAM								
2000-F00-PID-PR-10001	LEGEND SHEET 1 - PIPING AND INSTRUMENTATION DIAGRAM								
2	12SEP25	VALVE NUMBER UPDATED	AH	MM	JBe	LV	DM		
1	08JAN24	RE-ISSUED FOR CONSTRUCTION	NB	JDM	LS	LV	DM		
0	01OCT24	APPROVED FOR CONSTRUCTION	NB	LV	LS	LV	DM		



PROJECT:	NORTHERN STAR RESOURCES LTD KCGM GROWTH PROJECT		
TITLE:	AIR & WATER SERVICES PLANT AIR - SHEET 4 PIPING AND INSTRUMENTATION DIAGRAM		
SHEET:	A1	SCALE:	NTS
DRG No.:	2000-F24-PID-PR-10012		REVISION:
		2	