


D:\CAD PROJECTS\235 NORTHERN STAR RESOURCES LTD\23517 KCGM GROWTH PROJECT\3 DELIVERABLES\PRP\PID\ISSUED\12.09.25 - SIGNING\NATIVES\2000-F24-PID-PR-10018_1.DWG 10SEP25 11:03AM ANNE HOYNE

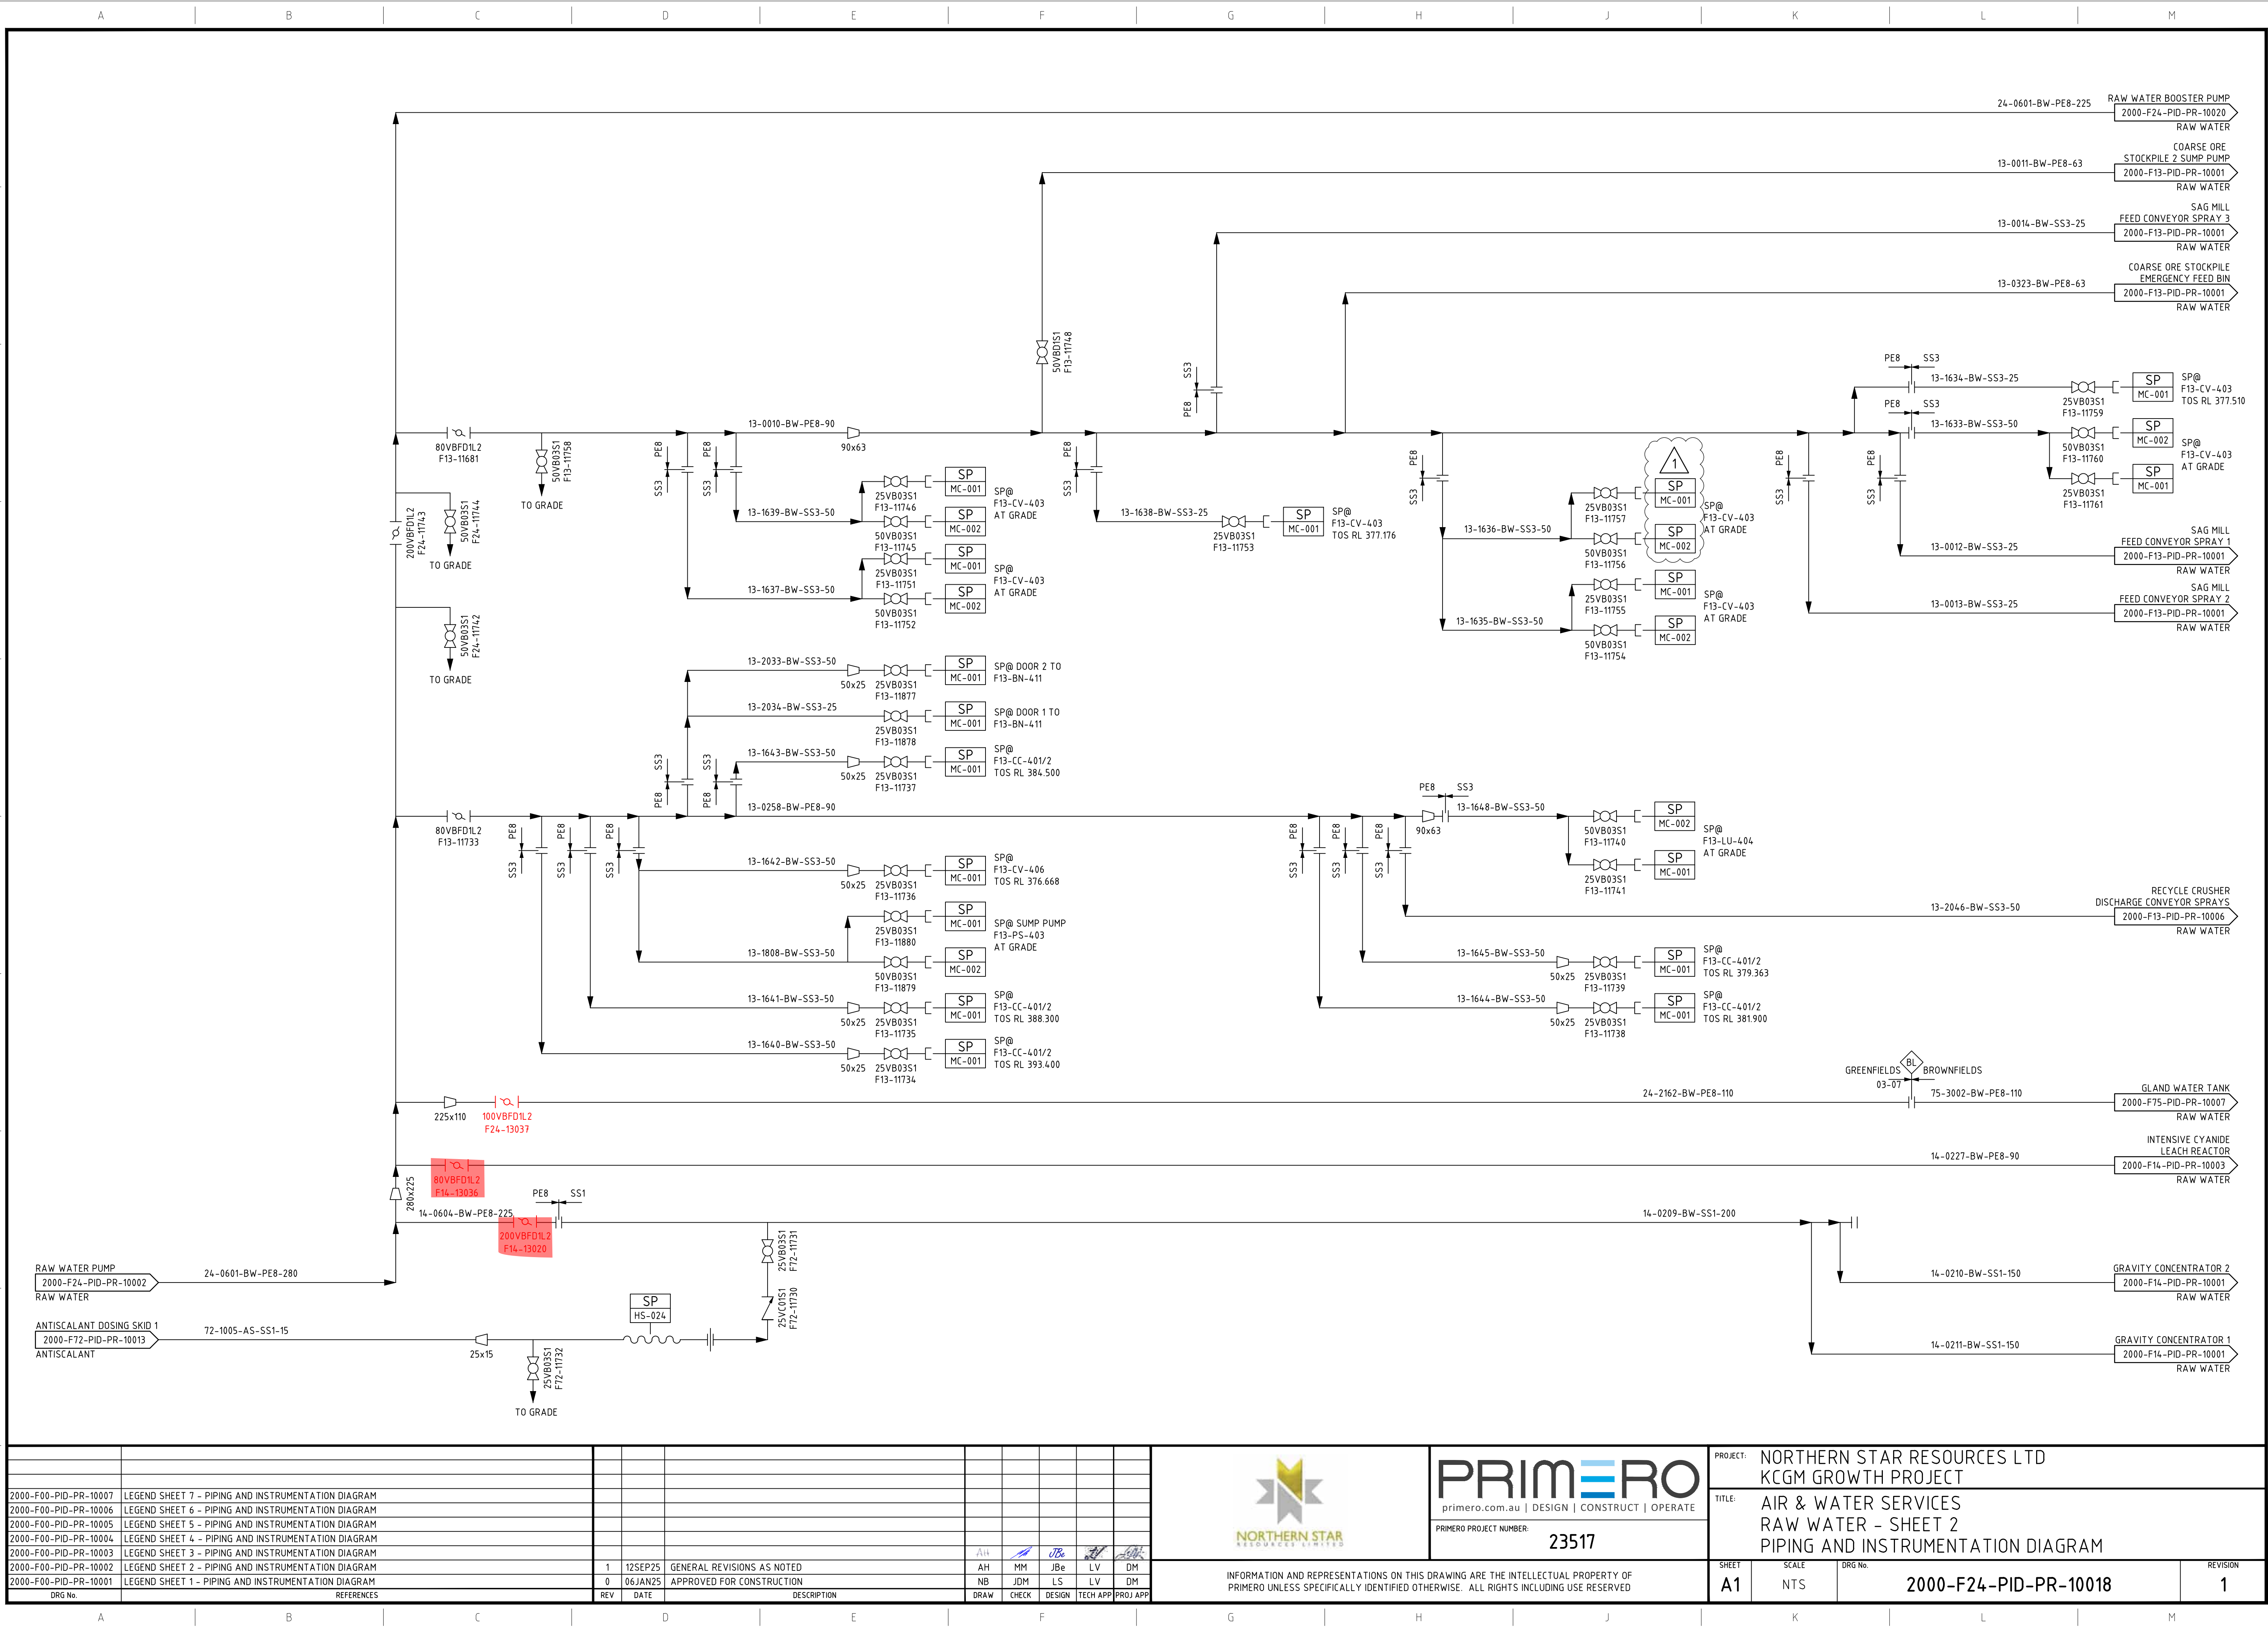

LEGEND	LEGEND SHEET 7 - PIPING AND INSTRUMENTATION DIAGRAM	REV	DATE	DESCRIPTION	DRAW	CHECK	DESIGN	TECH APP	PROJ APP
2000-F00-PID-PR-10007	LEGEND SHEET 7 - PIPING AND INSTRUMENTATION DIAGRAM	1	12SEP25	GENERAL REVISIONS AS NOTED	AH	MM	JBe	LV	DM
2000-F00-PID-PR-10006	LEGEND SHEET 6 - PIPING AND INSTRUMENTATION DIAGRAM	0	06JAN25	APPROVED FOR CONSTRUCTION	NB	JDM	LS	LV	DM
2000-F00-PID-PR-10005	LEGEND SHEET 5 - PIPING AND INSTRUMENTATION DIAGRAM								
2000-F00-PID-PR-10004	LEGEND SHEET 4 - PIPING AND INSTRUMENTATION DIAGRAM								
2000-F00-PID-PR-10003	LEGEND SHEET 3 - PIPING AND INSTRUMENTATION DIAGRAM								
2000-F00-PID-PR-10002	LEGEND SHEET 2 - PIPING AND INSTRUMENTATION DIAGRAM								
2000-F00-PID-PR-10001	LEGEND SHEET 1 - PIPING AND INSTRUMENTATION DIAGRAM								
DRG No.	REFERENCES	REV	DATE	DESCRIPTION	DRAW	CHECK	DESIGN	TECH APP	PROJ APP



INFORMATION AND REPRESENTATIONS ON THIS DRAWING ARE THE INTELLECTUAL PROPERTY OF PRIMERO UNLESS SPECIFICALLY IDENTIFIED OTHERWISE. ALL RIGHTS INCLUDING USE RESERVED

PROJECT:	NORTHERN STAR RESOURCES LTD KCGM GROWTH PROJECT			REVISION
TITLE:	AIR & WATER SERVICES RAW WATER - SHEET 2 PIPING AND INSTRUMENTATION DIAGRAM			
SHEET	A1	SCALE	NTS	
DRG No.	2000-F24-PID-PR-10018			1