


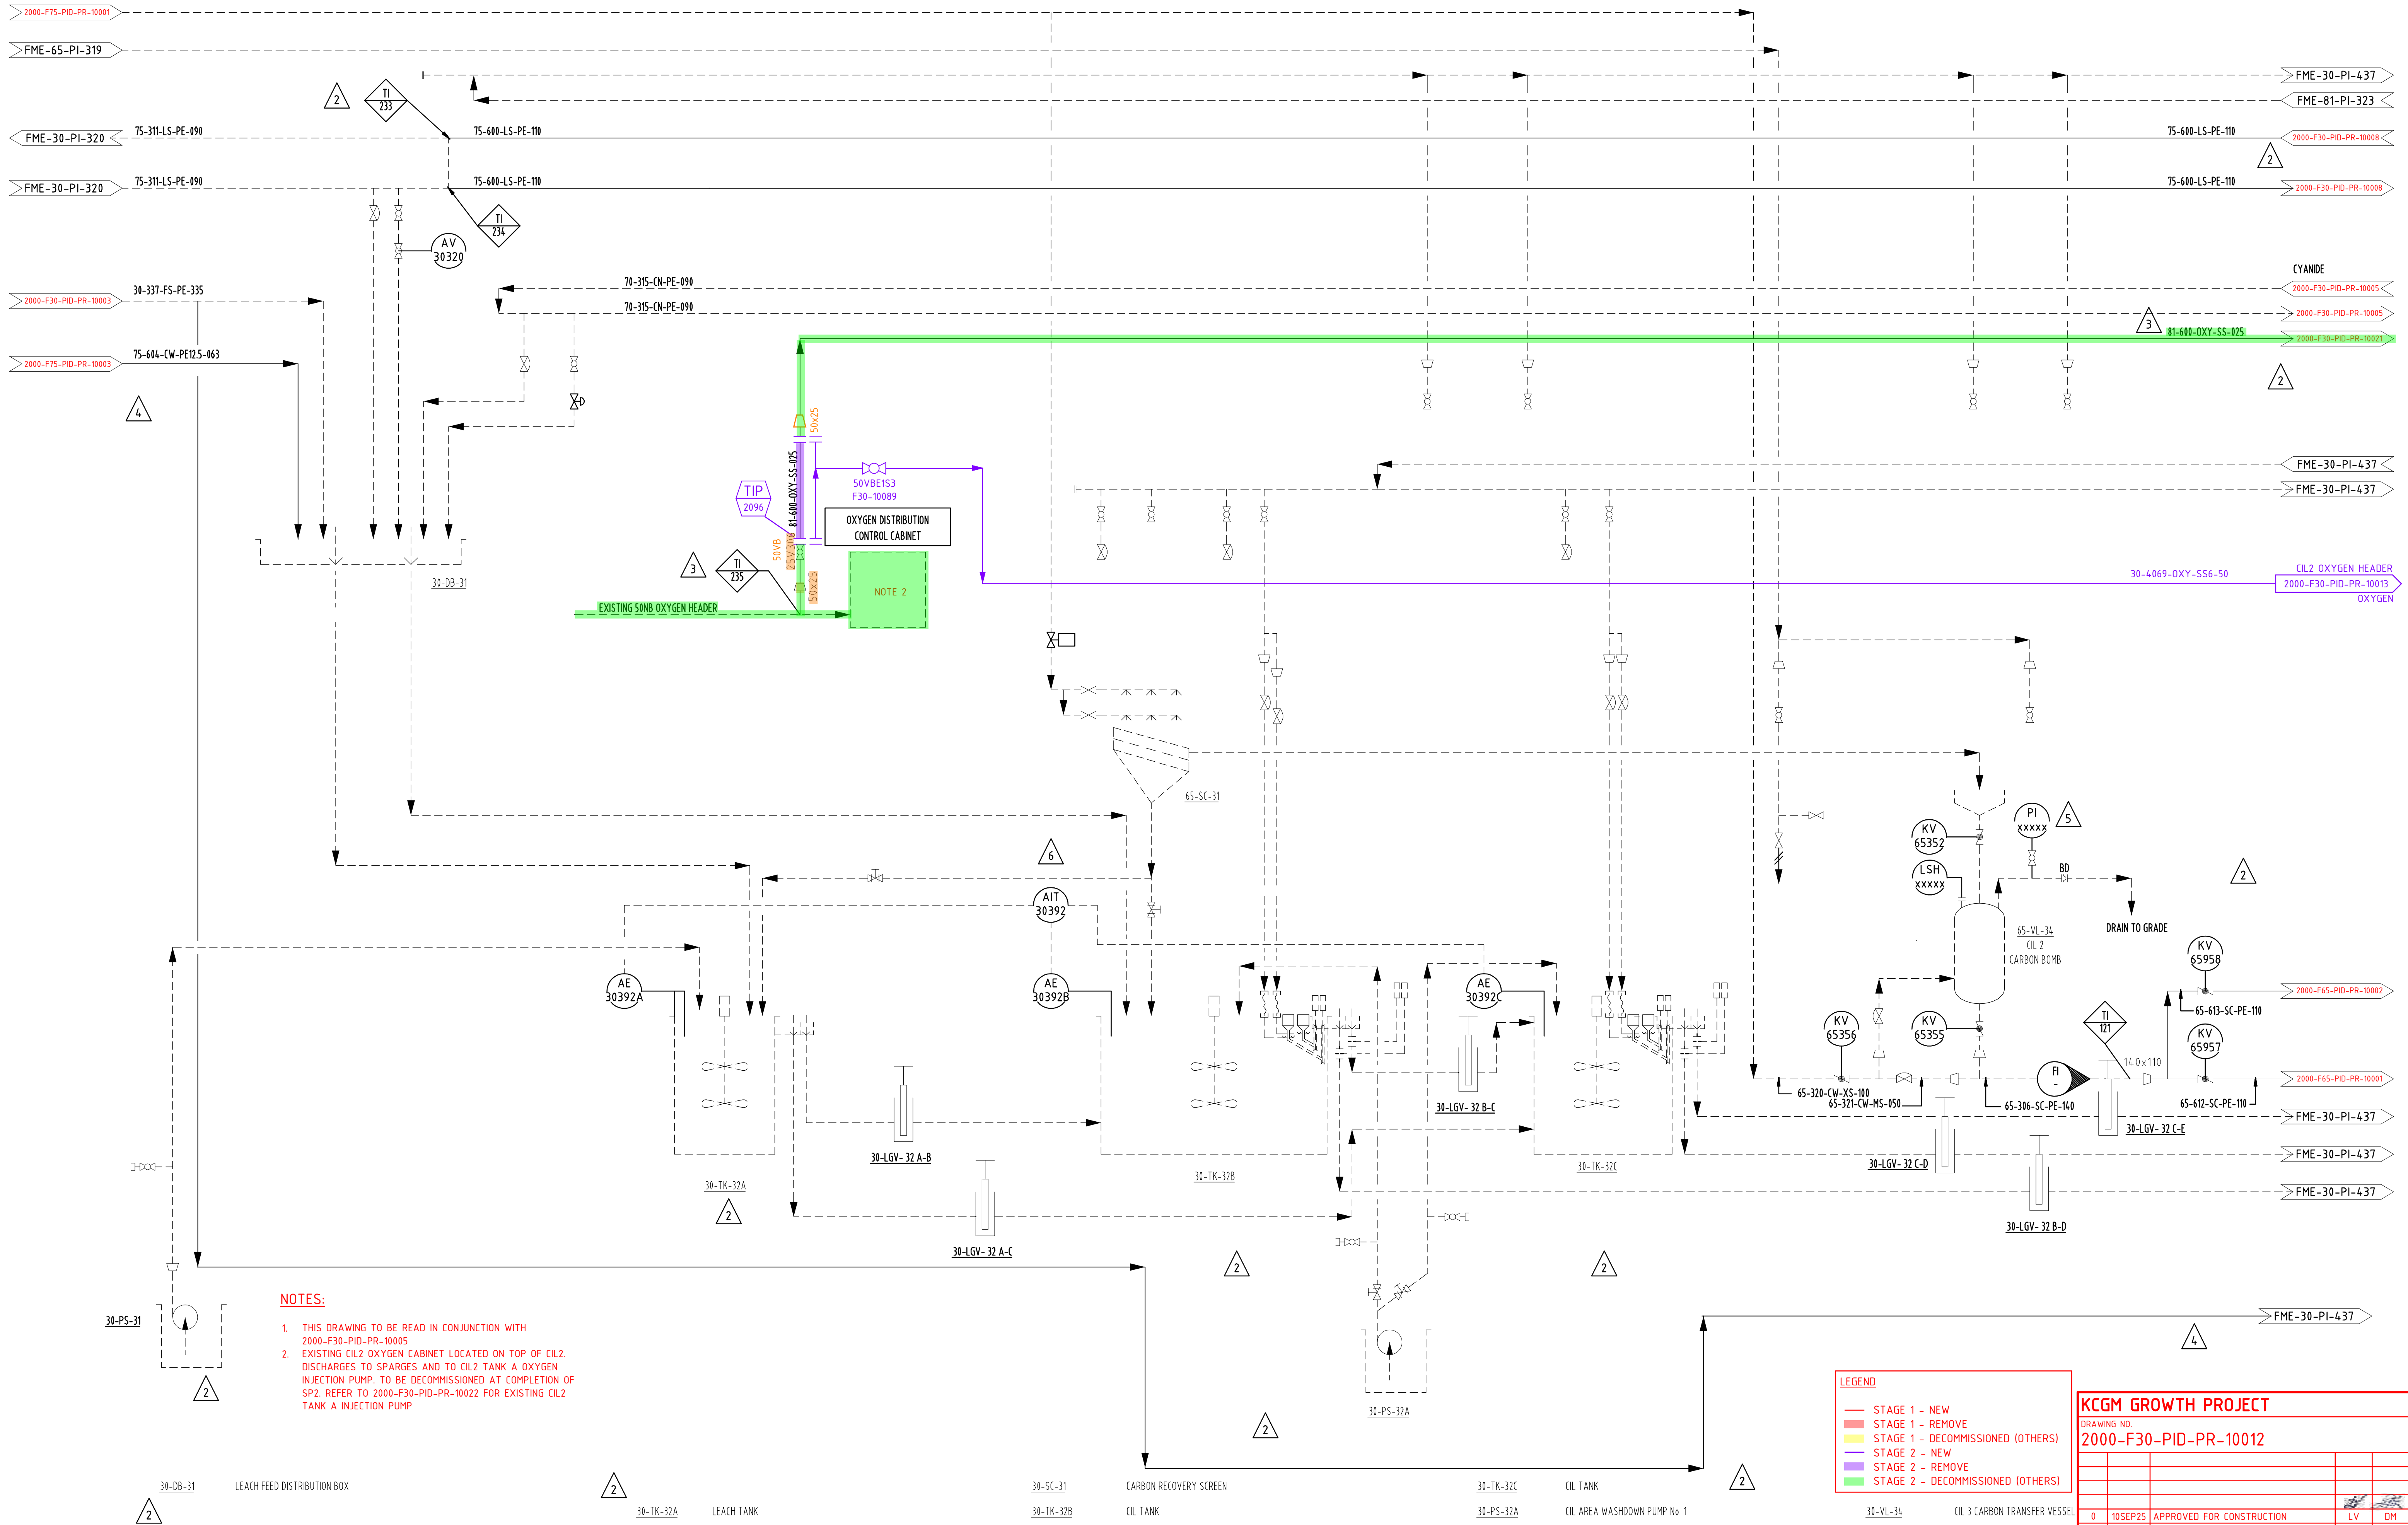

NOTES:

1. THIS DRAWING TO BE READ IN CONJUNCTION WITH 2000-F30-PID-PR-10005
2. EXISTING CIL2 OXYGEN CABINET LOCATED ON TOP OF CIL2. DISCHARGES TO SPARGES AND TO CIL2 TANK A OXYGEN INJECTION PUMP. TO BE DECOMMISSIONED AT COMPLETION OF SP2. REFER TO 2000-F30-PID-PR-10022 FOR EXISTING CIL2 TANK A INJECTION PUMP

LEGEND

- STAGE 1 - NEW
- STAGE 1 - REMOVE
- STAGE 1 - DECOMMISSIONED (OTHERS)
- STAGE 2 - NEW
- STAGE 2 - REMOVE
- STAGE 2 - DECOMMISSIONED (OTHERS)

KCGM GROWTH PROJECT

DRAWING NO.  
2000-F30-PID-PR-10012

| REV | DATE    | DESCRIPTION               | LV | DM |
|-----|---------|---------------------------|----|----|
| 0   | 10SEP25 | APPROVED FOR CONSTRUCTION |    |    |

| REV | DATE    | DESCRIPTION               | CHECK | TECH | APP |
|-----|---------|---------------------------|-------|------|-----|
| 1   | 10SEP25 | APPROVED FOR CONSTRUCTION |       |      |     |

| DRAWING No. | REFERENCE DRAWINGS |
|-------------|--------------------|
|             |                    |

|   |
|---|
| COPYRIGHT ©   |
| This drawing remains the property of MINPROC ENGINEERS LIMITED and may not be copied in any way without prior written approval from this company. |

MINPROC ENGINEERS LIMITED  
A.C.N. 008 992 694  
22, STIRLING HIGHWAY, NEDLANDS WA 6009  
PHONE (09) 347 4777

| No. | BY   | DATE       | REVISION         | CHECKED | APPROV. |
|-----|------|------------|------------------|---------|---------|
| 7   | L.W. | 30.03.2020 | REVISED AS NOTED | T.R.    | -       |

| No. | BY | DATE     | REVISION                | CHECKED | APPROV. |
|-----|----|----------|-------------------------|---------|---------|
| 6   | RH | 17/04/18 | LOOP AIT30392 INSTALLED | DC      | DC      |


| PROJECT APPR. | BY          | DATE   |
|---------------|-------------|--------|
|               | M.LANGRIDGE | 6/5/95 |

| DESIGN APPR. | BY       | DATE   |
|--------------|----------|--------|
|              | D.TAYLOR | 5/5/95 |

| DESIGNED | BY           | DATE   |
|----------|--------------|--------|
|          | G.TORKINGTON | 5/5/95 |

| CHECKED | BY           | DATE    |
|---------|--------------|---------|
|         | G.TORKINGTON | 30/4/95 |

| DRAWN | BY     | DATE    |
|-------|--------|---------|
|       | F.WARD | 27/7/94 |

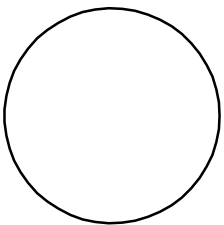

| CLIENT | KALGOORLIE CONSOLIDATED GOLD MINES                                                                |
|--------|---------------------------------------------------------------------------------------------------|
| TITLE  | FIMISTON EXPANSION 1994/95<br>PIPING & INSTRUMENTATION DIAGRAM<br>LEACH AND ADSORPTION - CIL No.2 |

| SIZE        | B1         |
|-------------|------------|
| SCALE       | N.T.S.     |
| REV. No.    | 1          |
| DRAWING No. | 30\PI\0436 |