


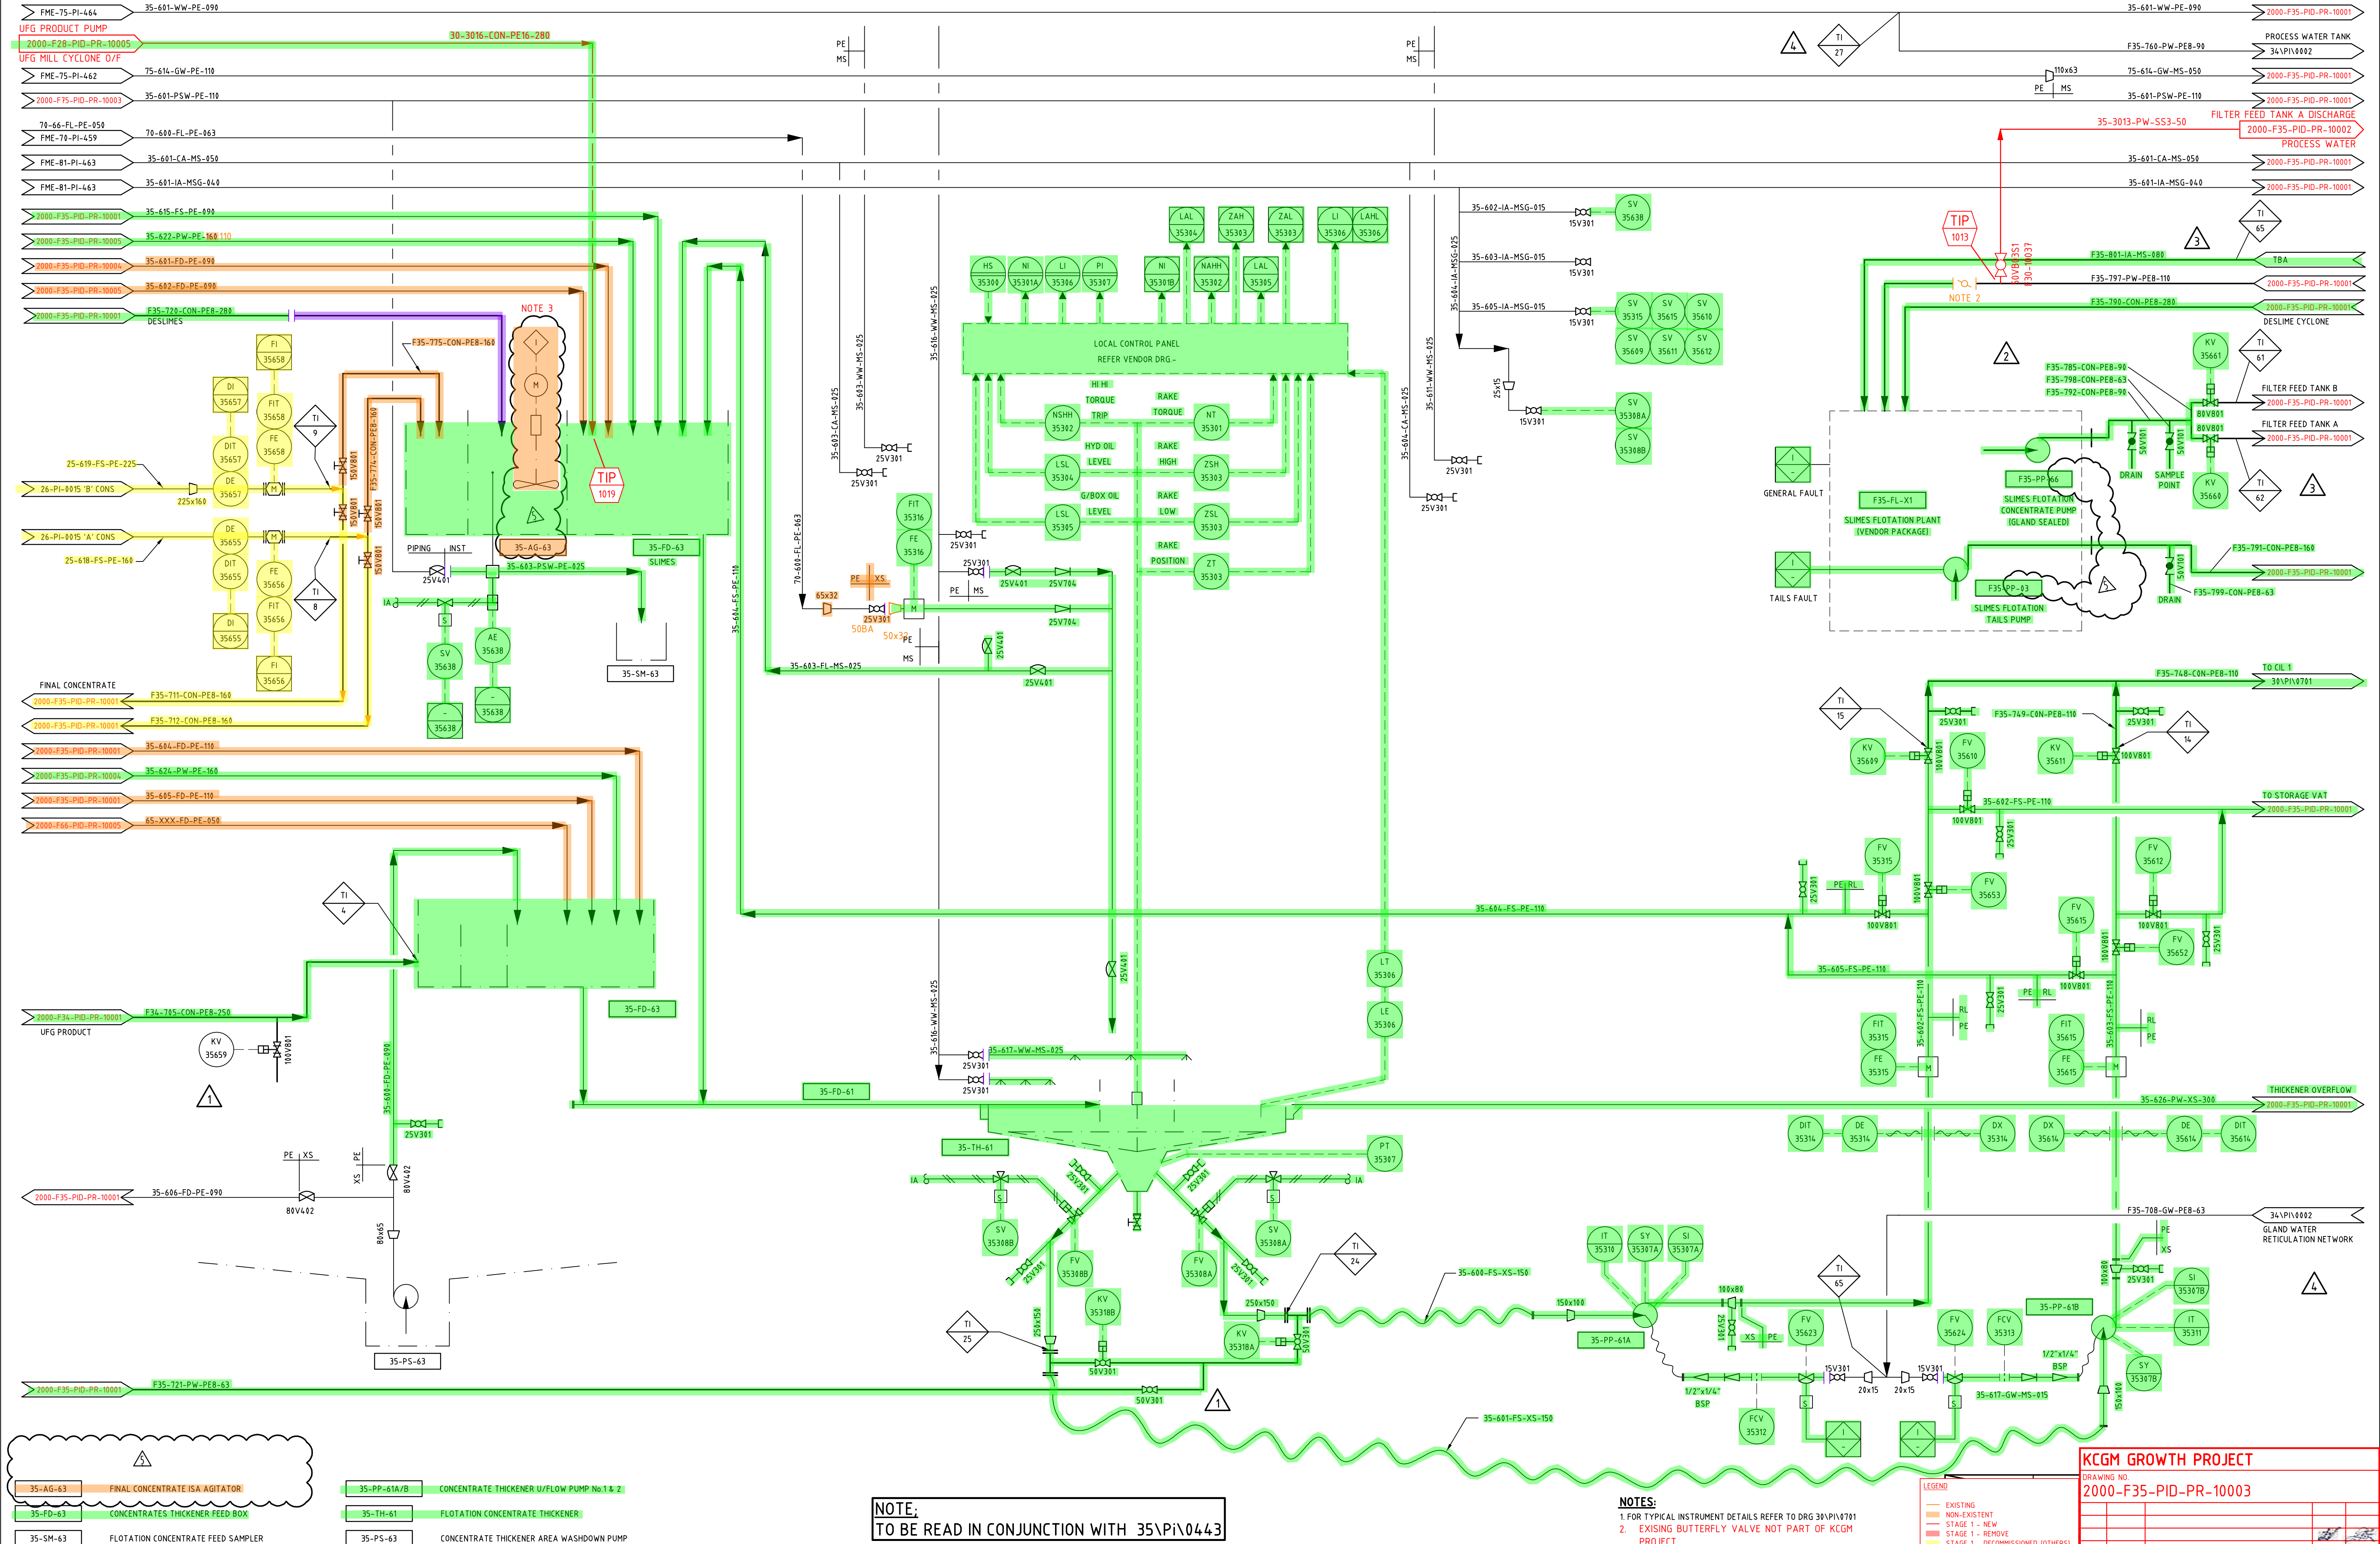

FIMISTON PLANT CONCENTRATES FILTRATION CONCENTRATE THICKENER AREA PIPING AND INSTRUMENTATION DIAGRAM				SIZE B1	DRAWING NUMBER 35\PI\0702	REV 5
KALGOORLIE CONSOLIDATED GOLD MINES PTY. LTD.				ABN 009 377 619 003		