
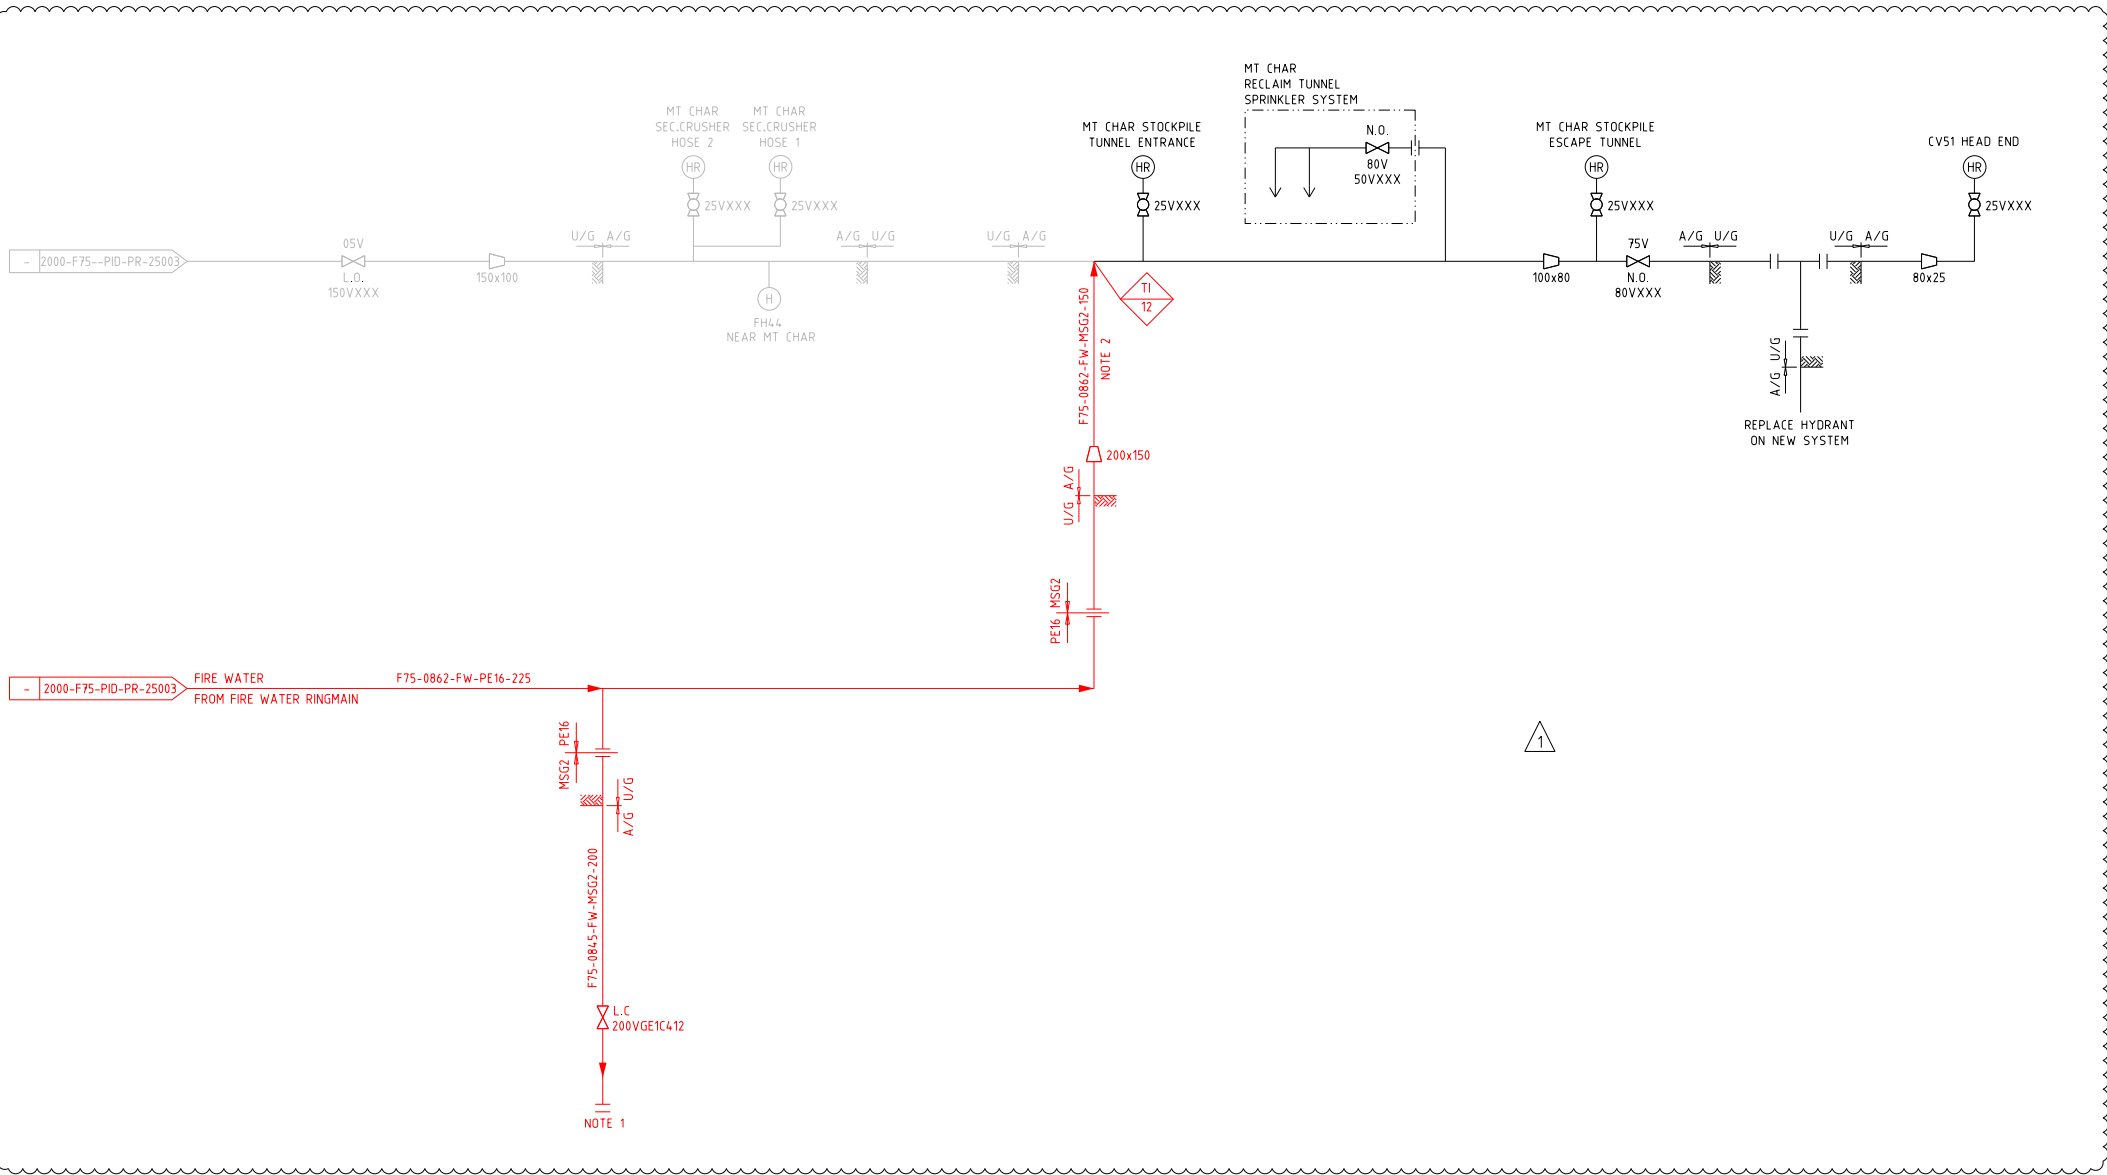


- NOTES:
- FUTURE STAGE 1 HIGH PRESSURE FIRE WATER TIE IN TO BACKFEED LEGACY SYSTEM.
 - BURIED EXISTING FIREWATER LINE TO BE UNCOVERED AND CAPPED USING BUTT WELDED MOULDED END CAP FITTING.

- LEGENDS:
- EXISTING
 - EXISTING TO BE MADE REDUNDANT DURING STAGE 1
 - NEW
 - FUTURE

 

APPROVED FOR
CONSTRUCTION

										 NORTHERN STAR		 DRA PACIFIC (PTY) LIMITED Level 8/256 Adelaide Terrace, Perth WA 6000 Tel: (08) 6163 5900 Level 4/145 Eagle Street, Brisbane Qld 4000 Tel: (07) 3236 4157		DRAWN	V. UNNY	12 MAY 2023	PROJECT KCGM GROWTH PROJECT – ENABLING WORKS				
														CHECKED	J. THOMPSON	12 MAY 2023	TITLE FIRE WATER DISTRIBUTION TO MT CHARLOTTE STOCKPILE AREA AREA 075 WATER SERVICES PIPING & INSTRUMENTATION DIAGRAM				
														DESIGNED	J. THOMPSON	12 MAY 2023					
														TECH APP	T. HAMMORF	12 MAY 2023					
														PROJ APP	T. HAMMORF	12 MAY 2023					
														CLIENT APP							
REFERENCES				DWG No		REV	DATE	REVISION		DRN	CHK	TECH APP	PROJ APP	A1		SCALE	NTS	DRG No.	2000-F75-PID-PR-25004	REV	1