


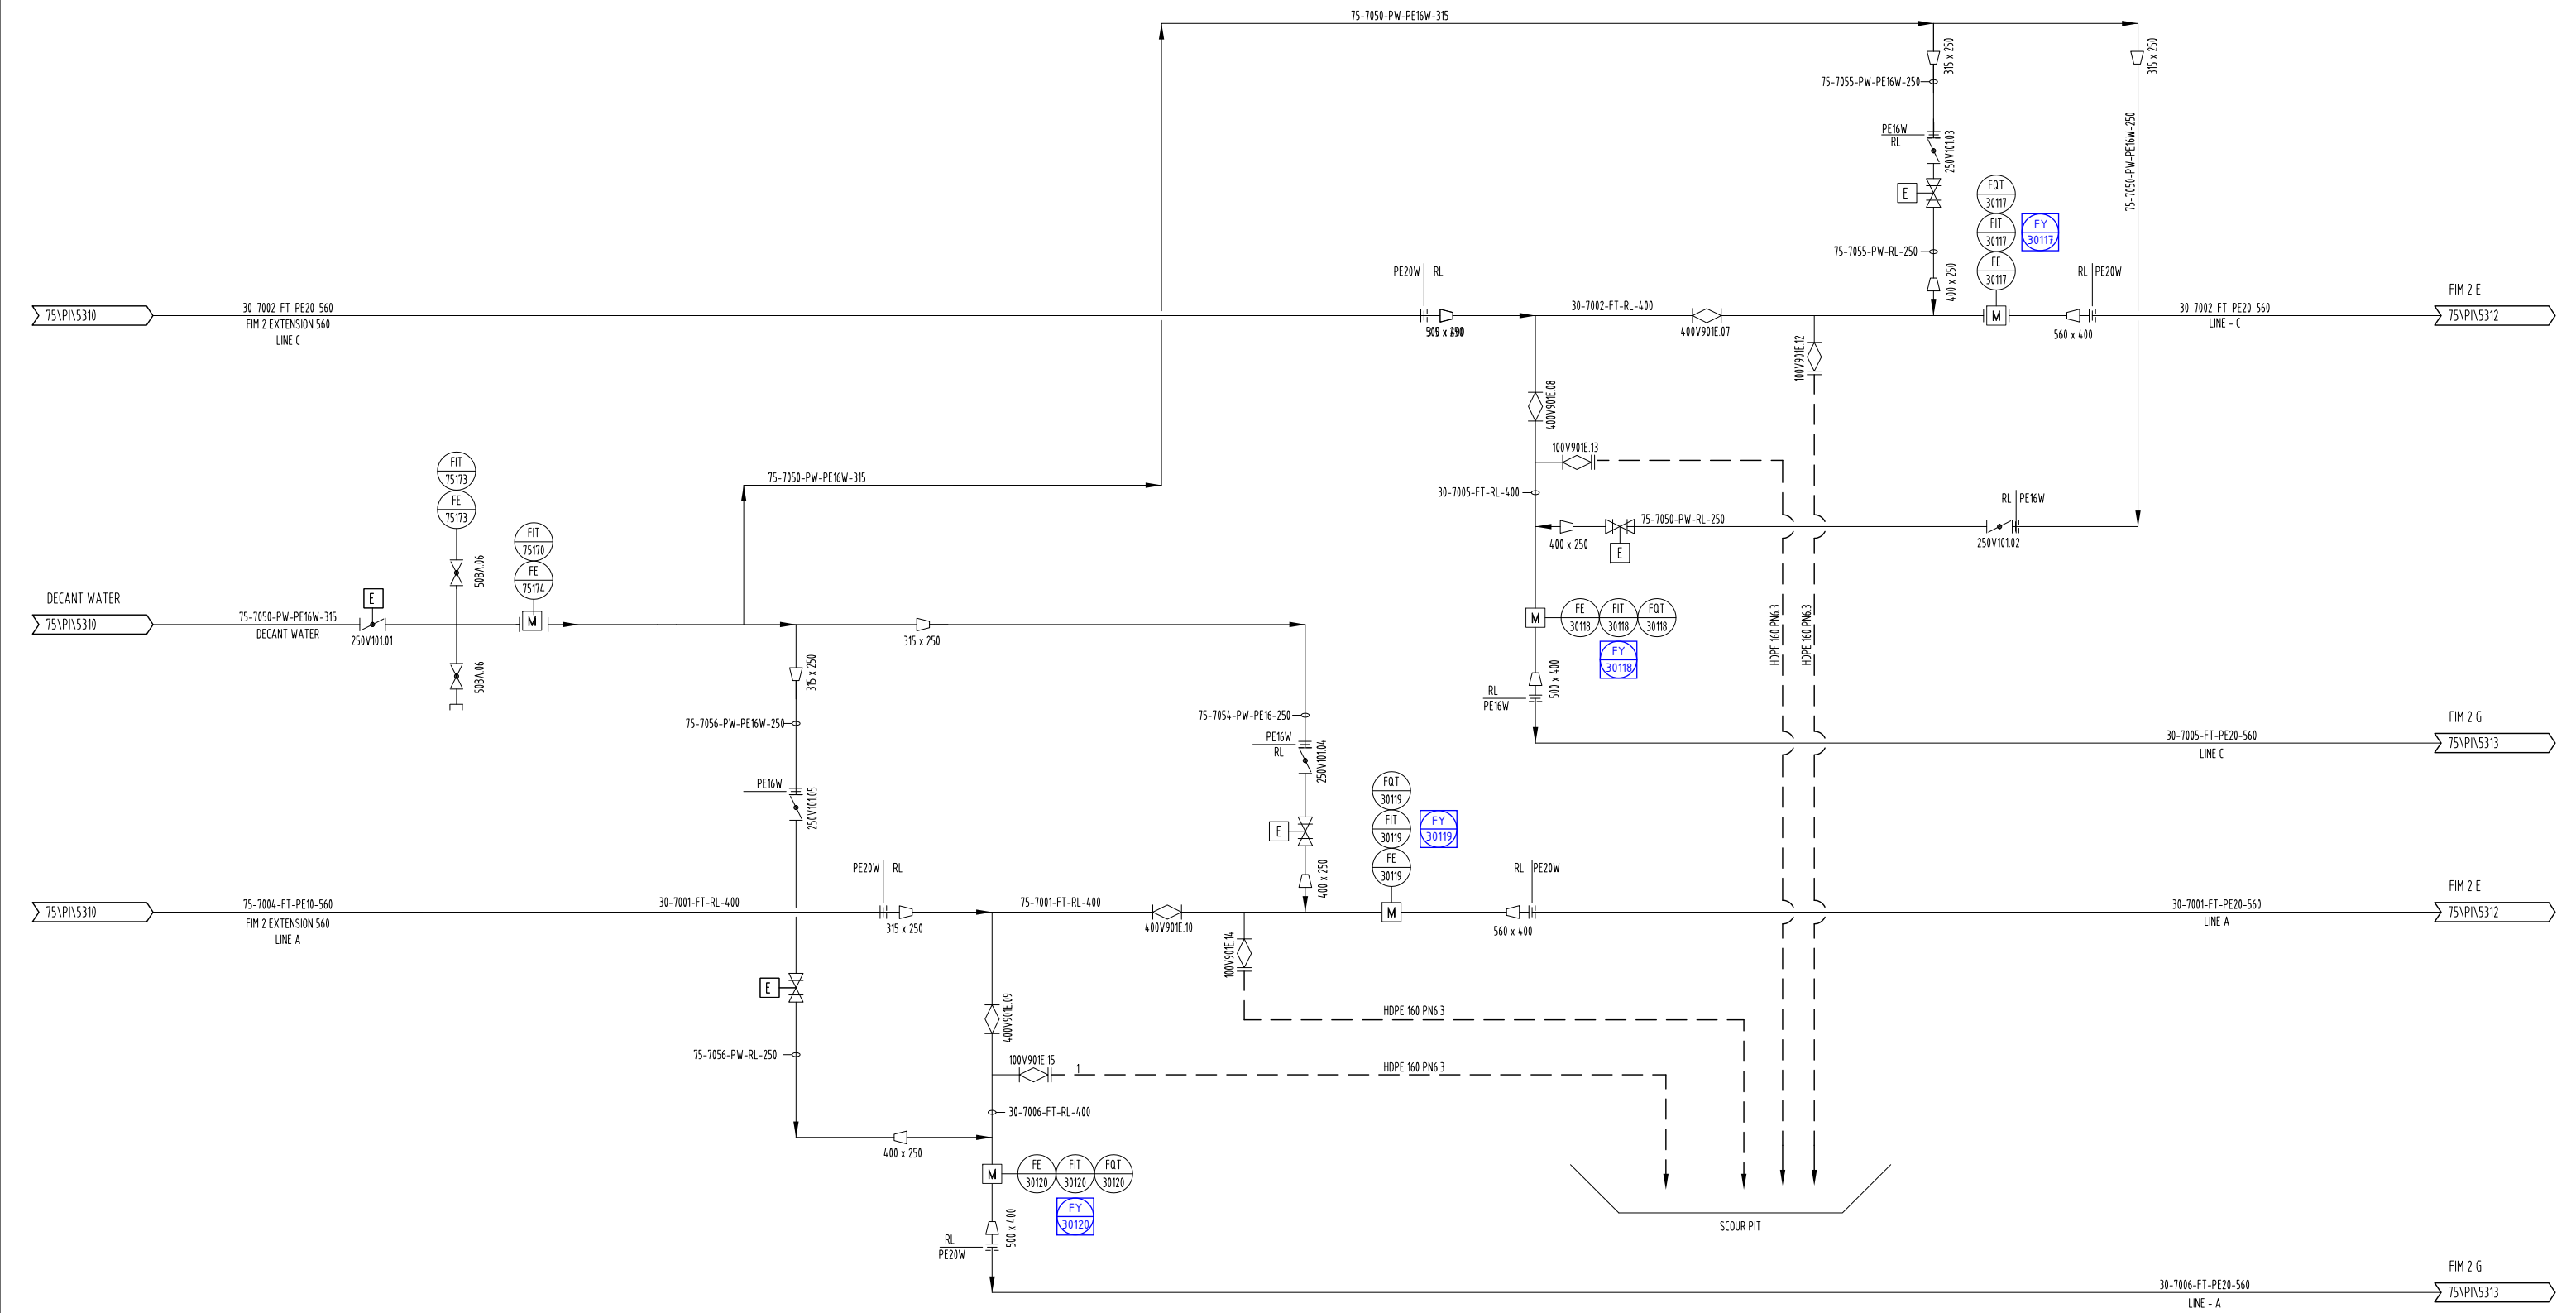

VALVE STATION No.3

LEGEND

EXISTING

NEW

KCGM GROWTH PROJECT				
DRAWING NO.				
2000-F75-PID-PR-40026				
0	05DEC24	APPROVED FOR CONSTRUCTION	CS	TvB
REV	DATE	DESCRIPTION	CHECK	TECH APP

LEGEND:

- EXISTING
- NEW
- FUTURE
- DECOMMISSIONED
- DECOMMISSIONED

 WILSHAW		+61 8 9479 0800 wilshaw.com.au	
WILSHAW DWG No.	REV	JOB No	7117

[illegible]