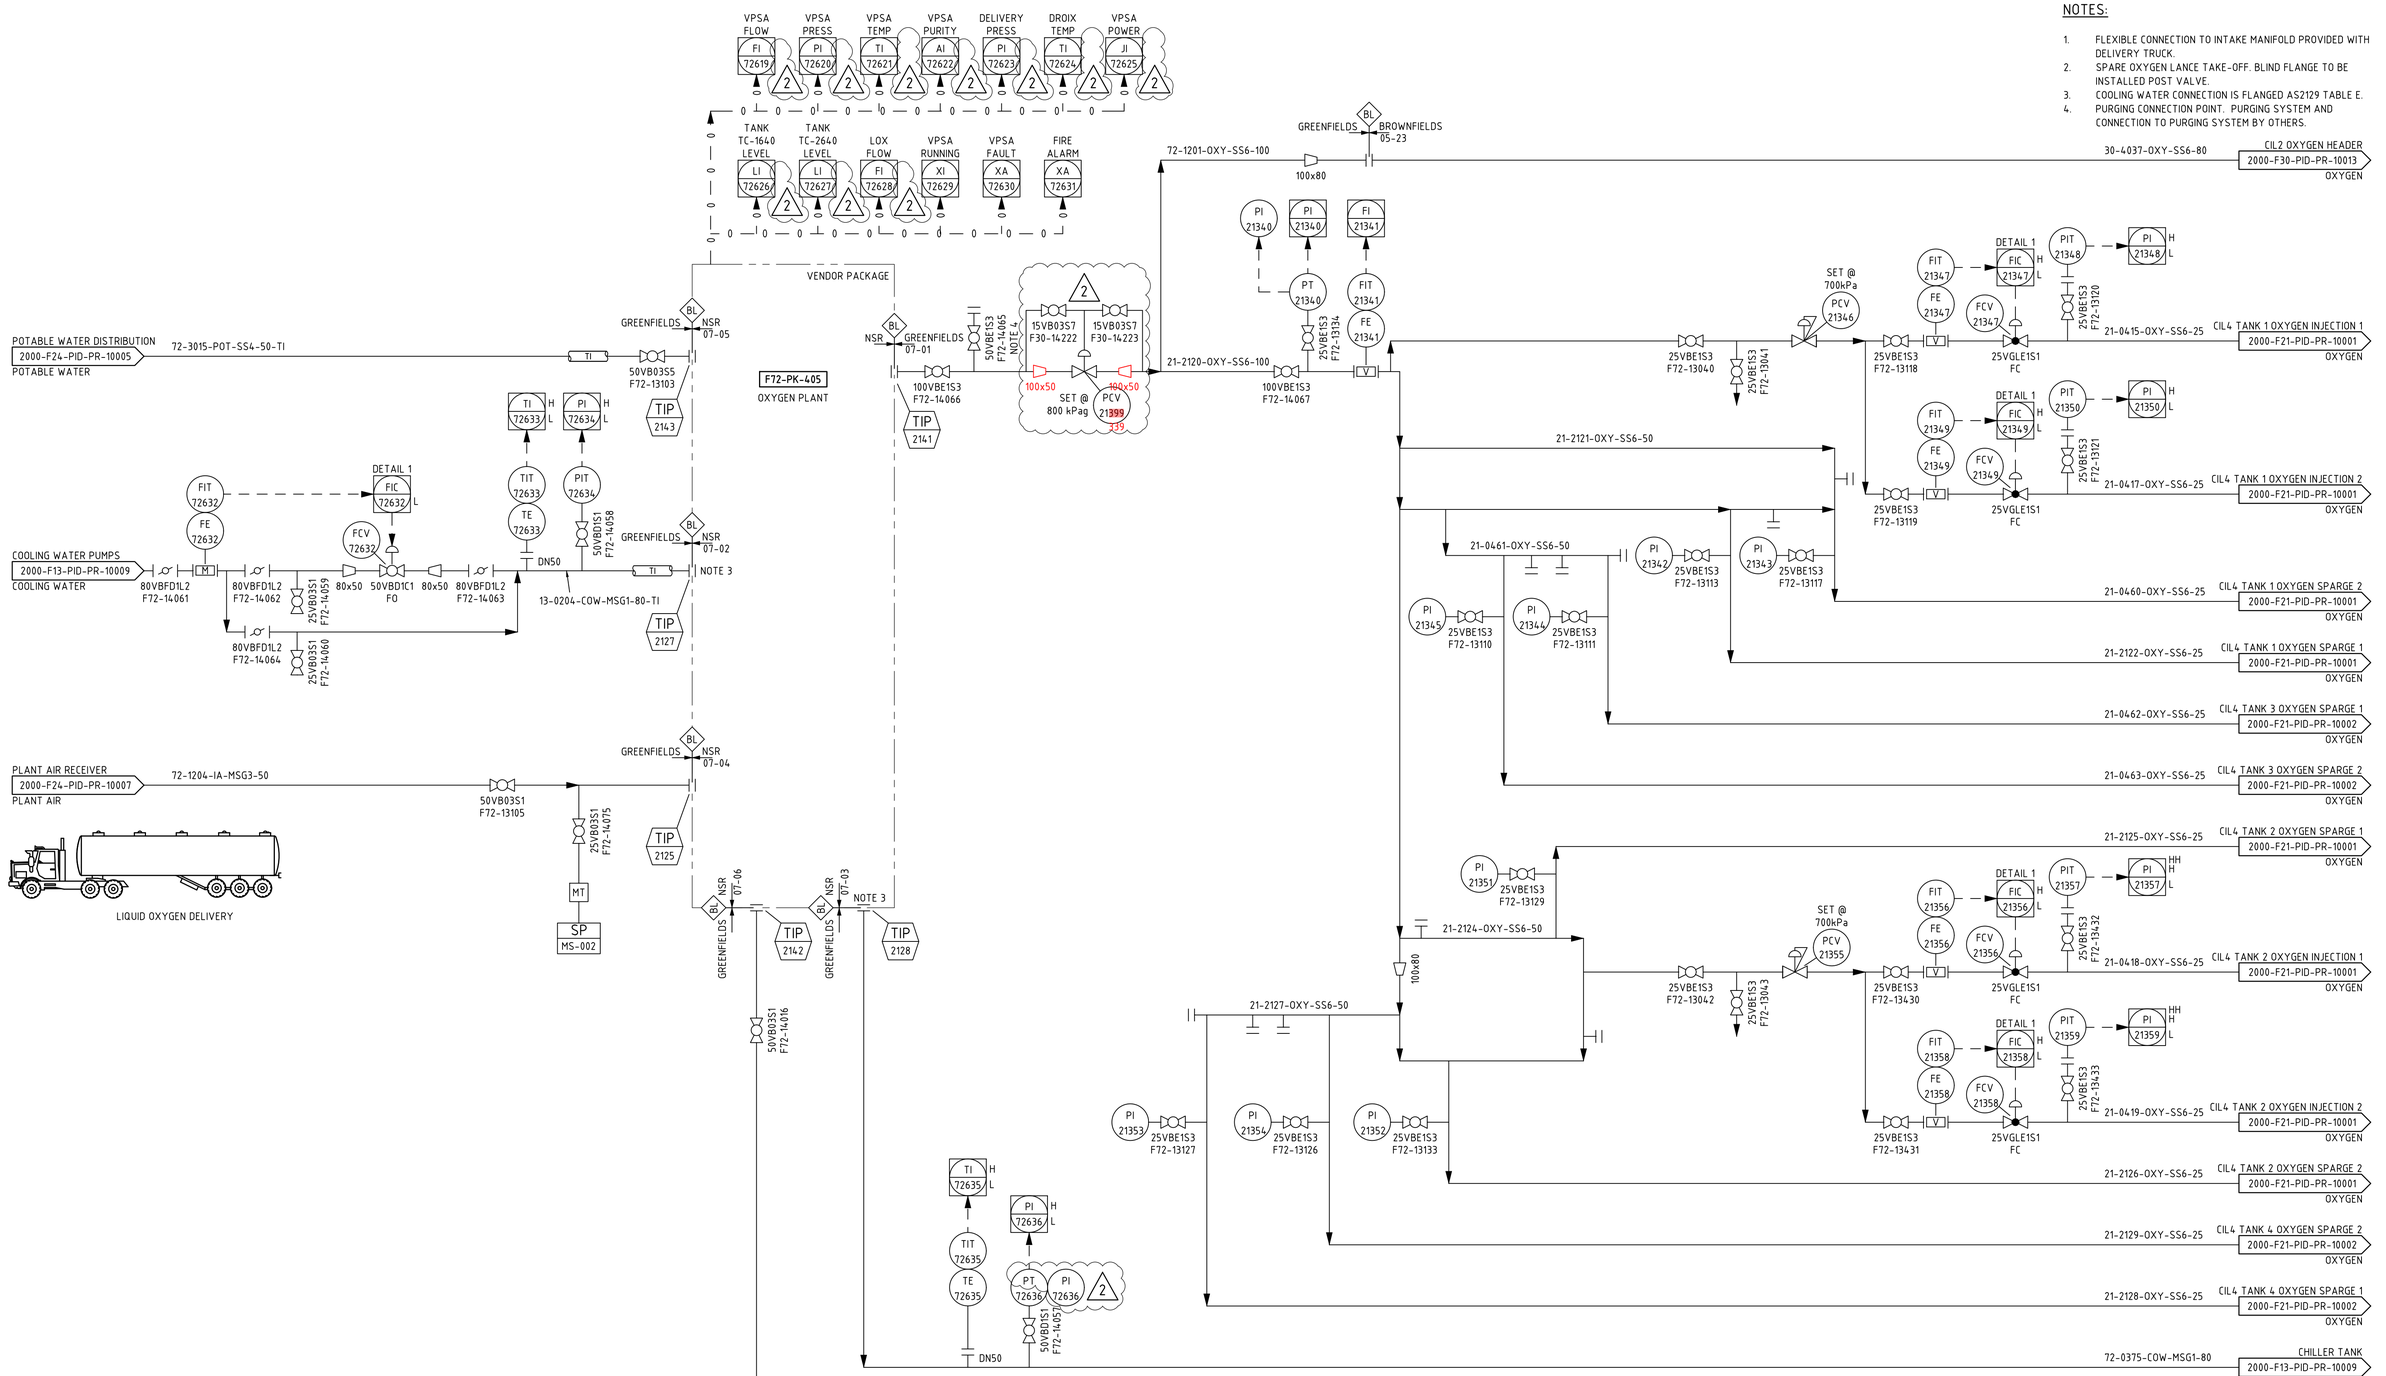


NOTES:

1. FLEXIBLE CONNECTION TO INTAKE MANIFOLD PROVIDED WITH DELIVERY TRUCK.
2. SPARE OXYGEN LANCE TAKE-OFF. BLIND FLANGE TO BE INSTALLED POST VALVE.
3. COOLING WATER CONNECTION IS FLANGED AS2129 TABLE E.
4. PURGING CONNECTION POINT. PURGING SYSTEM AND CONNECTION TO PURGING SYSTEM BY OTHERS.

DRG No.	REFERENCES	REV	DATE	DESCRIPTION	DRAW	CHECK	DESIGN	TECH APP	PROJ APP
2000-F00-PID-PR-10007	LEGEND SHEET 7 - PIPING AND INSTRUMENTATION DIAGRAM								
2000-F00-PID-PR-10006	LEGEND SHEET 6 - PIPING AND INSTRUMENTATION DIAGRAM								
2000-F00-PID-PR-10005	LEGEND SHEET 5 - PIPING AND INSTRUMENTATION DIAGRAM								
2000-F00-PID-PR-10004	LEGEND SHEET 4 - PIPING AND INSTRUMENTATION DIAGRAM				AH	MM	JBe	DA	DM
2000-F00-PID-PR-10003	LEGEND SHEET 3 - PIPING AND INSTRUMENTATION DIAGRAM	2	12SEP25	GENERAL REVISIONS AS NOTED	AH	MM	JBe	DA	DM
2000-F00-PID-PR-10002	LEGEND SHEET 2 - PIPING AND INSTRUMENTATION DIAGRAM	1	08JUL25	INSTRUMENT TAG SYMBOLS AND GENERAL REVISIONS ADDED	AH	JB	JBe	DA	DM
2000-F00-PID-PR-10001	LEGEND SHEET 1 - PIPING AND INSTRUMENTATION DIAGRAM	0	10JUN25	APPROVED FOR CONSTRUCTION	AH	JA	JBe	DA	DM

NORTHERN STAR RESOURCES LIMITED

PRIMERO
primero.com.au | DESIGN | CONSTRUCT | OPERATE

PRIMERO PROJECT NUMBER: 23517

INFORMATION AND REPRESENTATIONS ON THIS DRAWING ARE THE INTELLECTUAL PROPERTY OF PRIMERO UNLESS SPECIFICALLY IDENTIFIED OTHERWISE. ALL RIGHTS INCLUDING USE RESERVED

PROJECT: NORTHERN STAR RESOURCES LTD
KCGM GROWTH PROJECT

TITLE: REAGENTS MIXING & STORAGE
REAGENTS - OXYGEN
PIPING AND INSTRUMENTATION DIAGRAM

SHEET	SCALE	DRG No.	REVISION
A1	NTS	2000-F72-PID-PR-10011	2

O:\CAD PROJECTS\235 NORTHERN STAR RESOURCES LTD\23517 KCGM GROWTH PROJECT\03 DELIVERABLES\PRI\DISSUED\12.09.25 - SIGNING\NATIVES\2000-F72-PID-PR-10011_2.DWG 09SEP25 3:28PM ANNE.HOYNE