


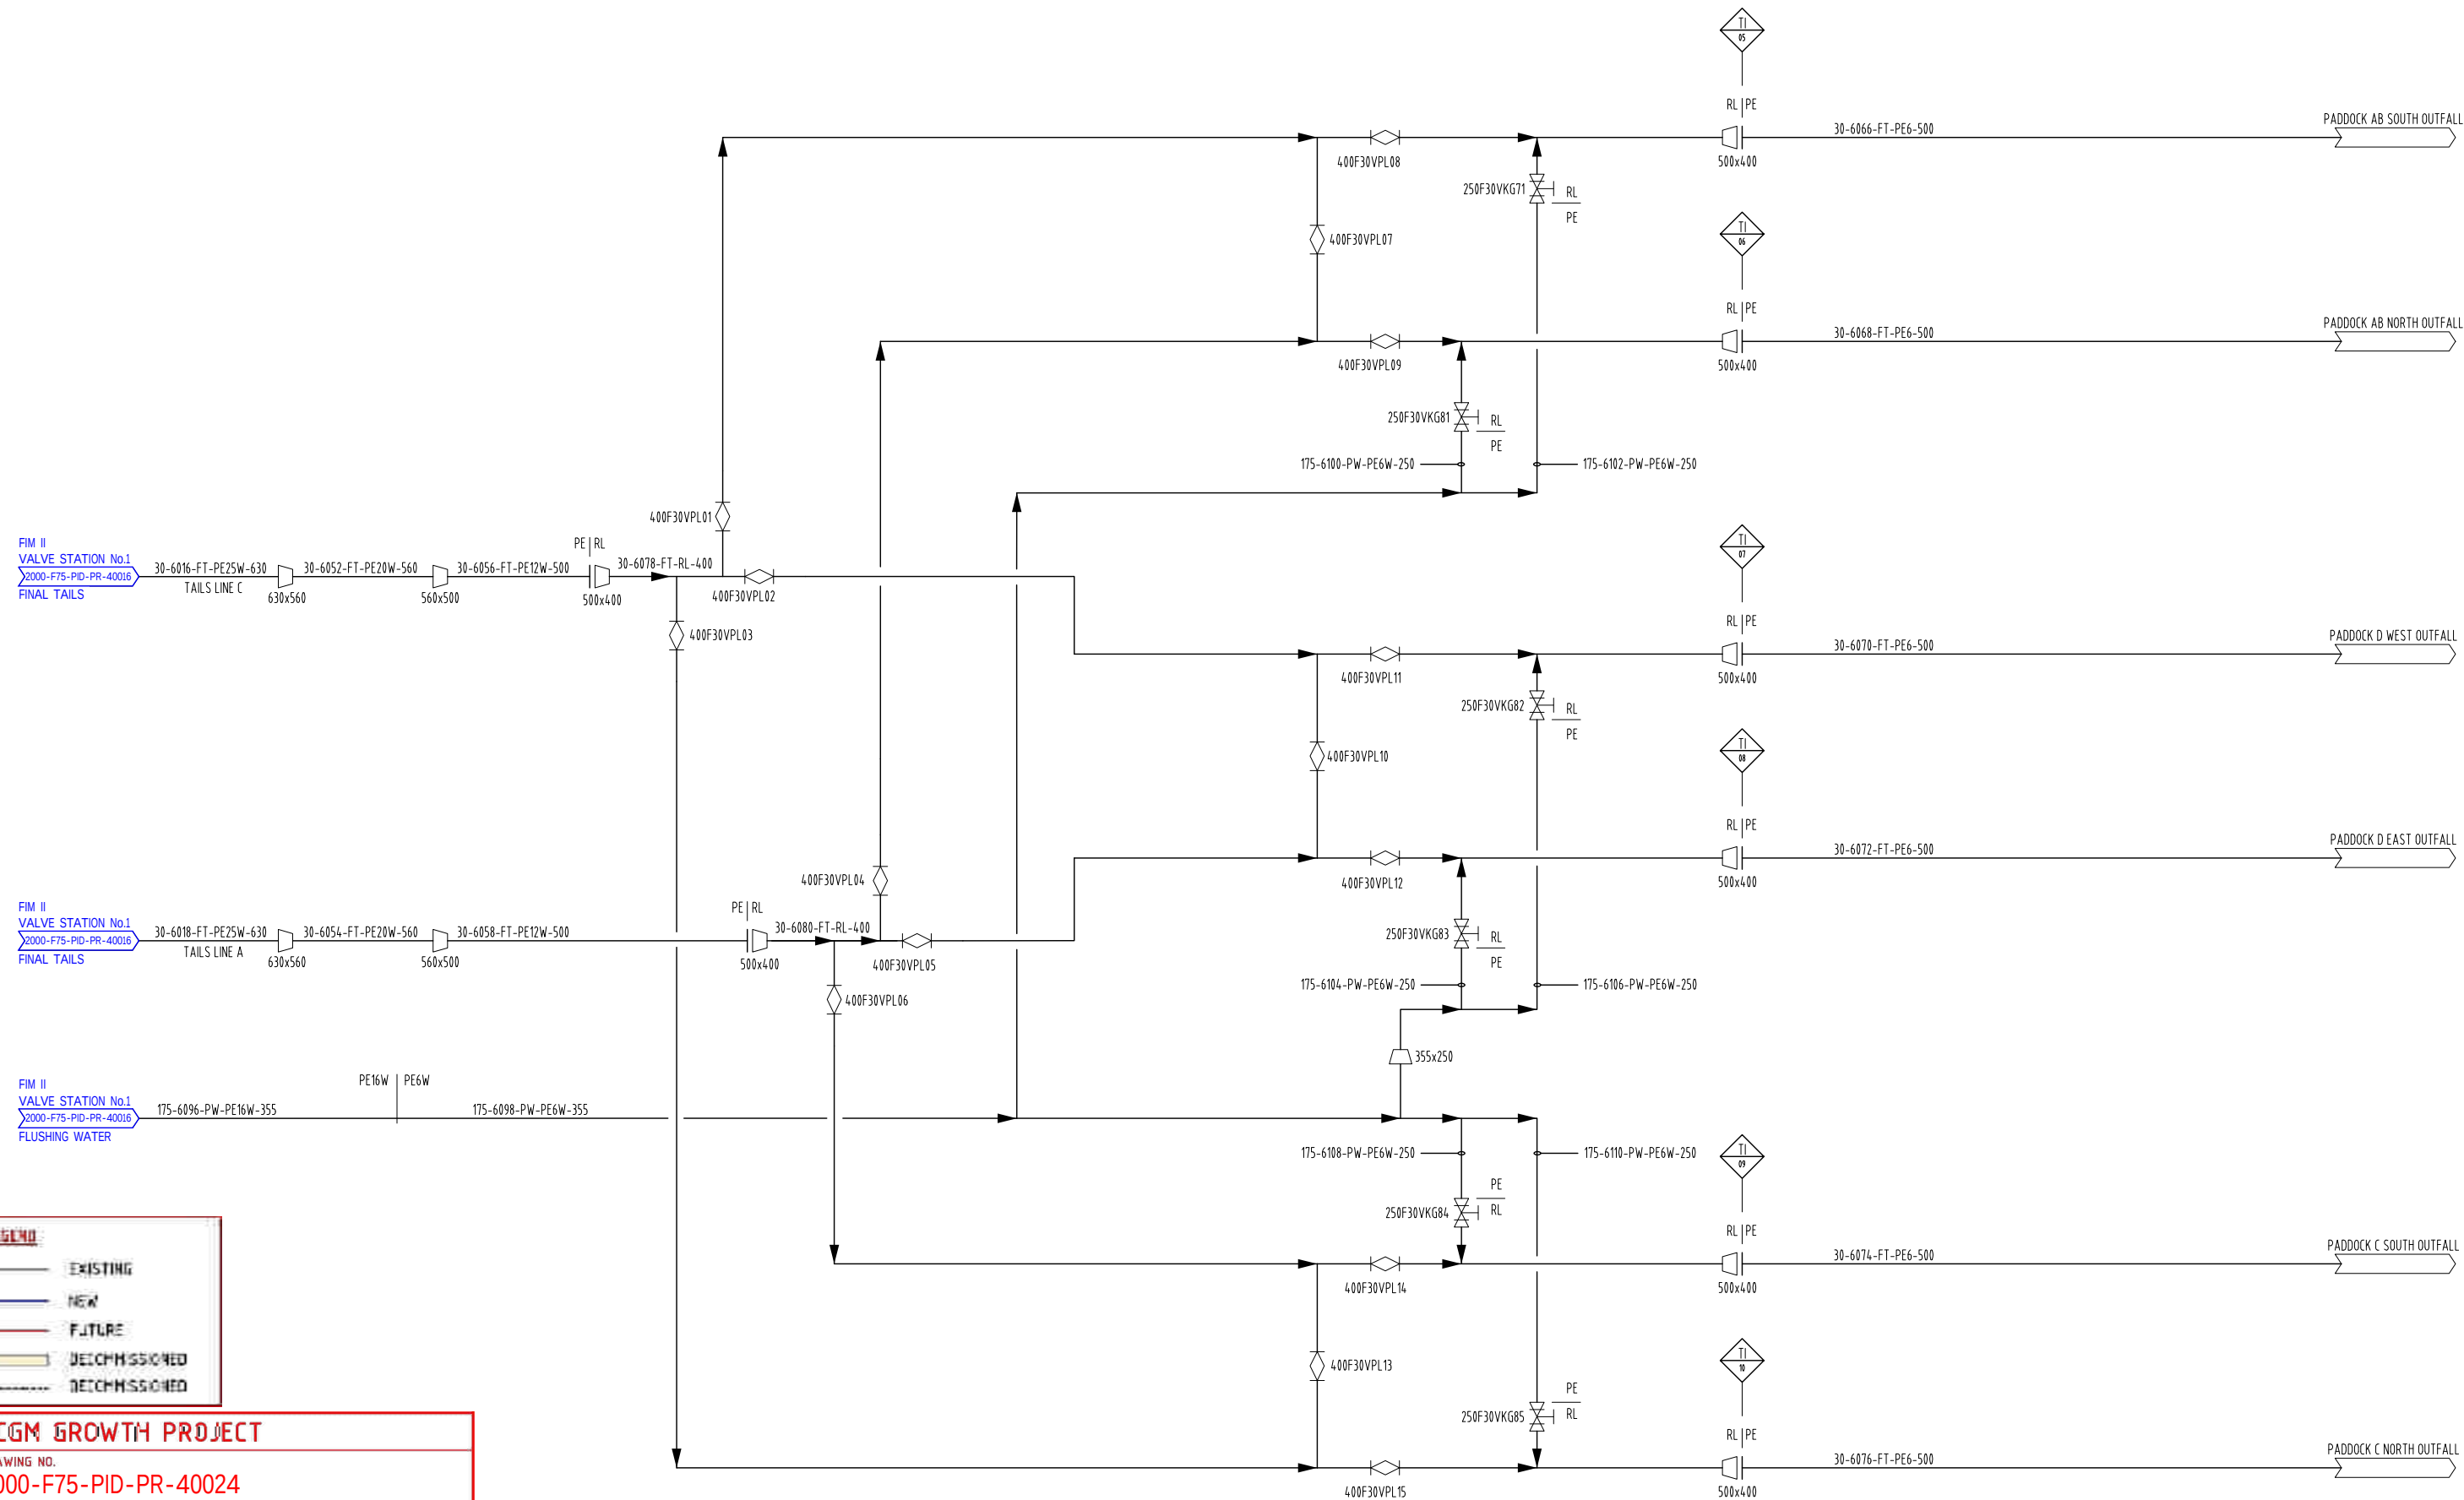

LEGEND

- EXISTING
- NEW
- FUTURE
- DECOMMISSIONED
- DECOMMISSIONED

KCGM GROWTH PROJECT

DRAWING NO.
2000-F75-PID-PR-40024

[illegible][illegible]