


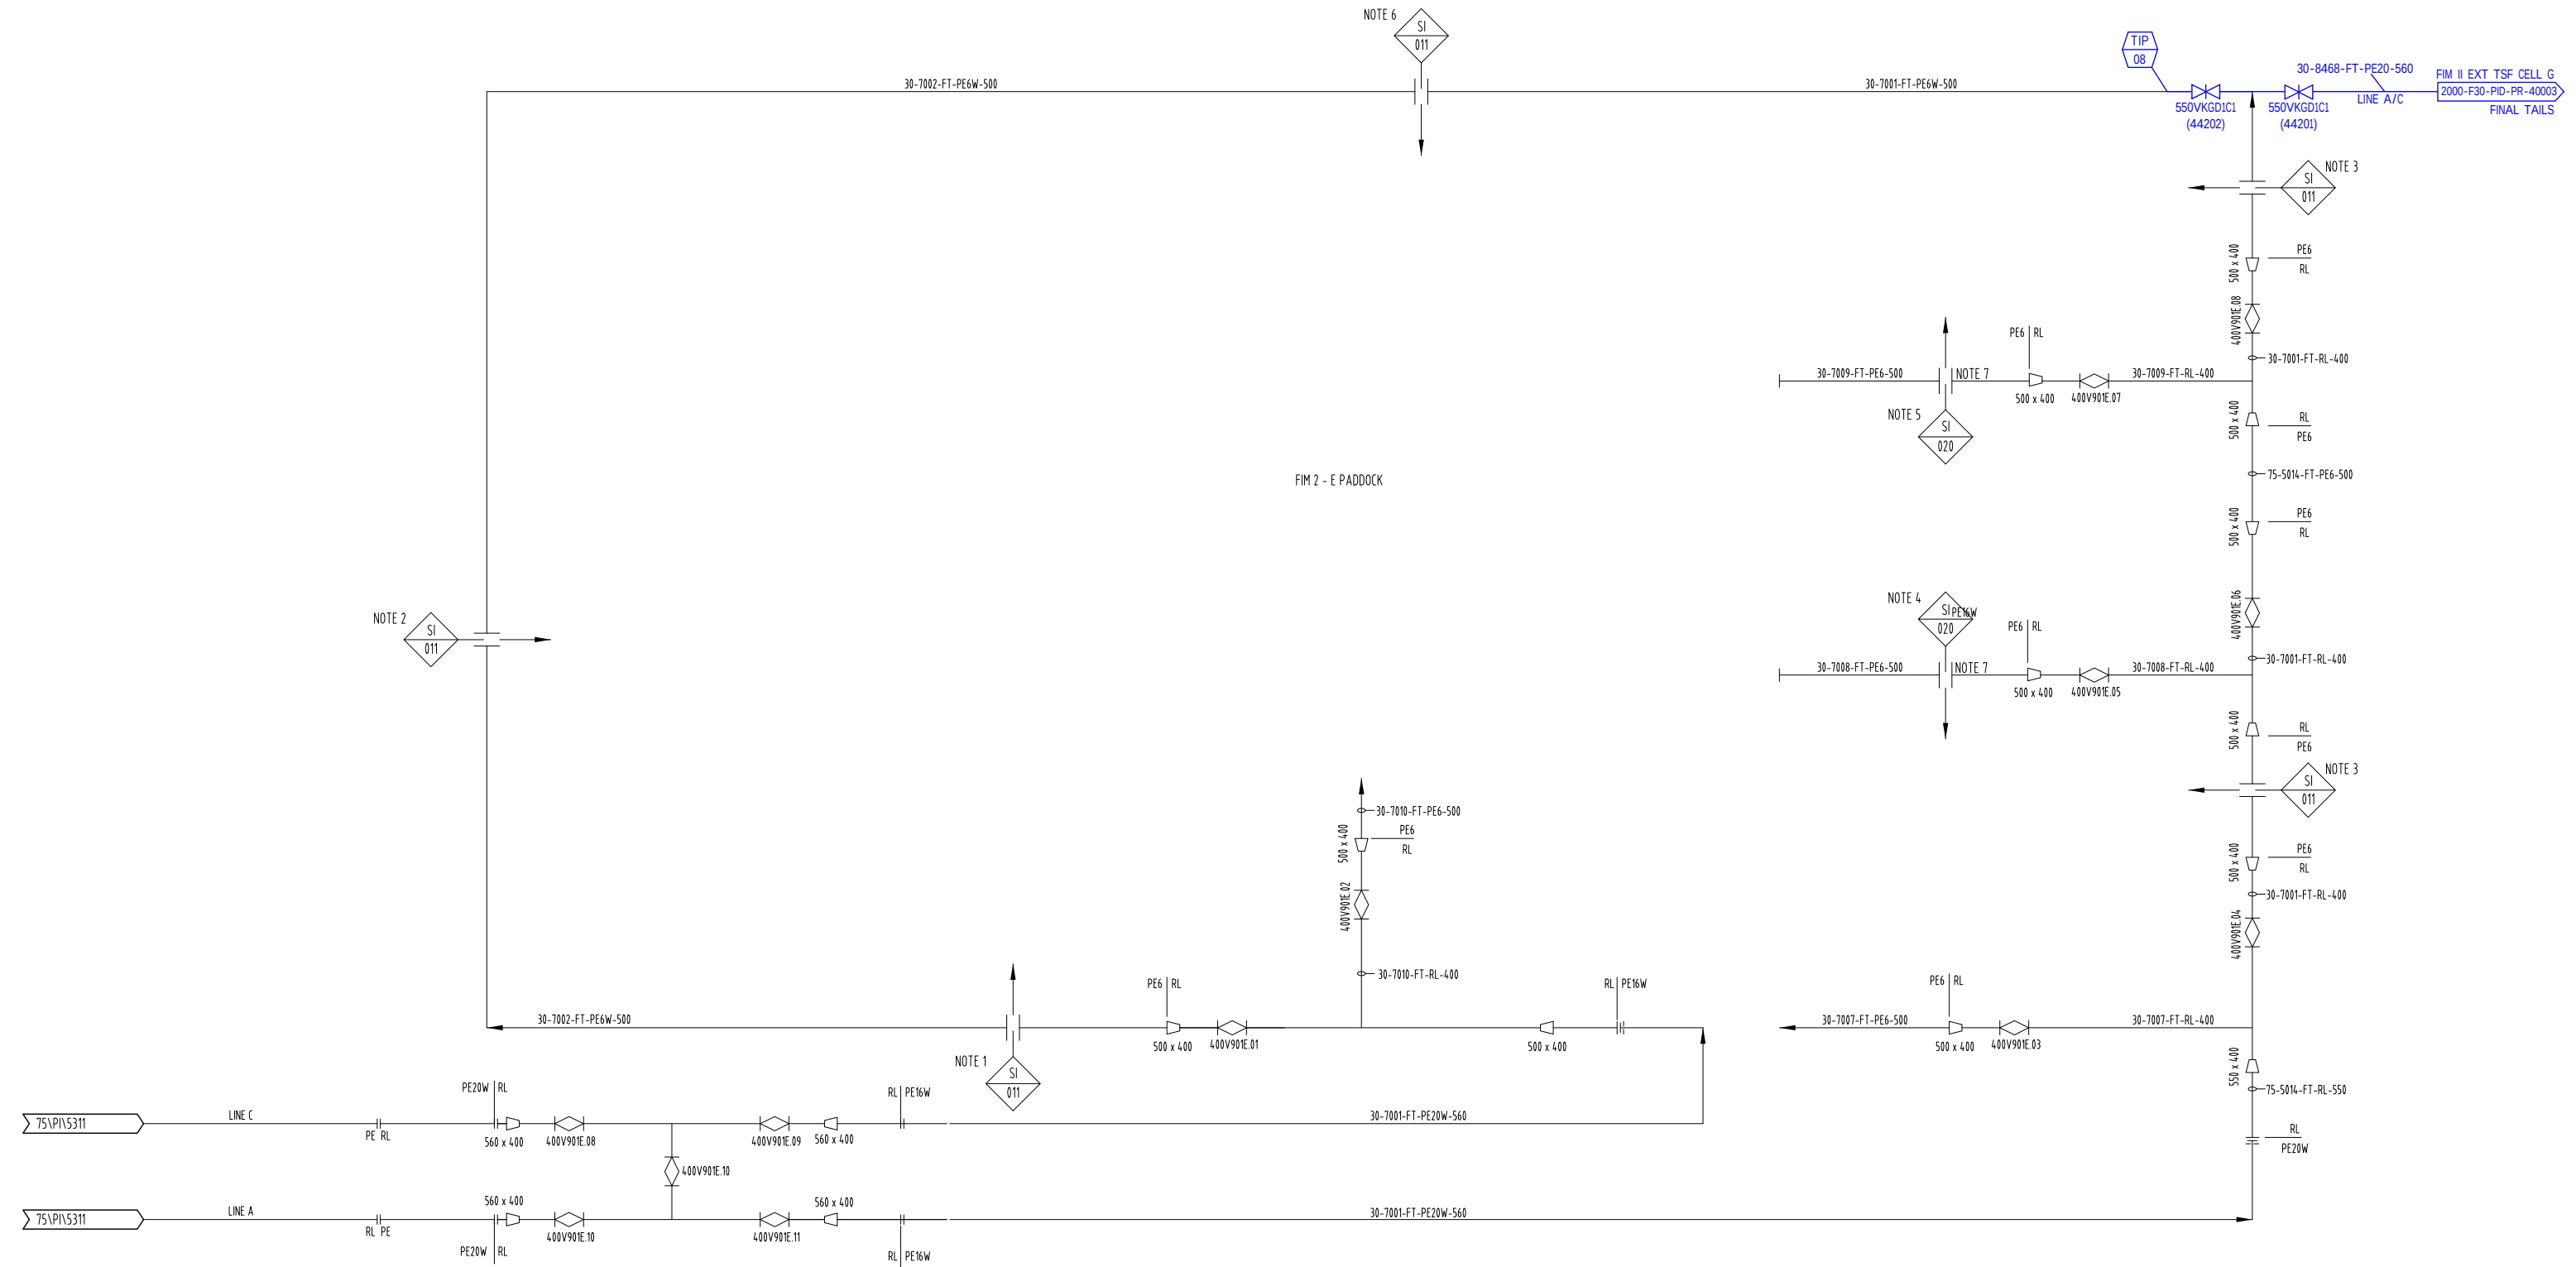

KCGM GROWTH PROJECT

DRAWING NO.
2000-F75-PID-PR-40027

[illegible]

LEGEND

- EXISTING
- NEW
- FUTURE
- DECOMMISSIONED
- DECOMMISSIONED

- NOTES

1. SPIGOTS SPACED AT 4.0m CENTRES DISCHARGING ON THE SOUTHERN WALL
2. SPIGOTS SPACED AT 4.0m CENTRES DISCHARGING ON THE WESTERN WALL
3. SPIGOTS SPACED AT 4.0m CENTRES DISCHARGING ON THE WESTERN SIDE OF THE CENTRAL WALL
4. OUTLETS SPACED AT 15m CENTRES DISCHARGING ON THE SOUTHERN SIDE OF THE CAUSEWAY
5. OUTLETS SPACED AT 15m CENTRES DISCHARGING ON THE NORTHERN SIDE OF THE CAUSEWAY
6. SPIGOTS SPACED AT 4.0m CENTRES DISCHARGING ON THE NORTHERN WALL
7. CAUSEWAY PIPING TO BE FLANGED EVERY 4.0m



+61 8 9479 0800
wilshaw.com.au

WILSHAW DWG No.	REV	JOB No 7117
-----------------	-----	-------------

FIMSTON PLANT WATER TREATMENT FIMSTON FIM 2 TSF EXTENSION P&I DIAGRAM - PADDOCK - E	SIZE	DRAWING NUMBER	REV
	A1	75/PI/5312	D

KALGOORLIE CONSOLIDATED GOLD MINES PTY. LTD.

ABN 009 377 619 003

[illegible]