


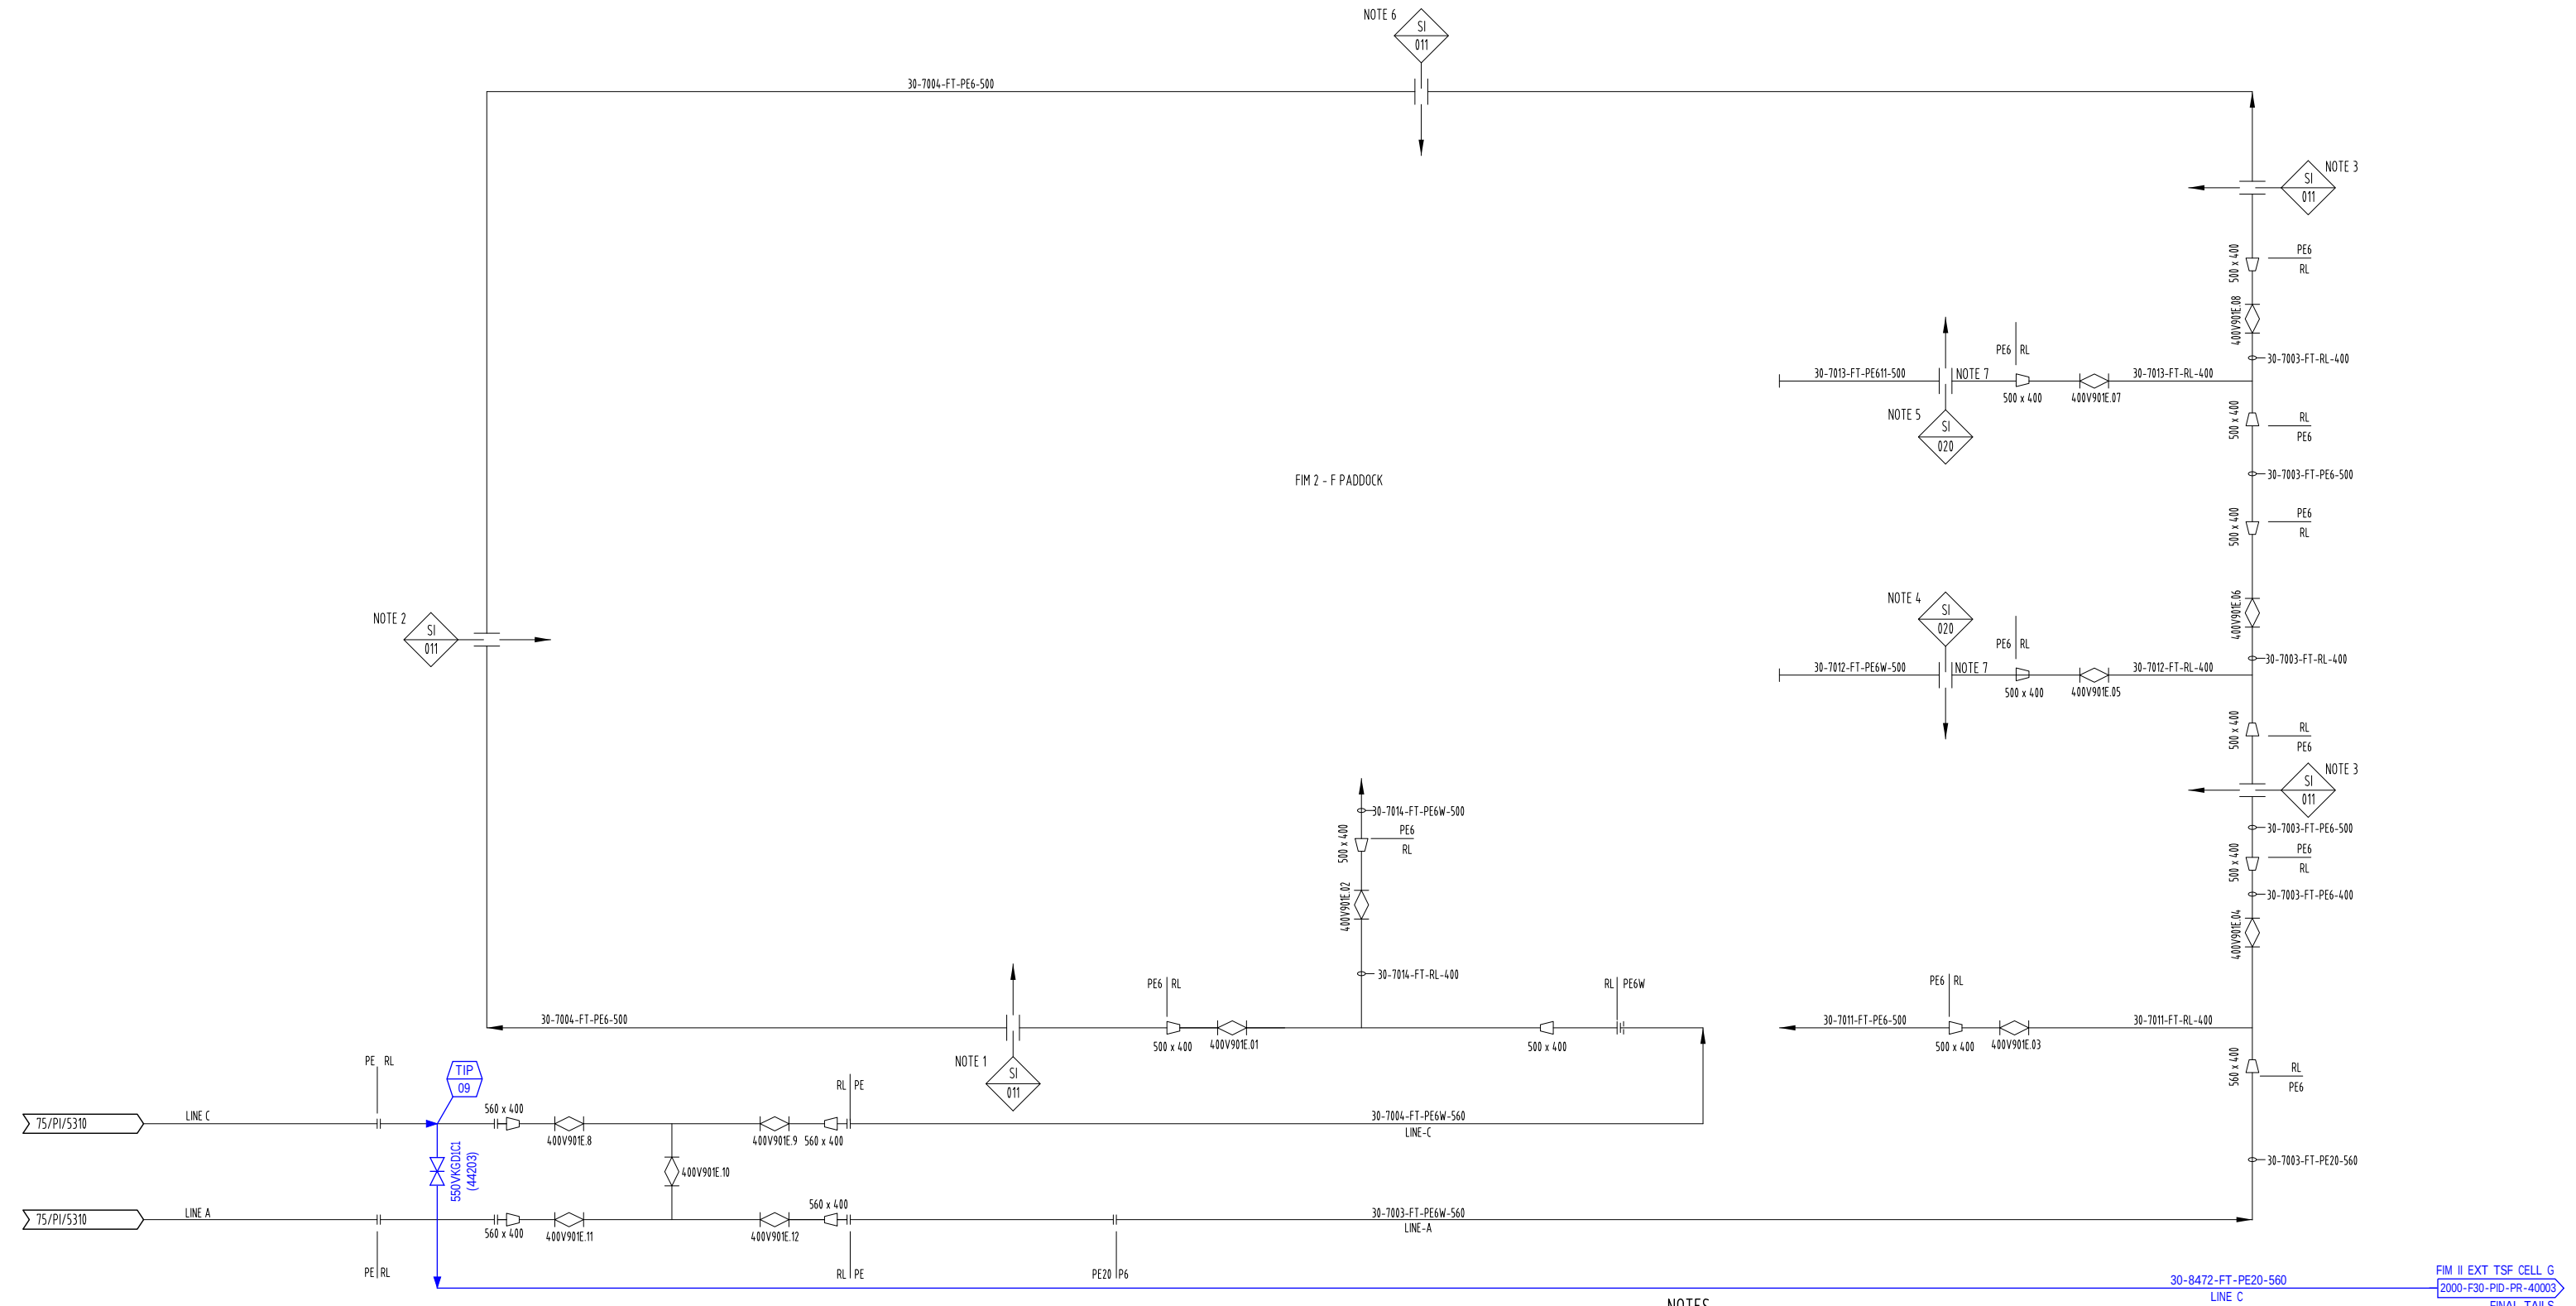

- ## NOTES
1. SPIGOTS SPACED AT 40m CENTRES DISCHARGING ON THE SOUTHERN WALL
 2. SPIGOTS SPACED AT 40m CENTRES DISCHARGING ON THE WESTERN WALL
 3. SPIGOTS SPACED AT 40m CENTRES DISCHARGING ON THE WESTERN SIDE OF THE CENTRAL WALL
 4. OUTLETS SPACED AT 15m CENTRES DISCHARGING ON THE SOUTHERN SIDE OF THE CAUSEWAY
 5. OUTLETS SPACED AT 15m CENTRES DISCHARGING ON THE NORTHERN SIDE OF THE CAUSEWAY
 6. SPIGOTS SPACED AT 40m CENTRES DISCHARGING ON THE NORTHERN WALL
 7. CAUSEWAY PIPING TO BE FLANGED EVERY 40m

KCGM GROWTH PROJECT					
DRAWING NO.					
2000-F75-PID-PR-40028					
0	05DEC24	APPROVED FOR CONSTRUCTION	CS	TVB	
REV	DATE	DESCRIPTION	CHECK	TECH APP	

LEGEND

— EXISTING

— NEW

— FUTURE

— DECOMMISSIONED

— DECOMMISSIONED

 WILSHAW		+61 8 9479 0800 wilshaw.com.au	
WILSHAW DWG No.	REV	JOB No	7117

[illegible]