


D:\CAD PROJECTS\235 NORTHERN STAR RESOURCES LTD\23517 KCGM GROWTH PROJECT\03 DELIVERABLES\PR\PID\2000-F72-PID-PR-10014 2.DWG 04SEP25 9:11AM ANNE HOYNE

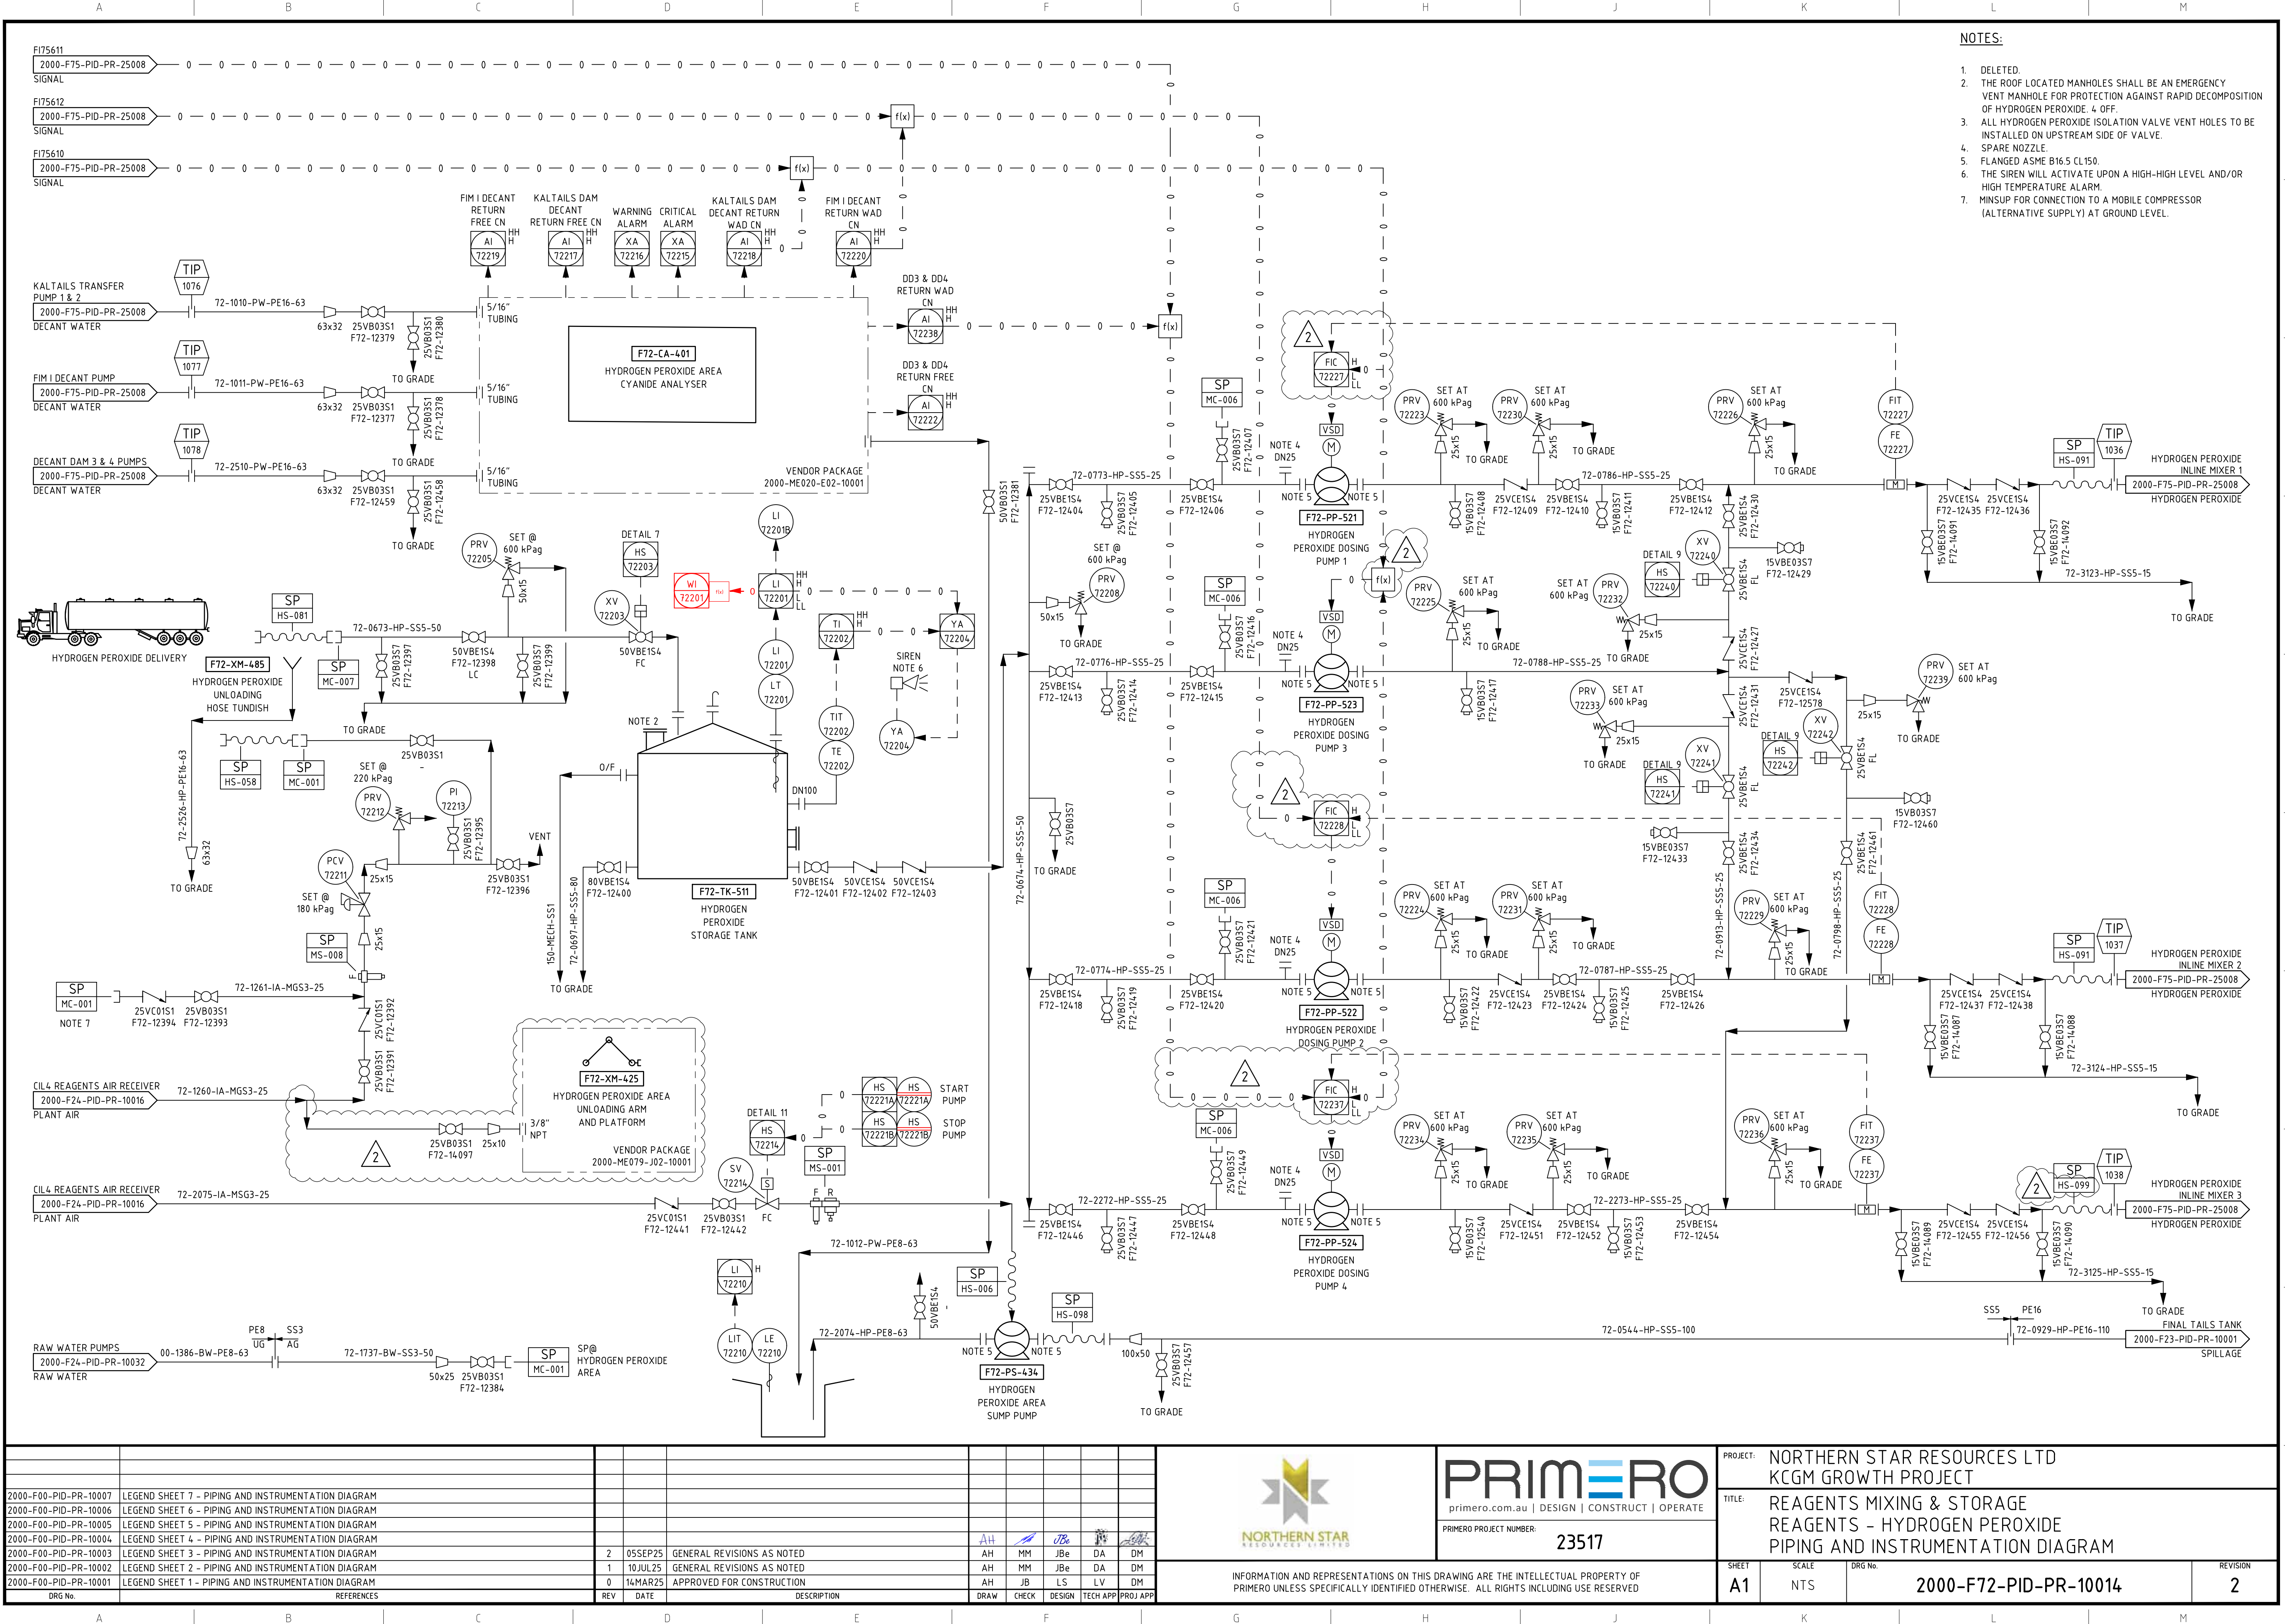

NOTES:

- DELETED.
- THE ROOF LOCATED MANHOLES SHALL BE AN EMERGENCY VENT MANHOLE FOR PROTECTION AGAINST RAPID DECOMPOSITION OF HYDROGEN PEROXIDE. 4 OFF.
- ALL HYDROGEN PEROXIDE ISOLATION VALVE VENT HOLES TO BE INSTALLED ON UPSTREAM SIDE OF VALVE.
- SPARE NOZZLE.
- FLANGED ASME B16.5 CL150.
- THE SIREN WILL ACTIVATE UPON A HIGH-HIGH LEVEL AND/OR HIGH TEMPERATURE ALARM.
- MINSUP FOR CONNECTION TO A MOBILE COMPRESSOR (ALTERNATIVE SUPPLY) AT GROUND LEVEL.