


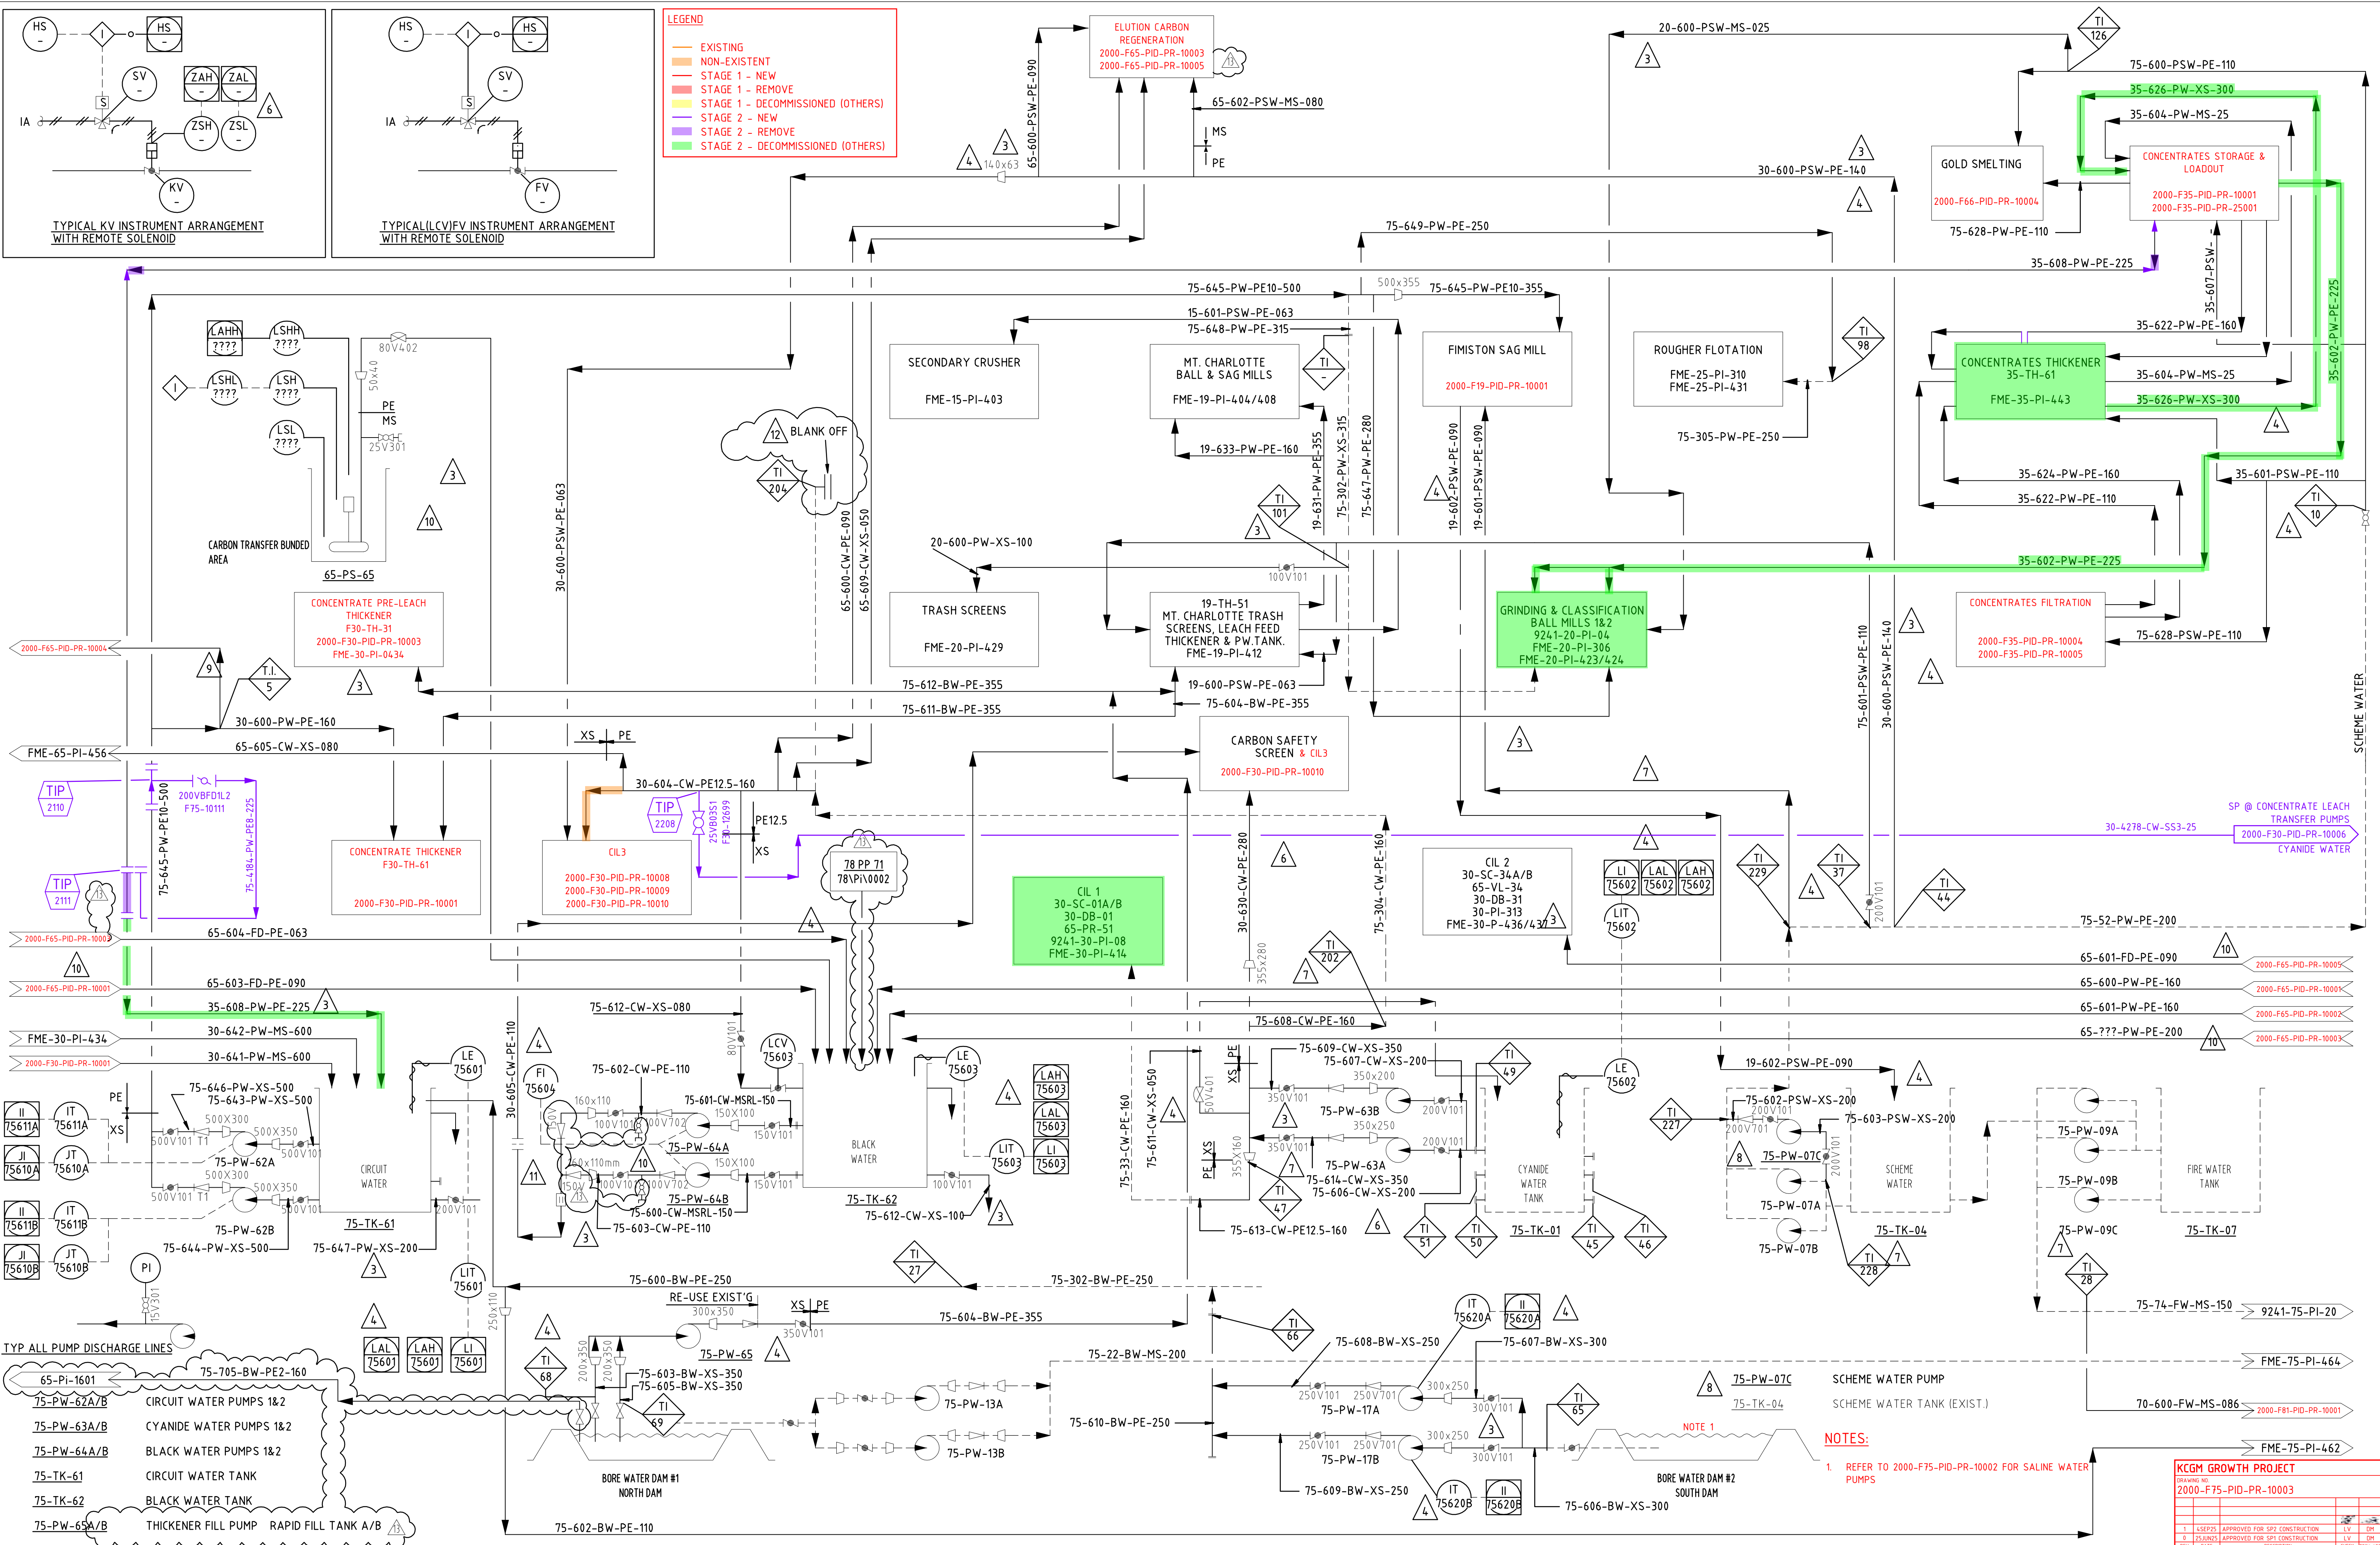

FME-00-SP-403 STANDARD EQUIPMENT SYMBOLS		COPYRIGHT ©		MINPROC ENGINEERS LIMITED A.C.N. 008 992 694 22, STIRLING HIGHWAY, NEDLANDS WA 6009 PHONE: (09) 341 4777		13 LW 01.04.2020 REV'D AS NOTED. VALVE & F/M ADDED		TR -		6 PR 8/5/95 REVISED AS NOTED		GT AH		PROJECT APPR.		BY DM		DATE 10/3/95				CLIENT		KALGOORLIE CONSOLIDATED GOLD MINES		SIZE		SCALE		N.T.S.	
FME-00-SP-404 ABBREVIATIONS & VALVE SYMBOLS		This drawing remains the property of MINPROC ENGINEERS LIMITED and may not be copied in any way without prior written approval from this company				12 JB 28/11/14 LINE 75-68-40-PEDS-40 REMOVED DMS 644		JB JB		5 PR 21/4/95 APPROVED FOR CONSTRUCTION F035		GT DT		DESIGN APPR.		DT		9/3/95				TITLE		FIMISTON EXPANSION 1994/95 PIPING & INSTRUMENT DIAGRAM WATER MANAGEMENT		REV. 01 2 3 4 5 6 7 8 9 10 11		DRAWING No.		FME-75-PI-0461	
FME-00-SP-408 INSTRUMENT STANDARDS						11 RH 29/9/11 ADDITION FLOW METER PS44 WHEN CONTROLS PUMPS STOPPED 44.3				4 PR 20/4/95 REVISED AS NOTED F-037		GT DT	