


D:\CAD PROJECTS\235 NORTHERN STAR RESOURCES LTD\23517 KCGM GROWTH PROJECT\03 DELIVERABLES\PR\PID\2000-F24-PID-PR-10004_1.DWG 11/01/25 10:57AM ANNE HOYNE

NOTES:

- PUMPS REQUIRING GLAND WATER THAT ARE WITHIN BROWNFIELDS SCOPE ARE TO TIE IN TO EXISTING GLAND WATER CIRCUIT.
- ALL GLAND WATER CONNECTIONS TO PUMPS TO BE AS PER TYPICAL GLAND WATER DETAIL. REFER TO 2000-F24-PID-PR-10034 AND 2000-F24-PID-PR-10035 FOR DETAILS.

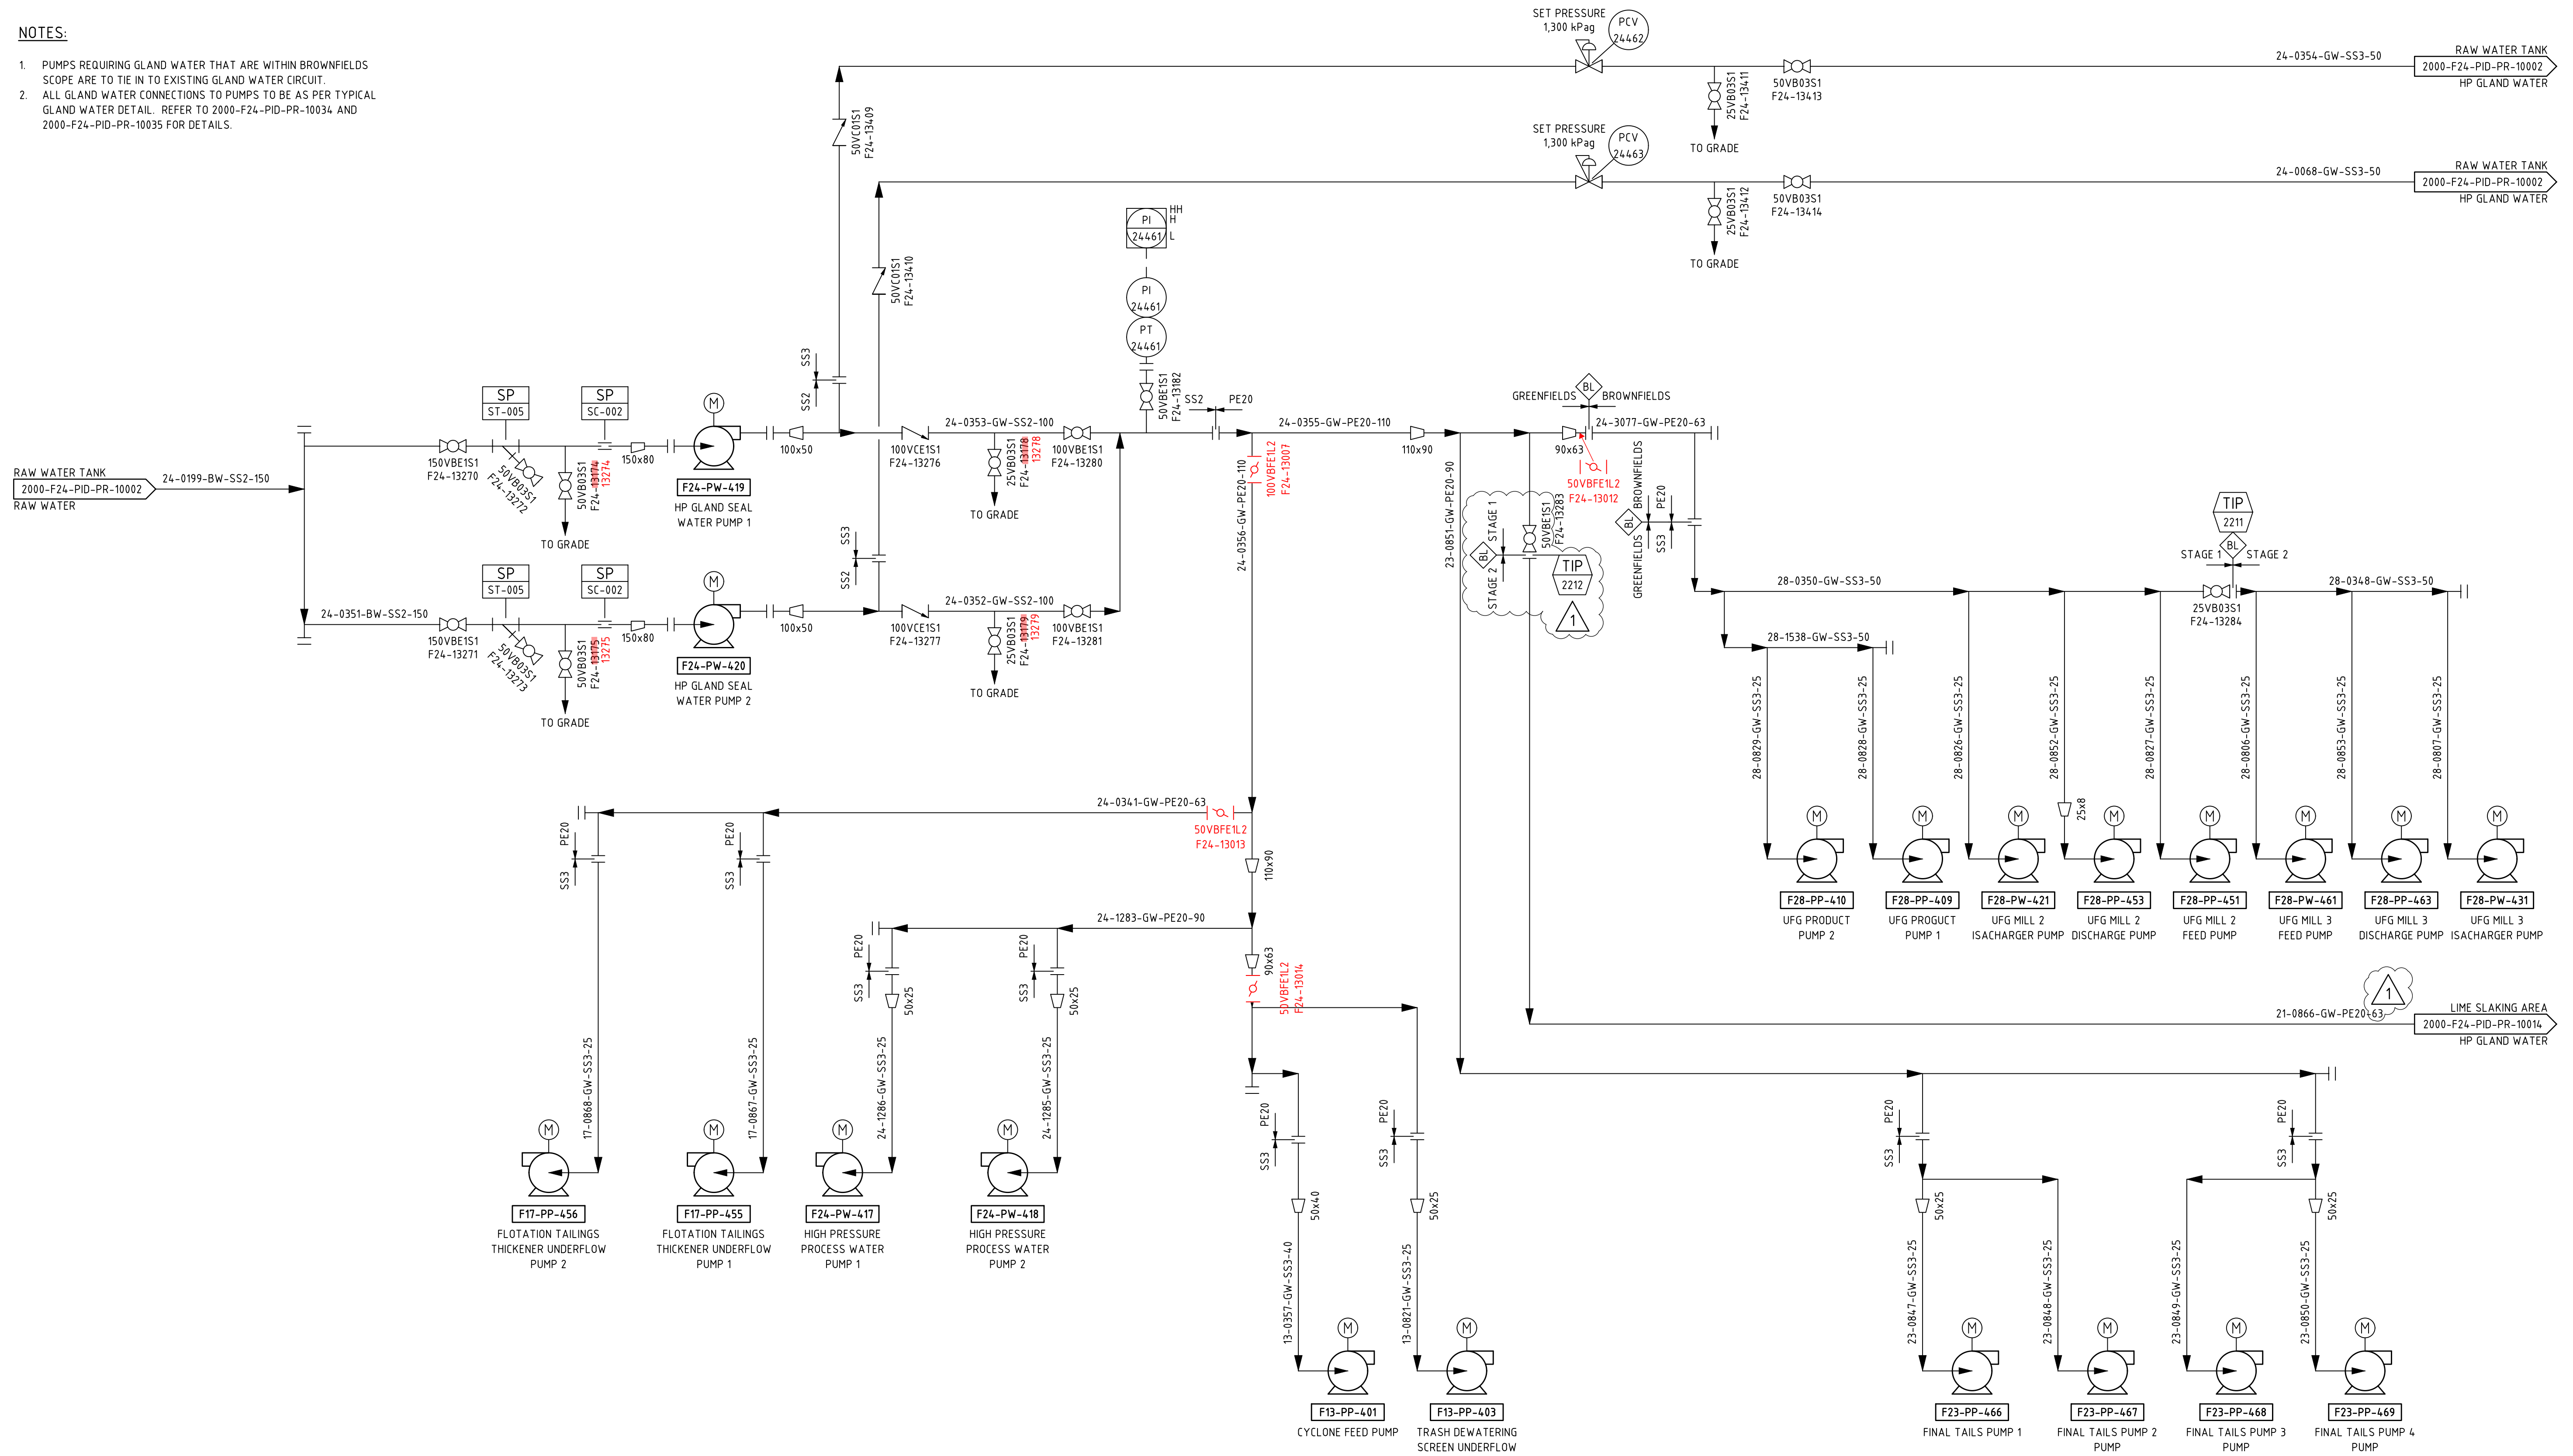

ORG No.	REFERENCES	REV	DATE	DESCRIPTION	DRAW	CHECK	DESIGN	TECH APP	PROJ APP
2000-F00-PID-PR-10007	LEGEND SHEET 7 - PIPING AND INSTRUMENTATION DIAGRAM								
2000-F00-PID-PR-10006	LEGEND SHEET 6 - PIPING AND INSTRUMENTATION DIAGRAM								
2000-F00-PID-PR-10005	LEGEND SHEET 5 - PIPING AND INSTRUMENTATION DIAGRAM								
2000-F00-PID-PR-10004	LEGEND SHEET 4 - PIPING AND INSTRUMENTATION DIAGRAM								
2000-F00-PID-PR-10003	LEGEND SHEET 3 - PIPING AND INSTRUMENTATION DIAGRAM								
2000-F00-PID-PR-10002	LEGEND SHEET 2 - PIPING AND INSTRUMENTATION DIAGRAM								
2000-F00-PID-PR-10001	LEGEND SHEET 1 - PIPING AND INSTRUMENTATION DIAGRAM								
1	10JUL25	GENERAL REVISIONS AS NOTED			AH	MM	JBe	LV	DM
0	25MAR25	APPROVED FOR CONSTRUCTION			AH	JDM	JBe	LV	DM



INFORMATION AND REPRESENTATIONS ON THIS DRAWING ARE THE INTELLECTUAL PROPERTY OF PRIMERO UNLESS SPECIFICALLY IDENTIFIED OTHERWISE. ALL RIGHTS INCLUDING USE RESERVED

PROJECT:	NORTHERN STAR RESOURCES LTD KCGM GROWTH PROJECT		
TITLE:	AIR & WATER SERVICES GLAND WATER - SHEET 2 PIPING AND INSTRUMENTATION DIAGRAM		
SHEET	A1	SCALE	NTS
DRG No.	2000-F24-PID-PR-10004		REVISION
			1