


D:\CAD PROJECTS\235 NORTHERN STAR RESOURCES LTD\23517 KCGM GROWTH PROJECT\03 DELIVERABLES\PR\PID\ISSUED\HISTORY\05.09.2025 - PID SIGNING\NATIVES\2000-F24-PID-PR-10013_2.DWG 08SEP25 4:11PM ANNE HOYNE

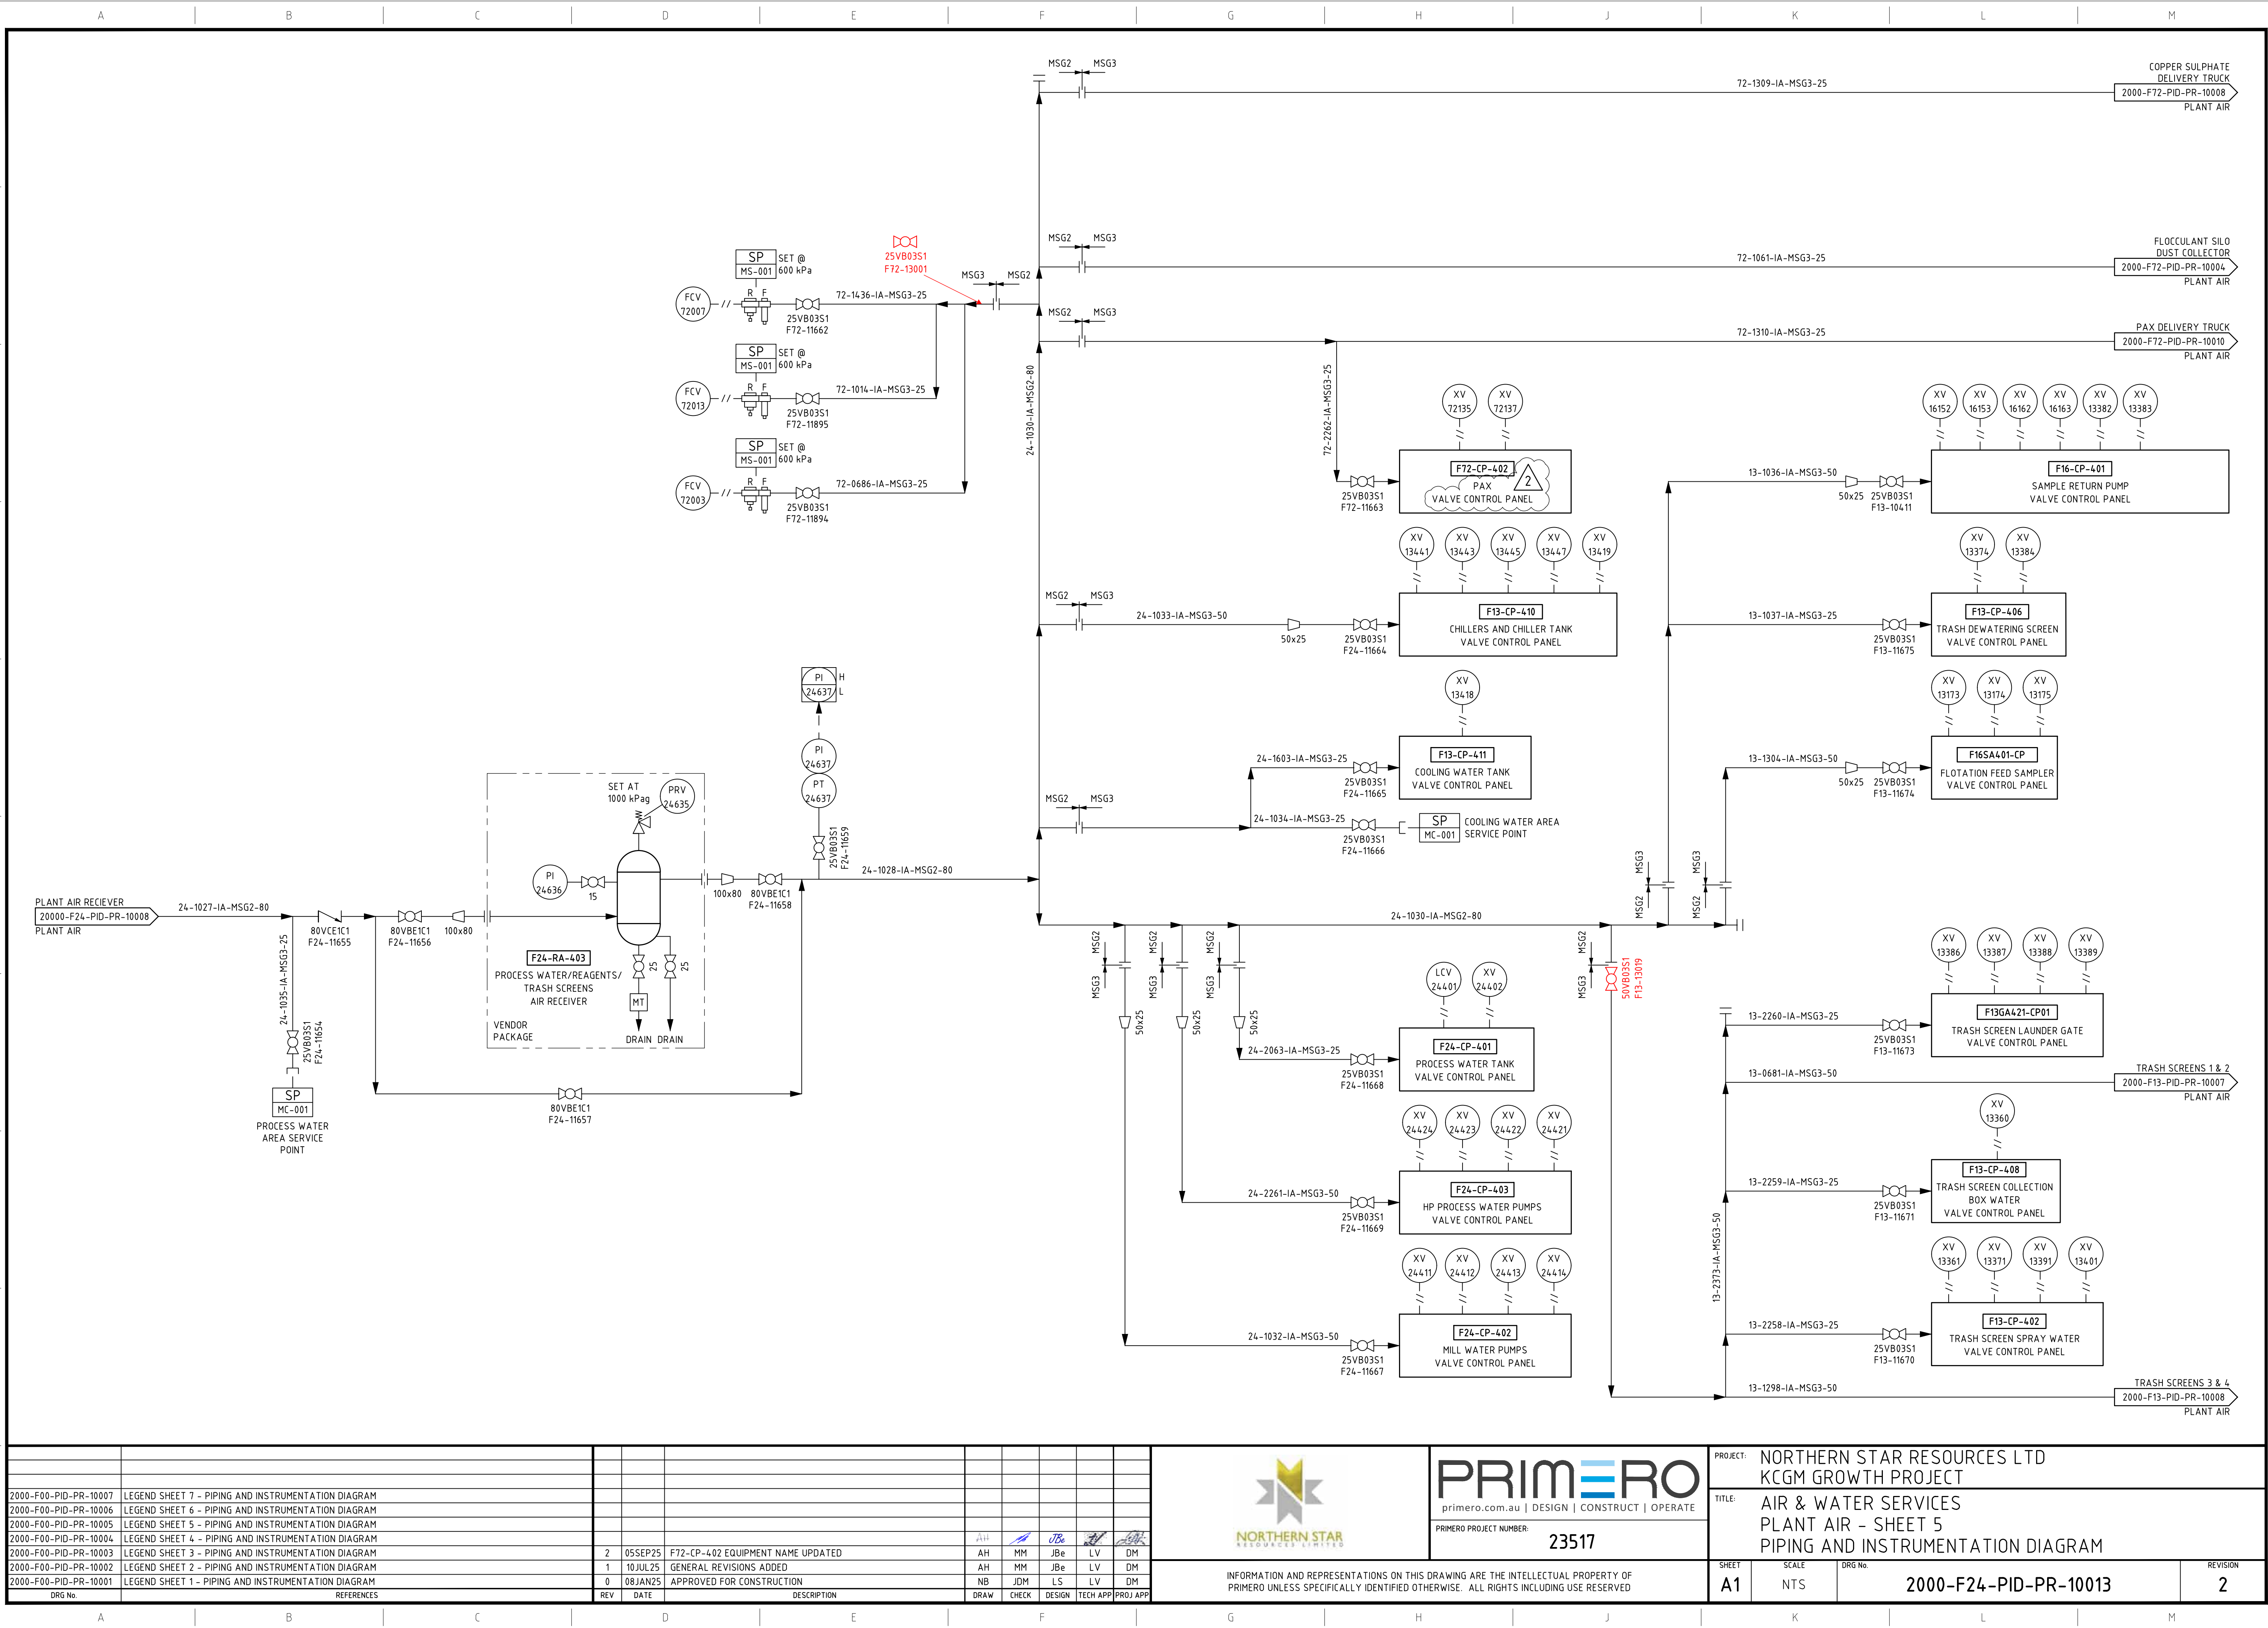

DRG No.	REFERENCES	REV	DATE	DESCRIPTION	DRAW	CHECK	DESIGN	TECH APP	PROJ APP
2000-F00-PID-PR-10007	LEGEND SHEET 7 - PIPING AND INSTRUMENTATION DIAGRAM								
2000-F00-PID-PR-10006	LEGEND SHEET 6 - PIPING AND INSTRUMENTATION DIAGRAM								
2000-F00-PID-PR-10005	LEGEND SHEET 5 - PIPING AND INSTRUMENTATION DIAGRAM								
2000-F00-PID-PR-10004	LEGEND SHEET 4 - PIPING AND INSTRUMENTATION DIAGRAM								
2000-F00-PID-PR-10003	LEGEND SHEET 3 - PIPING AND INSTRUMENTATION DIAGRAM								
2000-F00-PID-PR-10002	LEGEND SHEET 2 - PIPING AND INSTRUMENTATION DIAGRAM								
2000-F00-PID-PR-10001	LEGEND SHEET 1 - PIPING AND INSTRUMENTATION DIAGRAM								
2	05SEP25	F72-CP-402 EQUIPMENT NAME UPDATED	AH	MM	JBe	LV	DM		
1	10JUL25	GENERAL REVISIONS ADDED	AH	MM	JBe	LV	DM		
0	08JAN25	APPROVED FOR CONSTRUCTION	NB	JDM	LS	LV	DM		

		 primero.com.au DESIGN CONSTRUCT OPERATE		PROJECT: NORTHERN STAR RESOURCES LTD KCGM GROWTH PROJECT
PRIMERO PROJECT NUMBER: 23517		TITLE: AIR & WATER SERVICES PLANT AIR - SHEET 5 PIPING AND INSTRUMENTATION DIAGRAM		
SHEET A1	SCALE NTS	DRG No. 2000-F24-PID-PR-10013	REVISION 2	