


D:\CAD PROJECTS\235 NORTHERN STAR RESOURCES LTD\23517 KCGM GROWTH PROJECT\03 DELIVERABLES\PR\PID\2000-F24-PID-PR-10034.DWG 25MAR25 14:7PM ANNE.HOYNE

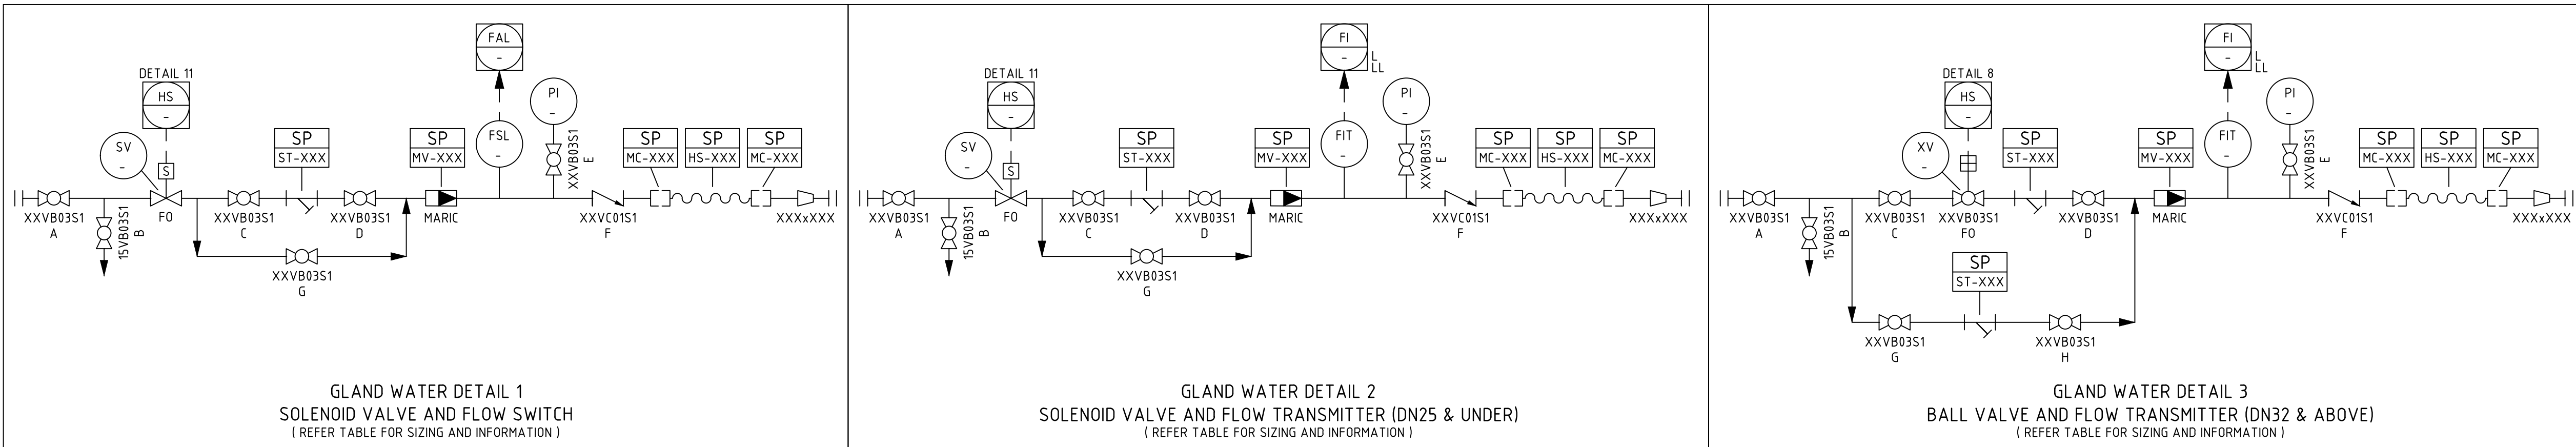

- NOTES:
- REFER TO 2000-F24-PID-PR-10003 AND 2000-F24-PID-PR-10014 FOR THE GREENFIELDS LOW PRESSURE GLAND SEAL WATER CIRCUIT.
  - REFER TO 2000-F24-PID-PR-10004 AND 2000-F24-PID-PR-10014 FOR THE GREENFIELDS HIGH PRESSURE GLAND SEAL WATER CIRCUIT.
  - PUMPS REQUIRING GLAND WATER THAT ARE WITHIN BROWNFIELDS SCOPE ARE TO TIE IN TO THE EXISTING GLAND WATER CIRCUIT. REFER TO 2000-F75-PID-PR-10007 FOR THE BROWNFIELDS GLAND WATER CIRCUIT.
  - VALVE SIZE MATCHES LINE SIZE UNLESS OTHERWISE SPECIFIED IN THE RELEVANT GLAND WATER DETAIL.
  - LP REFERS TO THE GREENFIELDS LOW PRESSURE GLAND WATER CIRCUIT, HP REFERS TO THE GREENFIELDS HIGH PRESSURE GLAND WATER CIRCUIT AND BF REFERS TO THE BROWNFIELDS GLAND WATER CIRCUIT.
  - GLAND WATER CONNECTION TO PUMPS F24-PW-401/402 IS A DN25 FLANGED CONNECTION. CONNECTING FLANGE DRILLED TO SUIT DN25 TBE PIPE NIPPLE FOR MINSUP CONNECTION.
  - REDUCING BUSH REQUIRED BETWEEN HOSE AND PUMP CONNECTION.

| EQUIPMENT DETAILS |                                                       |                       |                     |        |                    | MANUAL VALVE TAG NUMBERS |           |           |           |           |           |           |           | INSTRUMENTATION |          |       | SPECIAL PIPING ITEMS |       |       |       |         |
|-------------------|-------------------------------------------------------|-----------------------|---------------------|--------|--------------------|--------------------------|-----------|-----------|-----------|-----------|-----------|-----------|-----------|-----------------|----------|-------|----------------------|-------|-------|-------|---------|
| EQUIPMENT NUMBER  | PUMP DESCRIPTION                                      | P&ID NUMBER           | LINE SIZE<br>NOTE 4 | DETAIL | HP/LP/BF<br>NOTE 5 | A                        | B         | C         | D         | E         | F         | G         | H         | XV/SV/HS        | FSL/FAL  | PI    | SP-MV                | SP-ST | SP-MC | SP-HS | REDUCER |
| F14-PP-421        | INTENSIVE CYANIDE LEACH REACTOR DISCHARGE PUMP        | 2000-F14-PID-PR-10003 | 25                  | 1      | LP                 | F14-13151                | F14-13152 | F14-13153 | F14-13154 | F14-13156 | F14-13157 | F14-13155 | -         | 14118           | 14119    | 14120 | -                    | 011   | 001   | 015   | 25x15   |
| F16-PP-515        | FLOTATION CELL DRAIN PUMP                             | 2000-F16-PID-PR-10003 | 25                  | 1      | LP                 | F16-13158                | F16-13159 | F16-13160 | F16-13161 | F16-13163 | F16-13164 | F16-13162 | -         | 16357           | 16358    | 16359 | 004                  | 011   | 001   | 015   | 25x15   |
| F16-PP-638        | SAMPLE RETURN PUMP 1                                  | 2000-F16-PID-PR-10005 | 25                  | 1      | LP                 | F16-13165                | F16-13166 | F16-13167 | F16-13168 | F16-13170 | F16-13171 | F16-13169 | -         | 16155           | 16156    | 16157 | 001                  | 011   | 001   | 015   | 25x8    |
| F16-PP-639        | SAMPLE RETURN PUMP 2                                  | 2000-F16-PID-PR-10005 | 25                  | 1      | LP                 | F16-13172                | F16-13173 | F16-13174 | F16-13175 | F16-13177 | F16-13178 | F16-13176 | -         | 16165           | 16166    | 16167 | 001                  | 011   | 001   | 015   | 25x8    |
| F18-PP-407        | FINAL CONCENTRATE PUMP 1                              | 2000-F18-PID-PR-10001 | 25                  | 1      | LP                 | F18-13179                | F18-13180 | F18-13181 | F18-13182 | F18-13184 | F18-13185 | F18-13183 | -         | 18500           | 18501    | 18502 | 004                  | 011   | 001   | 015   | 25x15   |
| F18-PP-408        | FINAL CONCENTRATE PUMP 2                              | 2000-F18-PID-PR-10001 | 25                  | 1      | LP                 | F18-13186                | F18-13187 | F18-13188 | F18-13189 | F18-13191 | F18-13192 | F18-13190 | -         | 18504           | 18505    | 18506 | 004                  | 011   | 001   | 015   | 25x15   |
| F18-PP-501        | CLEANER FLOTATION CELL RECIRCULATION PUMP 1           | 2000-F18-PID-PR-10001 | 25                  | 1      | LP                 | F18-13193                | F18-13194 | F18-13195 | F18-13196 | F18-13198 | F18-13199 | F18-13197 | -         | 18508           | 18509    | 18510 | 002                  | 011   | 001   | 015   | N/A     |
| F18-PP-502        | CLEANER FLOTATION CELL RECIRCULATION PUMP 2           | 2000-F18-PID-PR-10001 | 25                  | 1      | LP                 | F18-13200                | F18-13201 | F18-13202 | F18-13203 | F18-13205 | F18-13206 | F18-13204 | -         | 18512           | 18513    | 18514 | 002                  | 011   | 001   | 015   | N/A     |
| F18-PP-511        | CLEANER-SCAVENGER FLOTATION CELL RECIRCULATION PUMP 1 | 2000-F18-PID-PR-10003 | 25                  | 1      | LP                 | F18-13207                | F18-13208 | F18-13209 | F18-13210 | F18-13212 | F18-13213 | F18-13211 | -         | 18524           | 18525    | 18526 | 002                  | 011   | 001   | 015   | N/A     |
| F18-PP-512        | CLEANER-SCAVENGER FLOTATION CELL RECIRCULATION PUMP 2 | 2000-F18-PID-PR-10003 | 25                  | 1      | LP                 | F18-13214                | F18-13215 | F18-13216 | F18-13217 | F18-13219 | F18-13220 | F18-13218 | -         | 18528           | 18529    | 18530 | 002                  | 011   | 001   | 015   | N/A     |
| F18-PP-513        | CLEANER-SCAVENGER FLOTATION CELL TAILS PUMP 1         | 2000-F18-PID-PR-10003 | 25                  | 1      | LP                 | F18-13221                | F18-13222 | F18-13223 | F18-13224 | F18-13226 | F18-13227 | F18-13225 | -         | 18532           | 18533    | 18534 | 002                  | 011   | 001   | 015   | N/A     |
| F18-PP-514        | CLEANER-SCAVENGER FLOTATION CELL TAILS PUMP 2         | 2000-F18-PID-PR-10003 | 25                  | 1      | LP                 | F18-13228                | F18-13229 | F18-13230 | F18-13231 | F18-13233 | F18-13234 | F18-13232 | -         | 18536           | 18537    | 18538 | 002                  | 011   | 001   | 015   | N/A     |
| F24-PW-401        | MILL WATER PUMP 1                                     | 2000-F24-PID-PR-10001 | 25                  | 1      | LP                 | F24-13235                | F24-13236 | F24-13237 | F24-13238 | F24-13240 | F24-13241 | F24-13239 | -         | 24512           | 24510    | 24511 | 002                  | 011   | 001   | 015   | NOTE 6  |
| F24-PW-402        | MILL WATER PUMP 2                                     | 2000-F24-PID-PR-10001 | 25                  | 1      | LP                 | F24-13242                | F24-13243 | F24-13244 | F24-13245 | F24-13247 | F24-13248 | F24-13246 | -         | 24515           | 24513    | 24514 | 002                  | 011   | 001   | 015   | NOTE 6  |
| F13-PP-401        | CYCLONE FEED PUMP                                     | 2000-F13-PID-PR-10002 | 40                  | 3      | HP                 | F13-10900                | F13-10901 | F13-10902 | F13-10903 | F13-10906 | F13-10907 | F13-10904 | F13-10905 | 13460           | FIT13461 | 13462 | 003                  | 012   | 011   | 017   | 40x32   |
| F13-PP-403        | TRASH DEWATERING SCREEN UNDERFLOW PUMP                | 2000-F13-PID-PR-10007 | 25                  | 1      | HP                 | F13-10908                | F13-10909 | F13-10910 | F13-10911 | F13-10913 | F13-10914 | F13-10912 | -         | 13464           | 13465    | 13466 | 005                  | 011   | 001   | 015   | 25x8    |
| F17-PP-455        | FLOTATION TAILINGS THICKENER UNDERFLOW PUMP 1         | 2000-F17-PID-PR-10002 | 25                  | 2      | HP                 | F17-10915                | F17-10916 | F17-10917 | F17-10918 | F17-10920 | F17-10921 | F17-10919 | -         | 17104           | FIT17105 | 17106 | 002                  | 011   | 001   | 015   | N/A     |
| F17-PP-456        | FLOTATION TAILINGS THICKENER UNDERFLOW PUMP 2         | 2000-F17-PID-PR-10002 | 25                  | 2      | HP                 | F17-10922                | F17-10923 | F17-10924 | F17-10925 | F17-10927 | F17-10928 | F17-10926 | -         | 17114           | FIT17115 | 17116 | 002                  | 011   | 001   | 015   | N/A     |
| F23-PP-466        | FINAL TAILS PUMP 1                                    | 2000-F23-PID-PR-10002 | 25                  | 2      | HP                 | F23-10929                | F23-10930 | F23-10931 | F23-10932 | F23-10934 | F23-10935 | F23-10933 | -         | 23480           | FIT23481 | 23482 | 002                  | 011   | 001   | 015   | N/A     |
| F23-PP-467        | FINAL TAILS PUMP 2                                    | 2000-F23-PID-PR-10002 | 25                  | 2      | HP                 | F23-10936                | F23-10937 | F23-10938 | F23-10939 | F23-10941 | F23-10942 | F23-10940 | -         | 23484           | FIT23485 | 23486 | 002                  | 011   | 001   | 015   | N/A     |
| F23-PP-468        | FINAL TAILS PUMP 3                                    | 2000-F23-PID-PR-10002 | 25                  | 2      | HP                 | F23-10943                | F23-10944 | F23-10945 | F23-10946 | F23-10948 | F23-10949 | F23-10947 | -         | 23488           | FIT23489 | 23490 | 002                  | 011   | 001   | 015   | N/A     |
| F23-PP-469        | FINAL TAILS PUMP 4                                    | 2000-F23-PID-PR-10002 | 25                  | 2      | HP                 | F23-10950                | F23-10951 | F23-10952 | F23-10953 | F23-10955 | F23-10956 | F23-10954 | -         | 23492           | FIT23493 | 23494 | 002                  | 011   | 001   | 015   | N/A     |
| F24-PW-417        | HIGH PRESSURE PROCESS WATER PUMP 1                    | 2000-F24-PID-PR-10001 | 25                  | 1      | HP                 | F24-10957                | F24-10958 | F24-10959 | F24-10960 | F24-10962 | F24-10963 | F24-10961 | -         | 24518           | 24516    | 24517 | 006                  | 011   | 001   | 015   | N/A     |
| F24-PW-418        | HIGH PRESSURE PROCESS WATER PUMP 2                    | 2000-F24-PID-PR-10001 | 25                  | 1      | HP                 | F24-10964                | F24-10965 | F24-10966 | F24-10967 | F24-10969 | F24-10970 | F24-10968 | -         | 24521           | 24519    | 24520 | 006                  | 011   | 001   | 015   | 32x25   |
| F28-PP-409        | UFG PRODUCT PUMP 1                                    | 2000-F28-PID-PR-10005 | 25                  | 1      | HP                 | F28-10971                | F28-10972 | F28-10973 | F28-10974 | F28-10976 | F28-10977 | F28-10975 | -         | 28400           | 28401    | 28402 | 004                  | 011   | 001   | 015   | 25x15   |
| F28-PP-410        | UFG PRODUCT PUMP 2                                    | 2000-F28-PID-PR-10005 | 25                  | 1      | HP                 | F28-10978                | F28-10979 | F28-10980 | F28-10981 | F28-10983 | F28-10984 | F28-10982 | -         | 28404           | 28405    | 28406 | 004                  | 011   | 001   | 015   | 25x15   |
| F28-PP-453        | UFG MILL 2 DISCHARGE PUMP                             | 2000-F28-PID-PR-10002 | 25                  | 1      | HP                 | F28-11900                | F28-11901 | F28-11902 | F28-11903 | F28-11905 | F28-11906 | F28-11904 | -         | 28412           | 28413    | 28414 | 004                  | 011   | 001   | 015   | 25x15   |
| F28-PP-451        | UFG MILL 2 FEED PUMP                                  | 2000-F28-PID-PR-10001 | 25                  | 1      | HP                 | F28-11914                | F28-11915 | F28-11916 | F28-11917 | F28-11919 | F28-11920 | F28-11918 | -         | 28408           | 28409    | 28410 | 005                  | 011   | 001   | 015   | 25x8    |
| F28-PW-421        | UFG MILL 2 ISACHARGER PUMP                            | 2000-F28-PID-PR-10001 | 25                  | 1      | HP                 | F28-11928                | F28-11929 | F28-11930 | F28-11931 | F28-11933 | F28-11934 | F28-11932 | -         | 28416           | 28417    | 28418 | 002                  | 011   | 001   | 015   | 25x10   |
| F30-PP-417        | CONCENTRATE THICKENER U/F PUMP 1                      | 2000-F30-PID-PR-10002 | 25                  | 1      | BF                 | F30-13249                | F30-13250 | F30-13251 | F30-13252 | F30-13254 | F30-13255 | F30-13253 | -         | 30447           | 30448    | 30449 | 001                  | 011   | 001   | 015   | 25x8    |
| F30-PP-418        | CONCENTRATE THICKENER U/F PUMP 2                      | 2000-F30-PID-PR-10002 | 25                  | 1      | BF                 | F30-13256                | F30-13257 | F30-13258 | F30-13259 | F30-13261 | F30-13262 | F30-13260 | -         | 30452           | 30453    | 30454 | 001                  | 011   | 001   | 015   | 25x8    |
| F35-PP-448        | UFG CIRCUIT 2 FEED PUMP                               | 2000-F35-PID-PR-10002 | 25                  | 1      | BF                 | F35-13263                | F35-13264 | F35-13265 | F35-13266 | F35-13268 | F35-13269 | F35-13267 | -         | 35437           | 35438    | 35439 | 001                  | 011   | 001   | 015   | 25x8    |

| |
|---|
| |
|---|