
NOTES:

1. DELETED.
2. CONNECTION IS DN65 VICTAULIC.
3. TANK TO BE INSULATED.

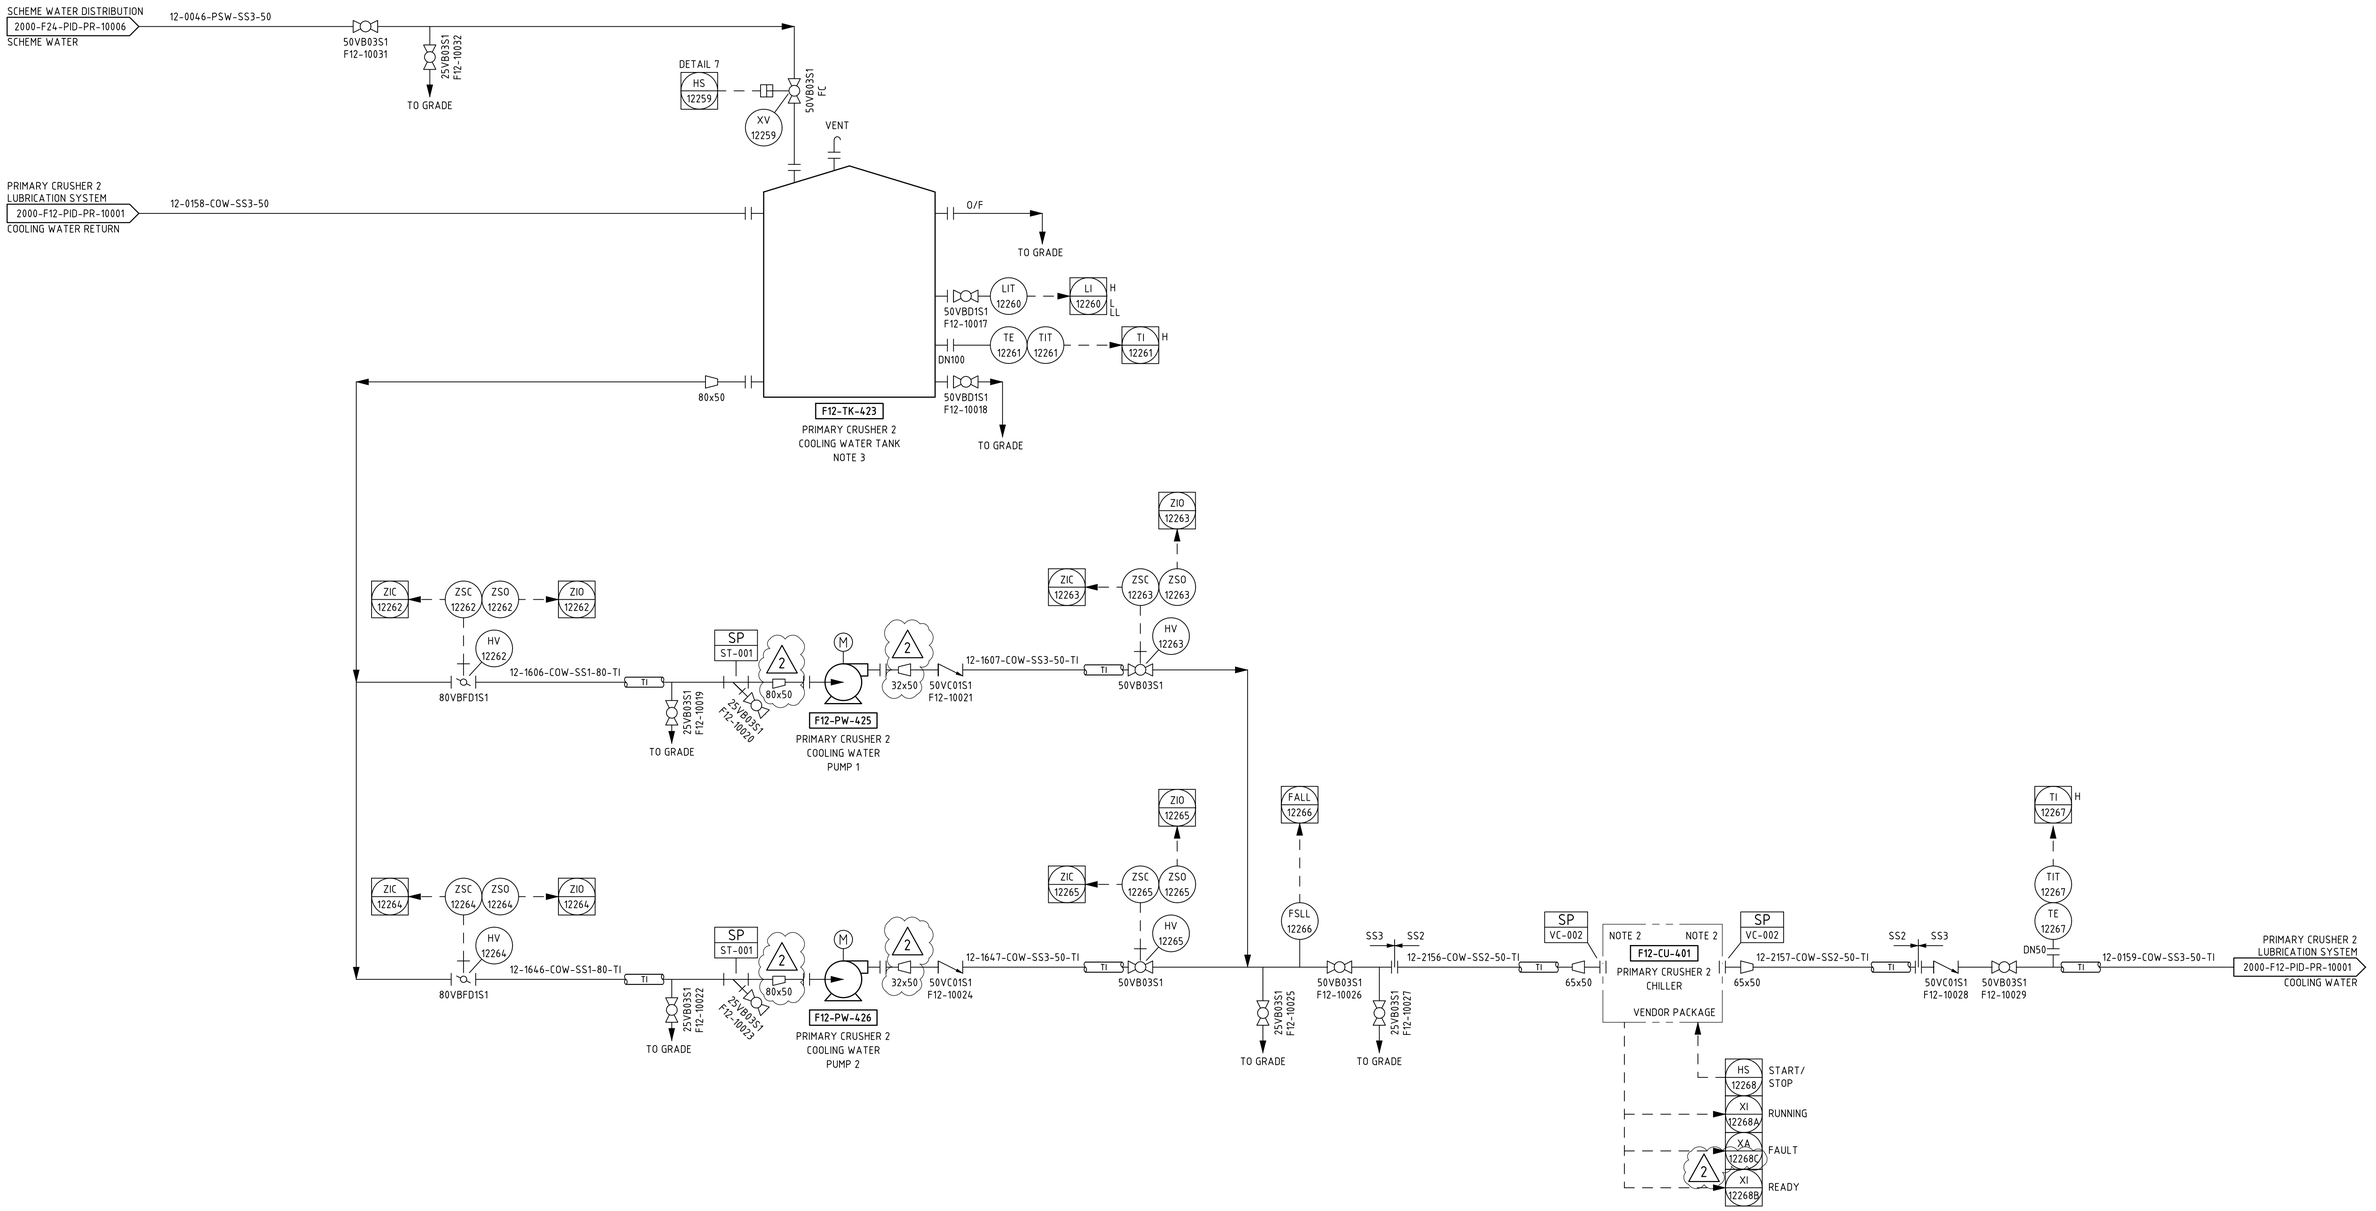


| DRG No. | REFERENCES | REV | DATE | DESCRIPTION | DRAW | CHECK | DESIGN | TECH APP | PROJ APP |
|---|---|---|---|---|---|---|---|---|---|
| | | | | | | | | | |
| | | | | | | | | | |
| | | | | | | | | | |
| 2000-F00-PID-PR-10007 | LEGEND SHEET 7 - PIPING AND INSTRUMENTATION DIAGRAM | | | | | | | | |
| 2000-F00-PID-PR-10006 | LEGEND SHEET 6 - PIPING AND INSTRUMENTATION DIAGRAM | | | | | | | | |
| 2000-F00-PID-PR-10005 | LEGEND SHEET 5 - PIPING AND INSTRUMENTATION DIAGRAM | | | | | | | | |
| 2000-F00-PID-PR-10004 | LEGEND SHEET 4 - PIPING AND INSTRUMENTATION DIAGRAM | | | | AH | | JBe | | |
| 2000-F00-PID-PR-10003 | LEGEND SHEET 3 - PIPING AND INSTRUMENTATION DIAGRAM | 2 | 05SEP25 | REDUCERS AND GENERAL REVISIONS ADDED | AH | MM | JBe | BS | DM |
| 2000-F00-PID-PR-10002 | LEGEND SHEET 2 - PIPING AND INSTRUMENTATION DIAGRAM | 1 | 31OCT24 | RE-ISSUED FOR CONSTRUCTION | NB | JB | LV | LS | DM |
| 2000-F00-PID-PR-10001 | LEGEND SHEET 1 - PIPING AND INSTRUMENTATION DIAGRAM | 0 | 26JUL24 | ISSUED FOR CONSTRUCTION | AK | JB | RB | LS | DM |

NORTHERN STAR RESOURCES LIMITED

PRIMERO
primero.com.au | DESIGN | CONSTRUCT | OPERATE

PRIMERO PROJECT NUMBER: 23517

INFORMATION AND REPRESENTATIONS ON THIS DRAWING ARE THE INTELLECTUAL PROPERTY OF PRIMERO UNLESS SPECIFICALLY IDENTIFIED OTHERWISE. ALL RIGHTS INCLUDING USE RESERVED

PROJECT: NORTHERN STAR RESOURCES LTD
KCGM GROWTH PROJECT

TITLE: PRIMARY CRUSHING
PRIMARY CRUSHING - SHEET 3 - STAGE 1
PIPING AND INSTRUMENTATION DIAGRAM

| SHEET | SCALE | DRG No. | REVISION |
|---|---|---|---|
| A1 | NTS | 2000-F12-PID-PR-10003 | 2 |

O:\CAD PROJECTS\23S NORTHERN STAR RESOURCES LTD\23517 KCGM GROWTH PROJECT\03 DELIVERABLES\PR\PID\2000-F12-PID-PR-10003_2.DWG 03SEP25 11:01AM ANNE.HOYNE