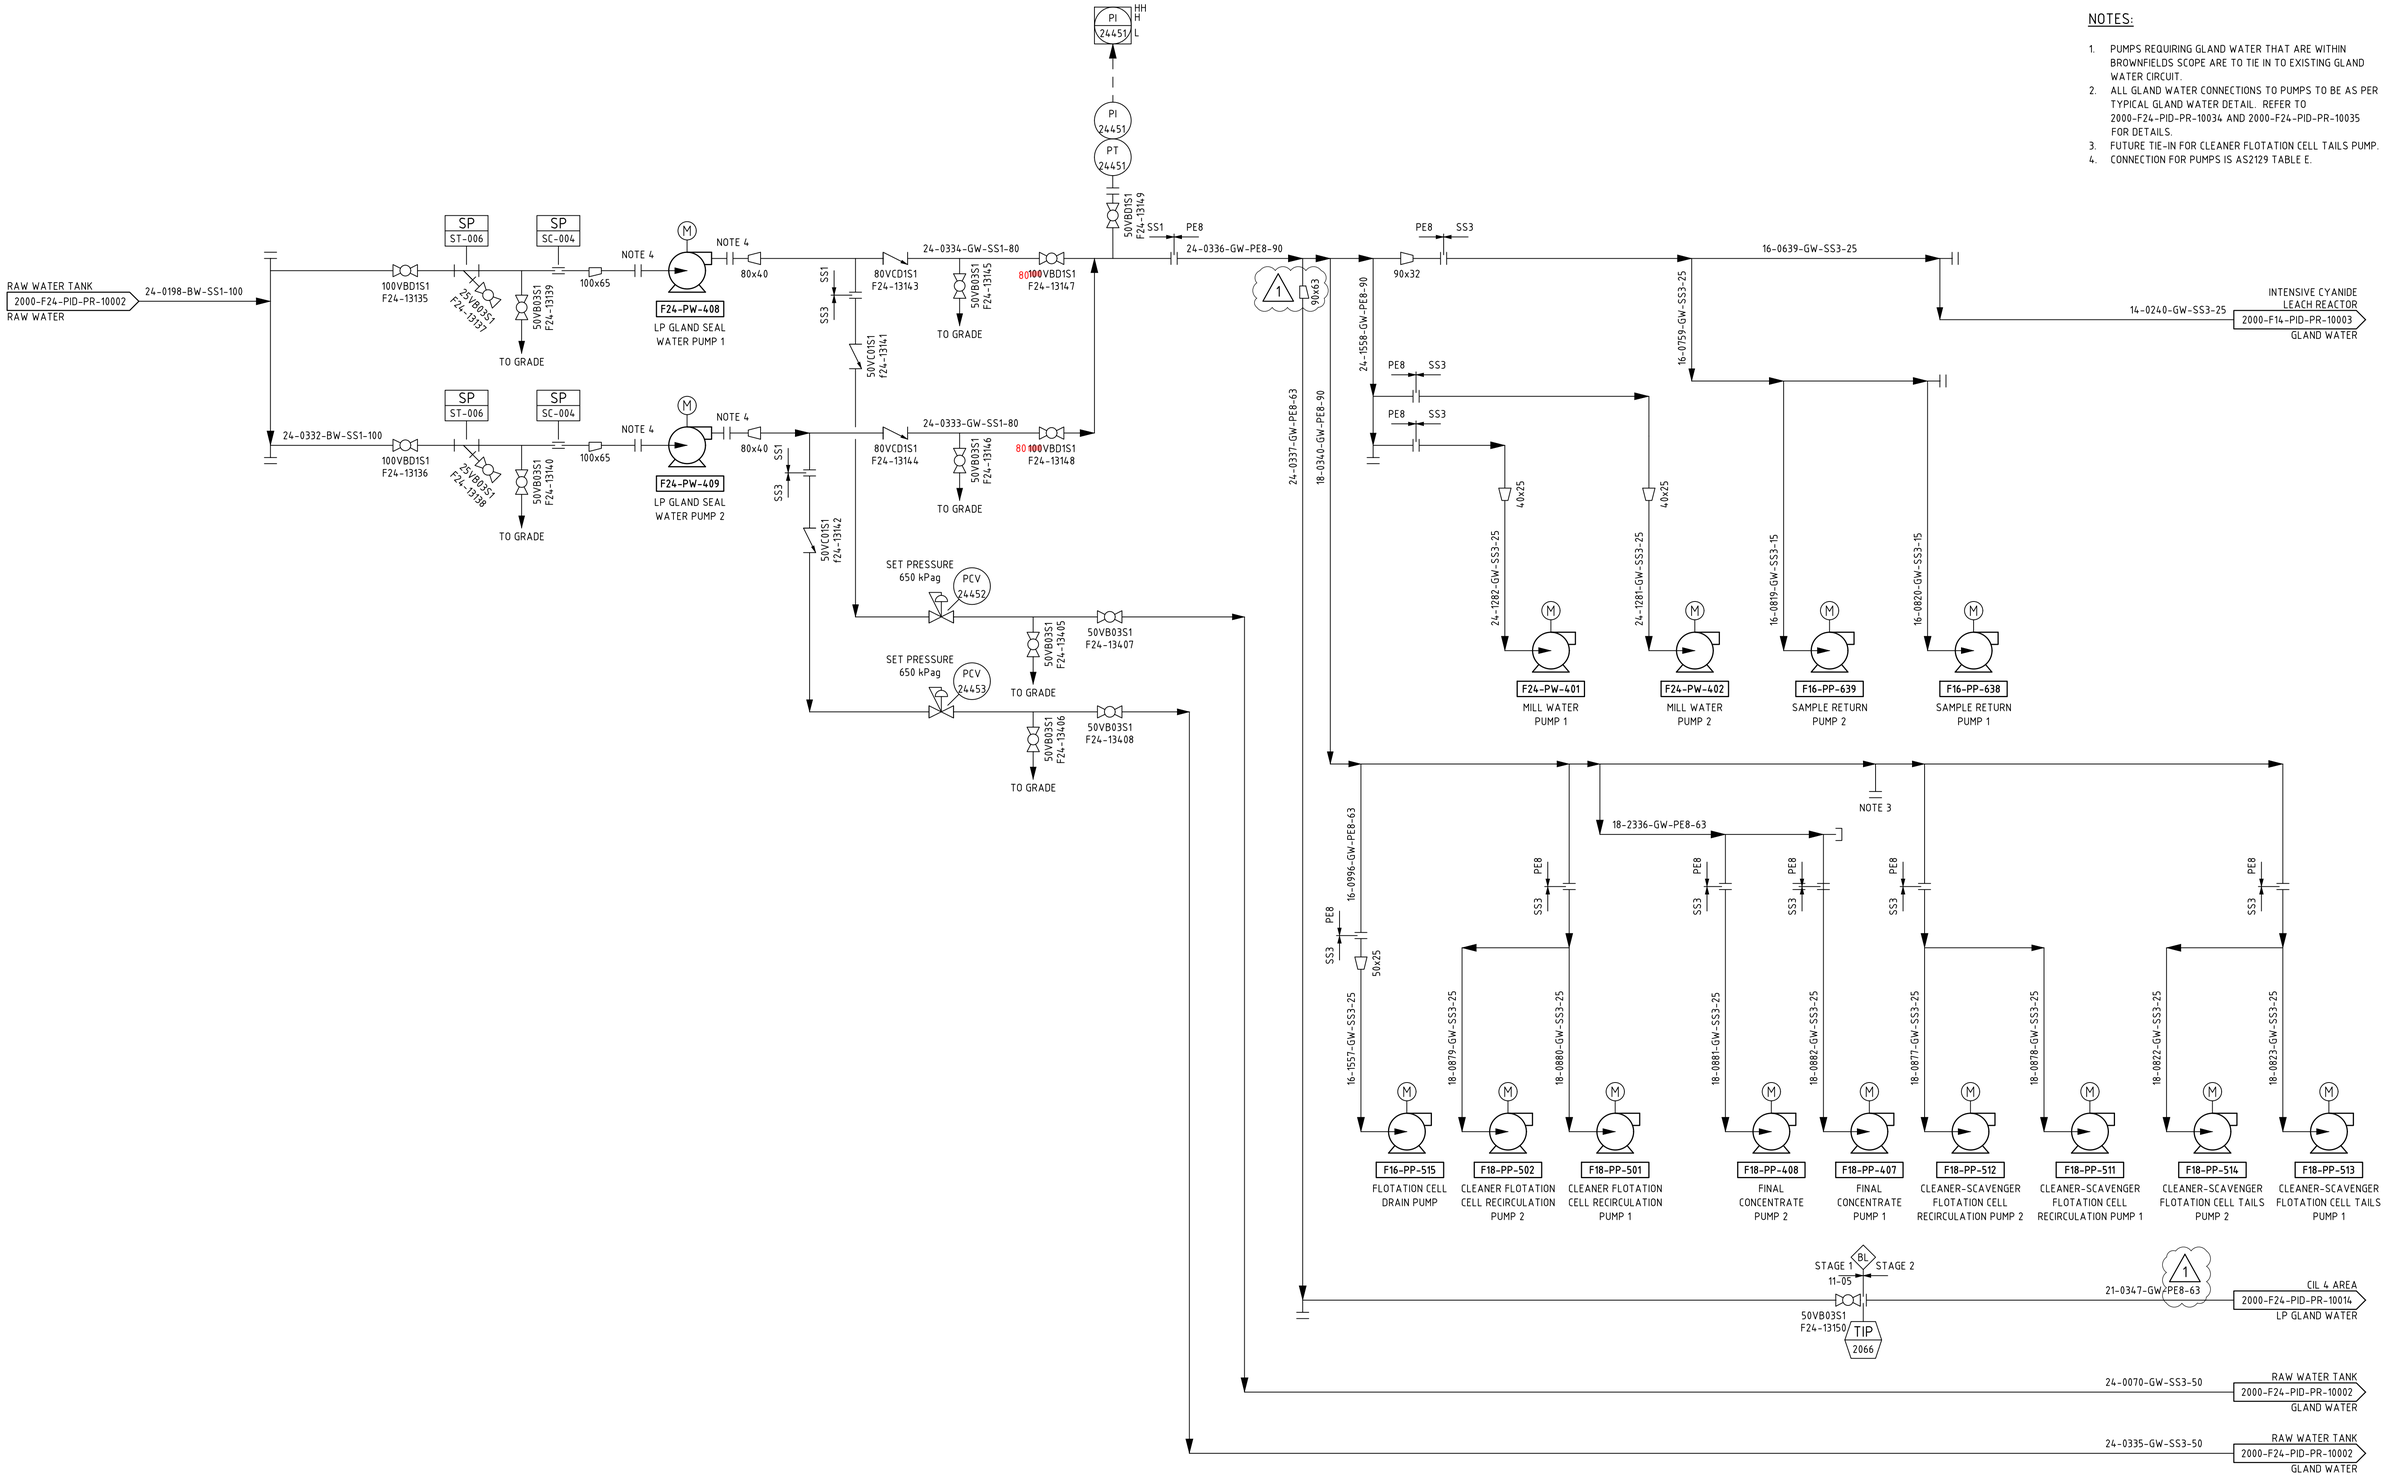


NOTES:

1. PUMPS REQUIRING GLAND WATER THAT ARE WITHIN BROWNFIELDS SCOPE ARE TO TIE IN TO EXISTING GLAND WATER CIRCUIT.
2. ALL GLAND WATER CONNECTIONS TO PUMPS TO BE AS PER TYPICAL GLAND WATER DETAIL. REFER TO 2000-F24-PID-PR-10034 AND 2000-F24-PID-PR-10035 FOR DETAILS.
3. FUTURE TIE-IN FOR CLEANER FLOTATION CELL TAILS PUMP.
4. CONNECTION FOR PUMPS IS AS2129 TABLE E.

DRG No.	REFERENCES	REV	DATE	DESCRIPTION	DRAW	CHECK	DESIGN	TECH APP	PROJ APP
2000-F00-PID-PR-10007	LEGEND SHEET 7 - PIPING AND INSTRUMENTATION DIAGRAM								
2000-F00-PID-PR-10006	LEGEND SHEET 6 - PIPING AND INSTRUMENTATION DIAGRAM								
2000-F00-PID-PR-10005	LEGEND SHEET 5 - PIPING AND INSTRUMENTATION DIAGRAM								
2000-F00-PID-PR-10004	LEGEND SHEET 4 - PIPING AND INSTRUMENTATION DIAGRAM								
2000-F00-PID-PR-10003	LEGEND SHEET 3 - PIPING AND INSTRUMENTATION DIAGRAM				AH	MM	JBe	LV	DM
2000-F00-PID-PR-10002	LEGEND SHEET 2 - PIPING AND INSTRUMENTATION DIAGRAM	1	10JUL25	LINE NUMBER CHANGE	AH	MM	JBe	LV	DM
2000-F00-PID-PR-10001	LEGEND SHEET 1 - PIPING AND INSTRUMENTATION DIAGRAM	0	25MAR25	APPROVED FOR CONSTRUCTION	AH	JDM	JBe	LV	DM

NORTHERN STAR RESOURCES LIMITED

PRIMERO
primero.com.au | DESIGN | CONSTRUCT | OPERATE

PRIMERO PROJECT NUMBER: 23517

INFORMATION AND REPRESENTATIONS ON THIS DRAWING ARE THE INTELLECTUAL PROPERTY OF PRIMERO UNLESS SPECIFICALLY IDENTIFIED OTHERWISE. ALL RIGHTS INCLUDING USE RESERVED

PROJECT: NORTHERN STAR RESOURCES LTD
KCGM GROWTH PROJECT

TITLE: AIR & WATER SERVICES
GLAND WATER - SHEET 1
PIPING AND INSTRUMENTATION DIAGRAM

SHEET	SCALE	DRG No.	REVISION
A1	NTS	2000-F24-PID-PR-10003	1

O:\CAD PROJECTS\23S NORTHERN STAR RESOURCES LTD\23517 KCGM GROWTH PROJECT\03 DELIVERABLES\PR\PID\2000-F24-PID-PR-10003_1.DWG 11JUL25 10:56AM ANNE.HOYNE